CONTRACT NO. B-19752

BRIDGES OVER 20' SPAN					
FEDERAL REGION NO.	STATE	PROJECT NO.	FISCAL YEAR	SHEET NO.	TOTAL SHEETS
5	IND.	EACNHI-65-3(245)III	1992	1	25

INDEX

PROJECT	STRUCTURE	TYPE	SPAN	OVER	STATION
* EACNHI-65-3(245)III	I-65-112-5723A	STEEL GIRDER	2@147'-0" SKEW 28°-47'-15" LT.	I-65 & RAMP '6S-N'	

SHEET NO.	SHEET DESIGNATION	SUBJECT	F.H.W.A. APPROVAL
1	ONE SHEET	TITLE SHEET & INDEX	
2	D1	GENERAL PLAN	
3	D2	RECONSTRUCTION DETAILS	
4	D3	REMOVAL AND RECONSTRUCTION DETAILS	
5	D4	BARRIER RAIL TYPE C4II DETAILS	
6	D5	BARRIER RAIL TYPE C4II TRANSITION DETAILS	
7	D6	G.R.E.A.T. UNIT & RECONSTRUCTION DETAILS	

B-19752 7-8

INDIANA DEPARTMENT OF TRANSPORTATION

BRIDGE PLANS

FOR SPANS OVER 20 FEET ON

FLETCHER AVE. OVER I-65 & RAMP '6S.-N.'

PROJECT EACNHI/65-3(245)III

BEGINNING AT A POINT ON THE CENTER LINE OF EXISTING FLETCHER AVE. APPROX. 97.76 FT. SOUTHEAST OF ITS INTERSECTION WITH CENTER LINE OF I-65(N.B.) AND EXTENDING IN A NORTH-WESTERLY DIRECTION FOR APPROX. 299.70 FT. TO A POINT ON CENTER LINE OF FLETCHER AVE. APPROX. 201.94 NORTHWEST OF ITS INTERSECTION WITH CENTER LINE OF I-65(N.B.) ALL IN SECTION 12, T.15N., R.3E., CENTER TOWNSHIP, MARION COUNTY.


5723A

ROADWAY LENGTH = 0.000 MI.
BRIDGE LENGTH = 0.056 MI.
TOTAL LENGTH = 0.056 MI.

MAX. GRADE = -1.62 %

NOTE:
WHENEVER NH-65-3(245)III
APPEARS ON THESE PLANS OR CONTRACT DOCUMENTS
IT SHALL BE INTERPRETED AS EACNHI-65-3(245)III

TRAFFIC DATA	I-65-112-5723A		I-65	
A.D.T. (1972)	10,900 V.P.D		(1992) 97,700 V.P.D	
A.D.T. (19 PROJECTED)	V.P.D		V.P.D	
D.H.V. (19 PROJECTED)	V.P.D		V.P.D	
TRUCKS	D.H.V.	% A.D.T. %	D.H.V.	% A.D.T. %
POSTED SPEED	30 M.P.H.		55 M.P.H.	
ACCESS CONTROL				
FUNCTIONAL CLASSIFICATION	URBAN ARTERIAL		INTERSTATE	

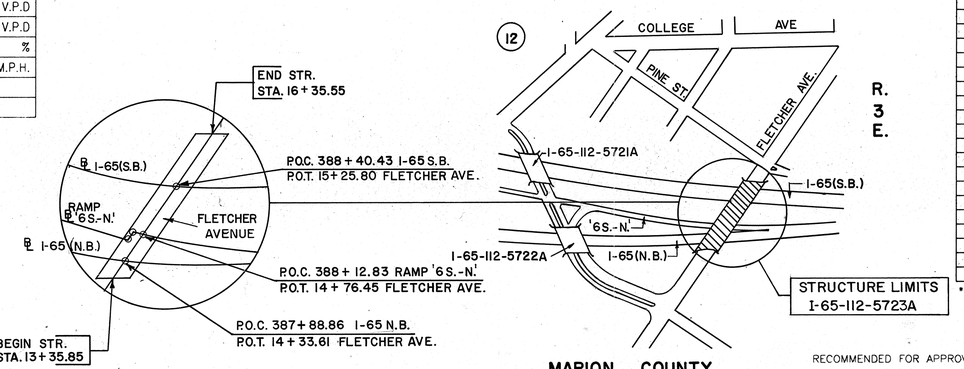

STRUCTURE LIMITS
I-65-112-5723A

MARION COUNTY
T. 15 N.

INDEX CONTINUED
STANDARD DRAWINGS

SHEET NO.	SHEET DESIGNATION	SUBJECT	F.H.W.A. APPROVAL	ADOPTED "A" REVISION "R"
	BRIDGE STD. BR5	BRIDGE RAILING CONNECTION DETAILS		
8	BRIDGE STD. C1	MISCELLANEOUS DETAILS	11-22-91	R 10-1-91
	BRIDGE STD. C2	MISCELLANEOUS DETAILS		
9	BRIDGE STD. C3	MISCELLANEOUS DETAILS	1-26-88	R 11-2-87
	BRIDGE STD. C4	PRESTRESSED CONCRETE PILES		
	BRIDGE STD. C5	PRECAST DECK PANEL DETAILS		
	BRIDGE STD. D	CASTING DETAILS AND ROADWAY DRAINS		
	BRIDGE STD. D1	ADJUSTING FRAME DETAILS FOR ROADWAY DRAINS		
	BRIDGE STD. PB1	PRESTRESSED CONCRETE TYPE I-BEAMS		
	BRIDGE STD. PB2	PRESTRESSED CONCRETE TYPE II I-BEAMS		
	BRIDGE STD. PB3	PRESTRESSED CONCRETE TYPE III I-BEAMS		
	BRIDGE STD. PB	PRESTRESSED CONCRETE TYPE I-BEAMS		
	BRIDGE STD. PB10	TOLERANCES FOR FABRICATION OF PRESTRESSED BEAMS		
	BRIDGE STD. PB11	ELASTOMERIC BEARING PADS FOR CONCRETE BEAMS		
	BRIDGE STD. R2A	BRIDGE LIGHTING DETAILS		
	BRIDGE STD. R2B	BRIDGE LIGHTING DETAILS		
	BRIDGE STD. S1	MISCELLANEOUS DETAILS		
	BRIDGE STD. SH1	STEEL SHOE DETAILS		
10	BRIDGE STD. SS-1	STRUCTURAL EXPANSION JOINTS CLASS-SS	6-20-91	A APRIL 91
11	BRIDGE STD. SS-2	STRUCTURAL EXPANSION JOINTS CLASS-SS	6-20-91	A APRIL 91
	BRIDGE STD. T SHEET A	STANDARD TEMPORARY BRIDGE		
	BRIDGE STD. T SHEET B	STANDARD TEMPORARY BRIDGE		
12	ROAD STD. SHEET A	STANDARD PAVEMENT JOINTS	*	R 3-1-90
13	ROAD STD. SHEET B	STANDARD PAVEMENT JOINTS	5-1-90	R 3-1-90
14	ROAD STD. SHEET MA-1	MISCELLANEOUS STANDARDS	7-13-88	R 6-1-88
15	ROAD STD. SHEET MA-1A	MISCELLANEOUS STANDARDS	5-1-90	R 3-1-90
	ROAD STD. SHEET MB-2	MISCELLANEOUS STANDARDS		
	ROAD STD. SHEET MB-4	MISCELLANEOUS STANDARDS		
	ROAD STD. SHEET MC	MISCELLANEOUS STANDARDS		
	ROAD STD. SHEET MC-1	MISCELLANEOUS STANDARDS		
	ROAD STD. SHEET	MISCELLANEOUS STANDARDS		
	ROAD STD. SHEET MD	MISCELLANEOUS STANDARDS		
	ROAD STD. SHEET MD	MISCELLANEOUS STANDARDS		
	ROAD STD. SHEET MD	MISCELLANEOUS STANDARDS		
16	ROAD STD. SHEET ME	MISCELLANEOUS STANDARDS	5-19-88	R 4-4-88
	ROAD STD. SHEET ME	MISCELLANEOUS STANDARDS		
	ROAD STD. SHEET ME	MISCELLANEOUS STANDARDS		
	ROAD STD. SHEET	MISCELLANEOUS STANDARDS		
	ROAD STD. SHEET MH	MISCELLANEOUS STANDARDS		
	ROAD STD. SHEET MH-1	MISCELLANEOUS STANDARDS		
	ROAD STD. SHEET MH-2	MISCELLANEOUS STANDARDS		
	ROAD STD. SHEET MI	MISCELLANEOUS STANDARDS		
	ROAD STD. SHEET MI-1	MISCELLANEOUS STANDARDS		
	ROAD STD. SHEET MI-2	MISCELLANEOUS STANDARDS		
	ROAD STD. SHEET	MISCELLANEOUS STANDARDS		
	ROAD STD. SHEET MI	MISCELLANEOUS STANDARDS		
	ROAD STD. SHEET	MISCELLANEOUS STANDARDS		
	ROAD STD. SHEET MN	MISCELLANEOUS STANDARDS		
	ROAD STD. SHEET MN-1	MISCELLANEOUS STANDARDS		
	ROAD STD. SHEET MP	MISCELLANEOUS STANDARDS		
	ROAD STD. SHEET MQ	MISCELLANEOUS STANDARDS		
17	ROAD STD. SHEET MT-2	MISCELLANEOUS STANDARDS	6-28-89	R 5-1-89
18	ROAD STD. SHEET MT-3	MISCELLANEOUS STANDARDS	8-5-88	R 8-1-88
	ROAD STD. SHEET MT	MISCELLANEOUS STANDARDS		
	ROAD STD. SHEET GR1	GUARD RAIL CLASS As		
	ROAD STD. SHEET GR2	GUARD RAIL CLASS Bs, Ds, Es & Hs		
	ROAD STD. SHEET GR4A	GUARD RAIL CLASS Hs		
	ROAD STD. SHEET GR7	GUARD RAIL FHP CONNECTION DETAILS		
	ROAD STD. SHEET GR8	STEEL BEAM GUARD RAIL		
	ROAD STD. SHEET GR10	GUARD RAIL BUFFER ENDS		
	ROAD STD. SHEET GR10A	GUARD RAIL BREAKAWAY CABLE TERMINAL		
	ROAD STD. SHEET GR10B	W-BEAM GUARD RAIL TERMINAL SECTION		
	ROAD STD. SHEET CB-1	CONCRETE MEDIAN BARRIER		
19	ROAD STD. SHEET CB-2	TEMPORARY CONCRETE BARRIER	1-11-89	R 9-1-88
	ROAD STD. SHEET 1 DETOURS	STANDARD DETOUR SIGNS		
20	ROAD STD. SHEET 1A DETOURS	STANDARD DETOUR SIGNS	6-20-91	R 4-1-91
	ROAD STD. SHEET 1B DETOURS	STANDARD DETOUR SIGNS		
	ROAD STD. SHEET 2 DETOURS	STANDARD DETOUR SIGNS		
21	ROAD STD. SHEET 2A DETOURS	STANDARD DETOUR SIGNS	*	A SEPT 1988
22	ROAD STD. SHEET 3 DETOURS	STANDARD DETOUR SIGNS	*	R 9-1-88
23	ROAD STD. SHEET 3A DETOURS	STANDARD DETOUR SIGNS	*	R 9-1-88
24	ROAD STD. SHEET 4 DETOURS	STANDARD DETOUR SIGNS	1-11-89	R. 9-1-88
25	ROAD STD. SHEET 5 DETOURS	STANDARD DETOUR SIGNS	*	R 9-1-88
	ROAD STD. SHEET 5A DETOURS	STANDARD DETOUR SIGNS		

* F.H.W.A. APPROVAL PENDING

PREPARED & RECOMMENDED BY
RQAW
REID, QUEBE, ALLISON, WILCOX & ASSOCIATES, INC.
INDIANAPOLIS, INDIANA
RAMAN D. PATEL P.E.

RAMAN D. PATEL REGISTERED No. 13050 STATE OF INDIANA PROFESSIONAL ENGINEER

RECOMMENDED FOR APPROVAL 10-9-92
BRIDGE REHABILITATION ENGINEER, INDIANA DEPARTMENT OF TRANSPORTATION

JAMES C. KARR REGISTERED No. 16000 STATE OF INDIANA PROFESSIONAL ENGINEER

APPROVED 10-9-92
CHIEF DIVISION OF DESIGN — INDIANA DEPARTMENT OF TRANSPORTATION

REVISIONS	
DATE	SHEET NO.

REVISIONS	
DATE	SHEET NO.
9/9/92	⚠ INDEX, PROJECT NO., INCLUDED DES. NO., ADT YEAR FOR I-65

RECOMMENDED FOR APPROVAL 10-9-92
DESIGN CONSULTANT SERVICES MANAGER
INDIANA DEPARTMENT OF TRANSPORTATION

DAVID M. PLUCKEBAUM REGISTERED No. 20674 STATE OF INDIANA PROFESSIONAL ENGINEER

FEDERAL HIGHWAY ADMINISTRATION
DEPARTMENT OF TRANSPORTATION
APPROVED:
DIVISION ADMINISTRATOR — DATE

INDIANA DEPARTMENT OF HIGHWAYS
STANDARD SPECIFICATIONS DATED 1988
TO BE USED WITH THESE PLANS.
DES. NO. 8716195

BRIDGE FILE: I-65-112-5723A

RQAW FILE: 91013/3311

+1.14% △ -1.62%

-1.62% △ +0.95%


UTILITIES

Power: Indianapolis Power & Light Co.
25 Monument Circle
Indianapolis, In. 46204
317-261-8261


Telephone: Indiana Bell Telephone Co.
240 N. Meridian St.
Indianapolis, In. 46204
800-382-5544

P.V.I. Sta. 14+50.00
Exist. El. 728.76 (1971)
L.V.C. = 200'


P.V.I. Sta. 16+85.00
Exist. El. 724.95 (1971)
L.V.C. = 100'

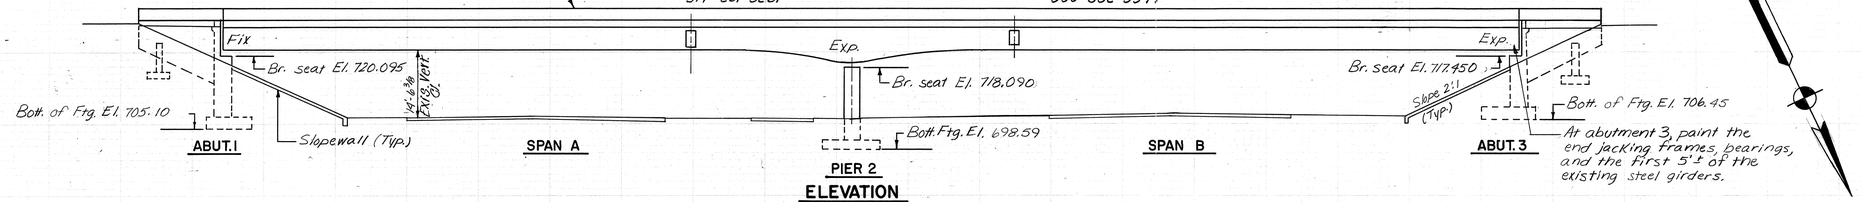

ELEVATION
SCALE 1/16"=1'-0"

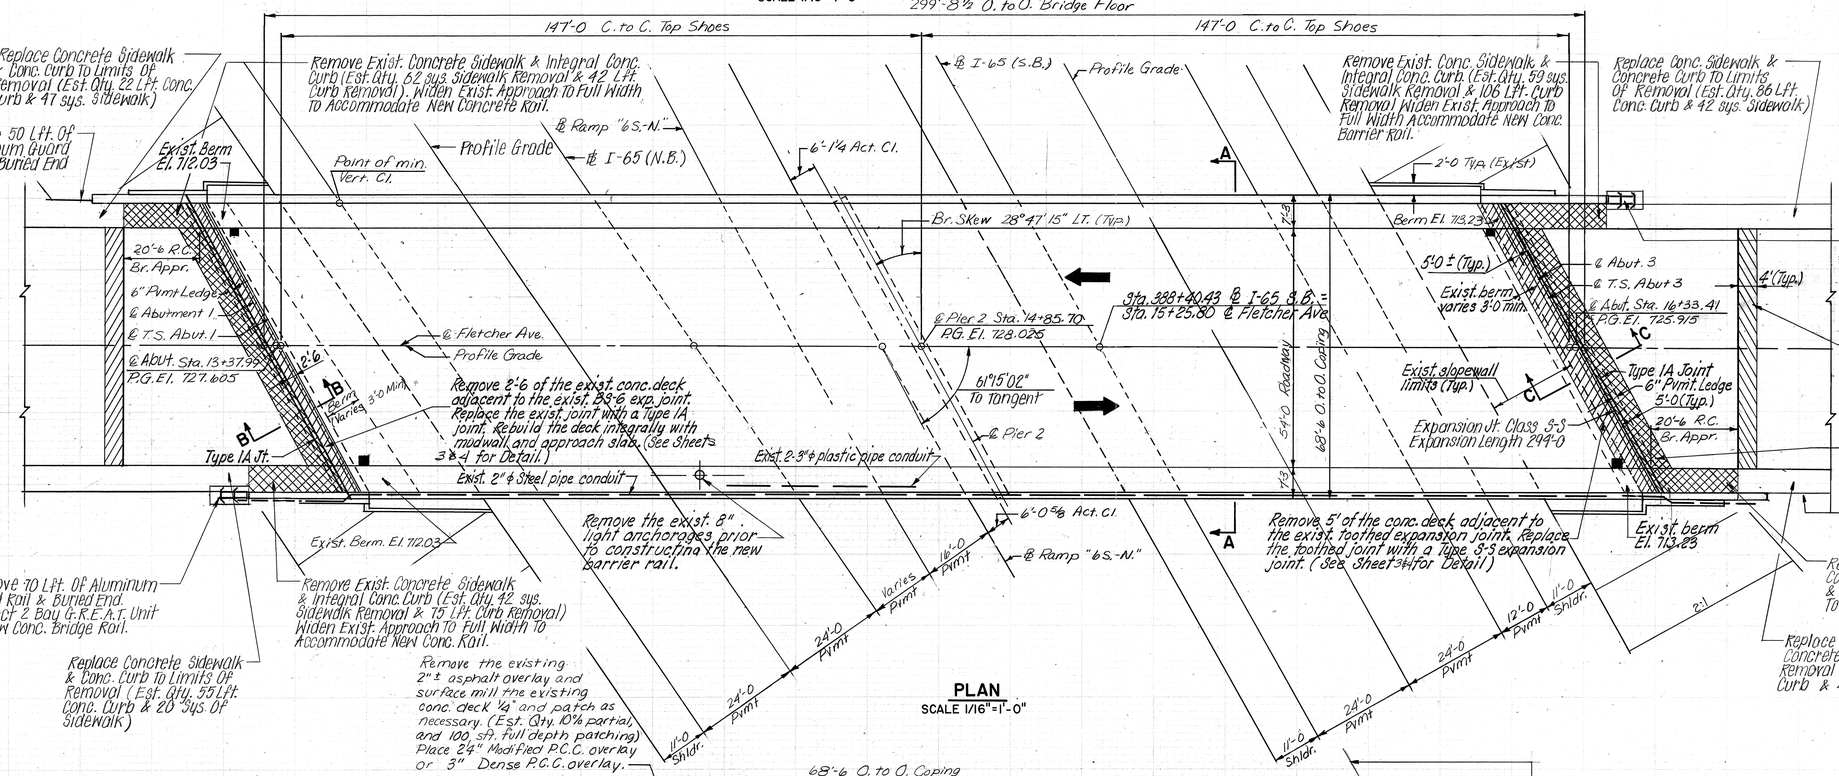

PLAN
SCALE 1/16"=1'-0"

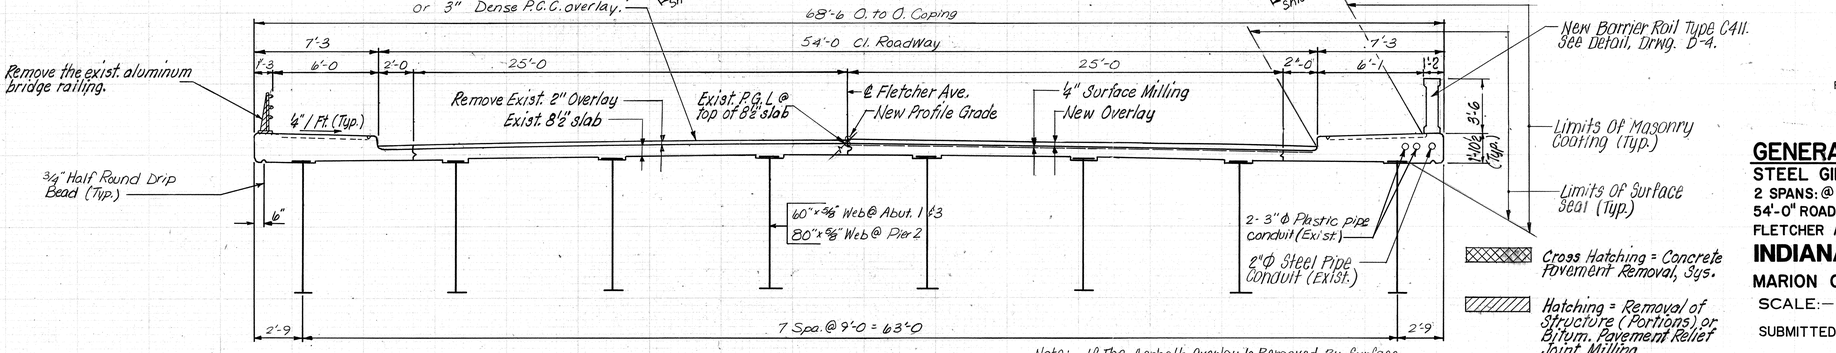

SECTION A-A
SCALE 1/4"=1'-0"

Cross Hatching = Concrete Pavement Removal, Sys.

Hatching = Removal of Structure (Portions) or Bitum. Pavement Relief Joint, Milling

Note: If The Asphalt Overlay Is Removed By Surface Milling, The Removal Of The Asphalt Overlay And The Additional ¼" Concrete Slab Surface Milling Must Be Done As Two Separate Operations.

GENERAL NOTES:

PLANS FOR EXISTING STRUCTURE ARE ON FILE IN THE BRIDGE DEPARTMENT AT THE INDIANA DEPARTMENT OF TRANSPORTATION, AS BRIDGE FILE NO. I-65-112-5723 AND ARE AVAILABLE UPON REQUEST.

WHERE NEW WORK IS TO BE FITTED TO OLD WORK, THE CONTRACTOR SHALL CHECK ALL DIMENSIONS AND CONDITIONS IN THE FIELD AND REPORT ANY ERRORS OR DISCREPANCIES TO THE ENGINEER AND ASSUME RESPONSIBILITY FOR THEIR CORRECTNESS AND THE FIT OF THE NEW PART TO OLD.

CONCRETE FOR PATCHES IN DETERIORATED DECK AREAS SHALL BE BRIDGE DECK PATCHING CONCRETE OR BRIDGE DECK OVERLAY MATERIAL.

THE HAND CHIPPING AND CLEANING OF DETERIORATED DECK AREAS SHALL BE AS DIRECTED BY THE ENGINEER. IT IS THE INTENT OF THESE PLANS THAT ALL SUCH DETERIORATED CONCRETE BE REMOVED, AND SHOULD THERE BE ANY DOUBT AS TO THE QUALITY OF THE CONCRETE, REMOVAL SHALL CONTINUE UNTIL PERFECTLY SOUND CONCRETE IS EXPOSED.

SEAL ALL EXPOSED CONCRETE SURFACES, AS NOTED ON THE PLANS, WITH AN APPROVED SEALER. SEE SUPPLEMENTAL SPECIFICATIONS SECTION 709.05.

CONCRETE IN SUPERSTRUCTURE AND RAILINGS TO BE CLASS "C".

CHAMFER EXPOSED EDGES 1" UNLESS NOTED.

THE BOUNDARIES OF FULL DEPTH REMOVAL AREAS SHALL BE SAW CUT. ALL SAW CUTS FOR REMOVALS SHALL BE MADE TO A MINIMUM DEPTH OF 1" BELOW THE ORIGINAL SURFACE OR TO THE TOP OF THE REINFORCING IF COVER IS LESS THAN 1".

REINFORCING STEEL COVERING SHALL BE 2 1/2" BELOW THE TOP AND 1" ABOVE THE BOTTOM OF THE CLASS "C" CONCRETE SLAB AND 2" IN ALL OTHER PARTS UNLESS NOTED.

ALL BITUMINOUS MATERIAL IN THIS CONTRACT TO BE INCLUDED IN THE PAY ITEM "BITUMINOUS MIXTURE FOR APPROACHES, HV" EXCEPT TACK COAT WHICH SHALL BE PAID FOR AS "BITUMINOUS MATERIAL FOR TACK COAT" IN SQUARE YARDS.

FOR CONCRETE REMOVAL EQUIPMENT, SEE ARTICLE 202.03(B) OF THE STANDARD SPECIFICATIONS.

WHEN DRILLING FOR THE **INSTALLATION OF THE NEW BARRIER RAIL, UTILITY SERVICE** SHALL NOT BE **INTERRUPTED**. IF **UTILITY SERVICE** IS **INTERRUPTED**, THE PROPER UTILITIES SHOULD BE NOTIFIED IMMEDIATELY.

MATERIAL NOTES:

BRIDGE DECK OVERLAY:
2 1/4" MODIFIED PORTLAND CEMENT CONCRETE OVERLAY
OR
3" DENSE PORTLAND CEMENT CONCRETE OVERLAY.
(2" OR 2 3/4" ABOVE THE ORIGINAL SURFACE)

PAVEMENT RELIF JOINT:
330 POUNDS PER SQUARE YARD H. A. C. SURFACE TYPE II, MV.

GENERAL PLAN

STEEL GIRDER BRIDGE
2 SPANS: @ 147'-0" SKEW: 28° 47' 15" LT.
54'-0" ROADWAY; TWO 6'-1" SIDEWALKS
FLETCHER AVE. OVER I-65 & RAMP 6S-N

INDIANA DEPARTMENT OF TRANSPORTATION

MARION COUNTY

SCALE:- **AS NOTED** DATE:- November 7, 1991

SUBMITTED FOR APPROVAL: Richard T. O'Connor

DRAWING:- D-1 OF D-6 SHEET:- 2 OF 25

PROJECT:- NH/65-3(245)111

BRIDGE CONTRACT NO. B-19752

BRIDGE FILE:- I-65-112-5723A


RICHARD T. O'CONNOR REGISTERED No. 17778 STATE OF INDIANA PROFESSIONAL ENGINEER

DESIGNED		C'K'D	
DRAWN	DJS	C'K'D	JET
TRACED		C'K'D	

SF-22317

RQAW FILE: 91013/3311

TP118

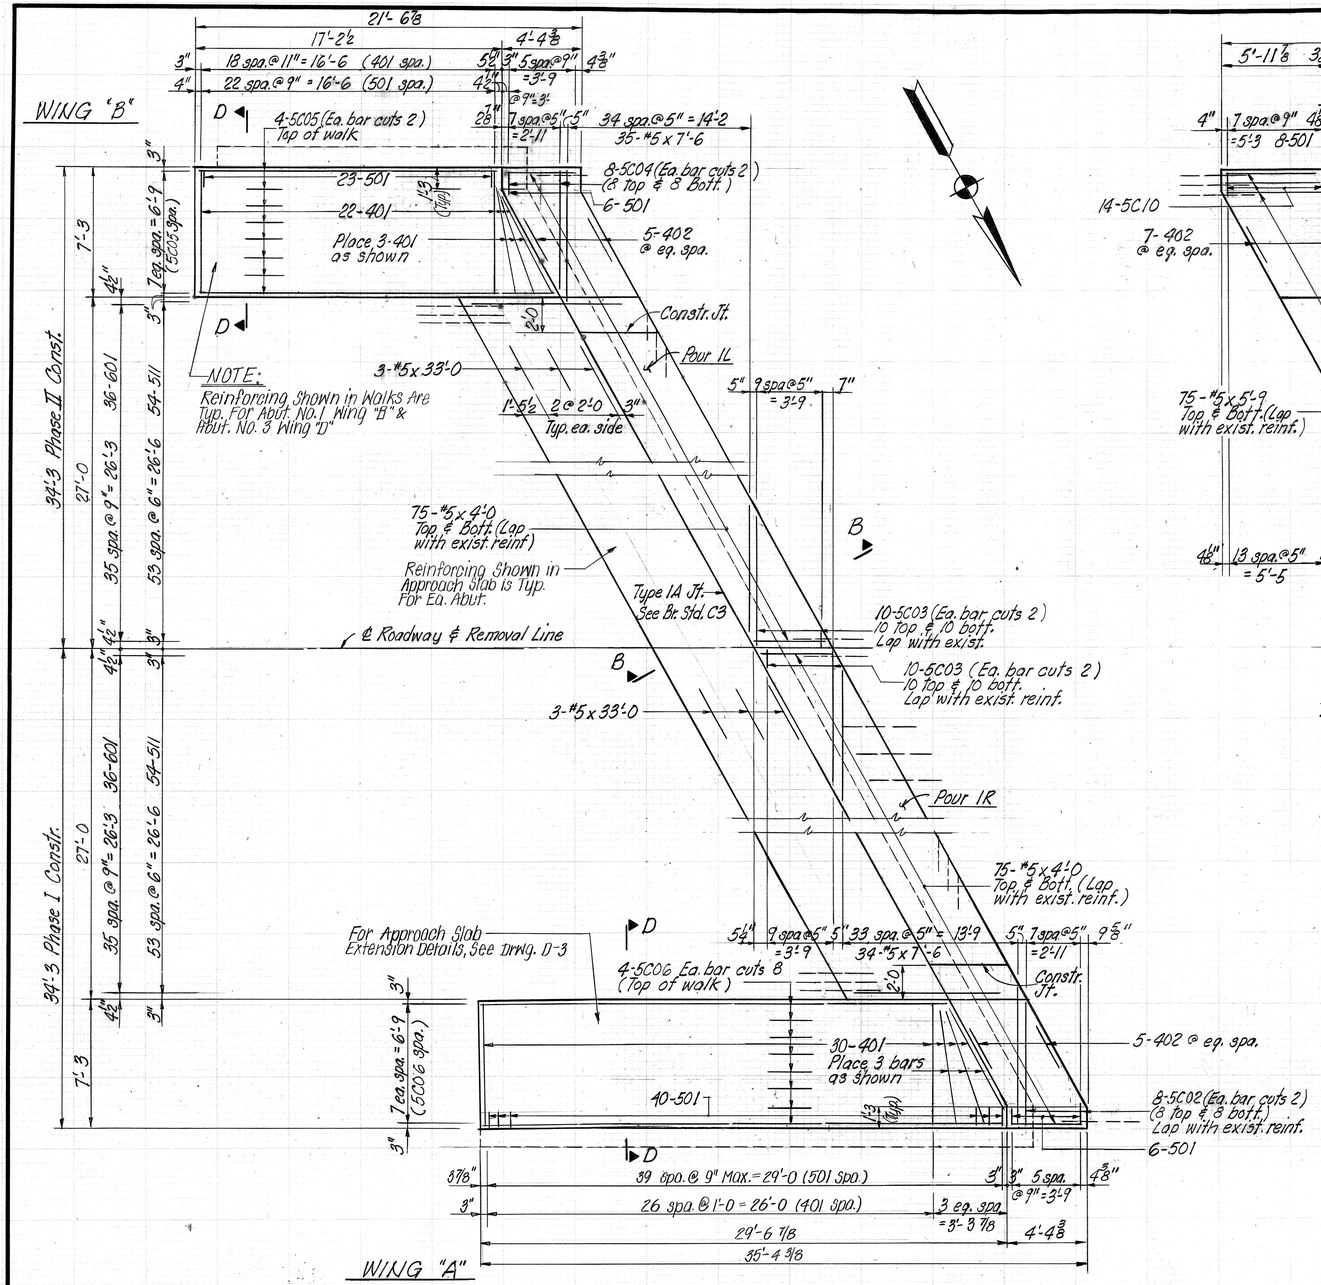

Note:
See Br. Std. C1 for Reinf. Bar Notes.
Exist. reinf. to be cut, cleaned, straightened and extended 2'-0 into new concrete at 5'-0 removal only.
See Br. Std. 33-1 & 2 for Exp. Joint, Class 33.

RECONSTRUCTION DETAILS

INDIANA DEPARTMENT OF TRANSPORTATION


DESIGNED ____ C'K'D ____
DRAWN M.E.B. C'K'D JET
TRACED ____ C'K'D ____
SF-22317

SCALE:— AS NOTED DATE:- November 7, 1991
SUBMITTED FOR APPROVAL: Richard J. O'Connor
DRAWING:- D-2 OF D-6 SHEET:- 3 OF 25
PROJECT:- NH/65-3(245)III STATION:—
BRIDGE CONTRACT NO. B-19752
BRIDGE FILE:- I-65-112-5723A


RICHARD J. O'CONNOR REGISTERED No. 17778 STATE OF INDIANA PROFESSIONAL ENGINEER

RQAW FILE : 91013/3311


TP118

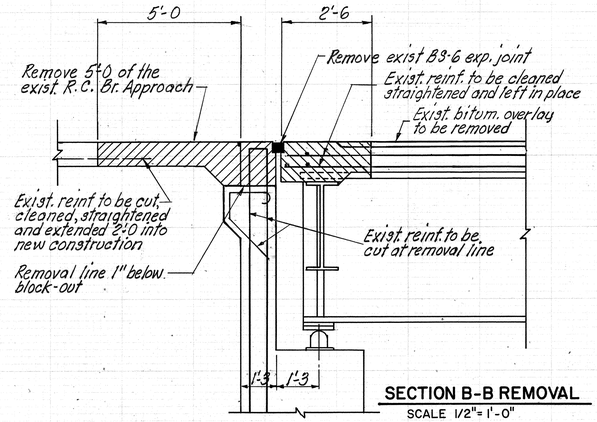


SECTION B-B REMOVAL
SCALE 1/2"= 1'-0"

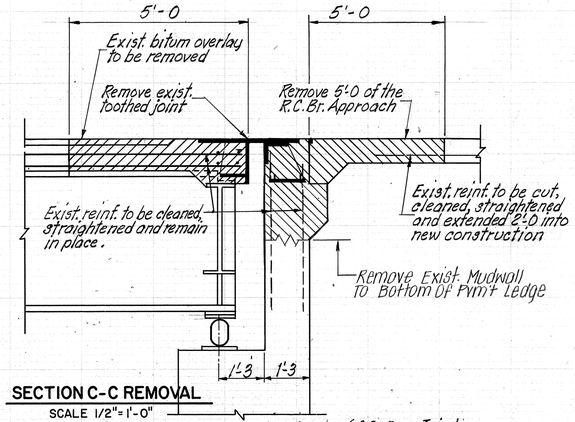

SECTION C-C REMOVAL
SCALE 1/2"= 1'-0"

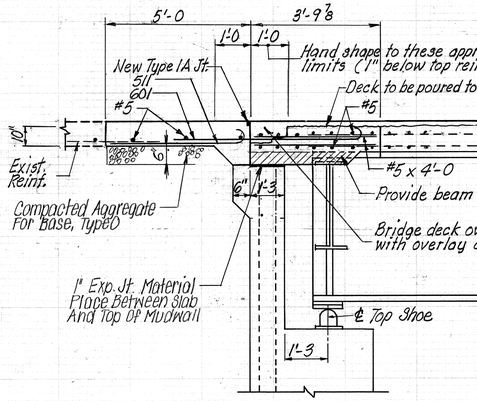

SECTION B-B RECONSTRUCTION
SCALE 1/2"=1'-0"

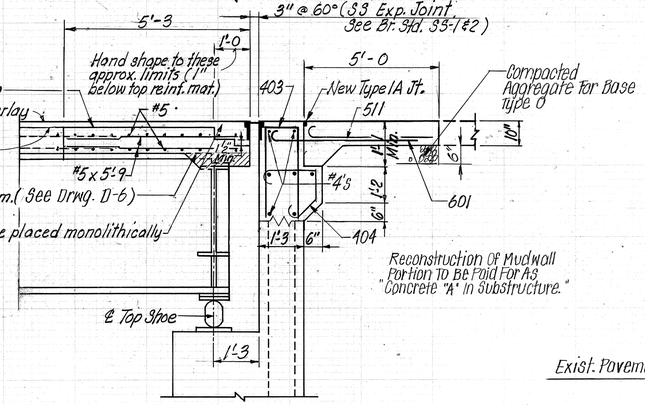


SECTION C-C RECONSTRUCTION
SCALE 1/2"=1'-0"

Reconstruction Of Mudwall Portion To Be Paid For As "Concrete "A" in Substructure."

BILL OF MATERIALS
R.C. APPROACHES

Epoxy Coated Reinforcing Steel			
Size or Mark	No of Bars	Length	Weight (Lbs.)
501	122	5'-8	
582	231	7'-6	
591	4	17'-7	
594	2	24'-1	
595	2	29'-7	
Total Epoxy Coated Reinf.			2,713
Reinforcing Steel			
#6	33	3'-0	
Total #6			149
5C05	8	36'-3	
5C06	4	55'-2	
5C11	4	43'-5	
511	216	5'-11	
591	4	17'-7	
594	2	24'-1	
595	2	29'-7	
5C92	12	38'-3	
5C93	6		
5C94	6	56'-11	
#5	12	33'-0	
Total #5			3,761
401	98	10'-0	
Total #4			655
Total Reinf. Steel			4,565
Miscellaneous			Qty.
Cement, Conc. Pavement, Reinf. 10 IN			139 Sys.
Curb Walk, Integral, Concrete			71 Sys.
Field Drilled Holes in Conc.			33 Ea.

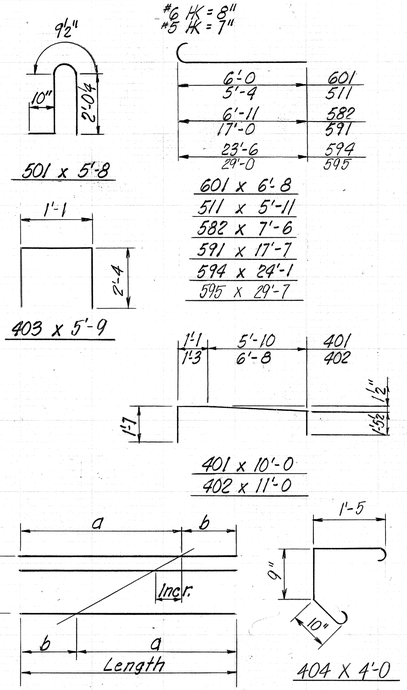

Mark	a	b	N	Incr.	Length
5C02	7'-6	2'-2	8	9⅛"	9'-8
5C03	7'-6	0'-9	20	9⅛"	8'-3
5C04	6'-8	1'-4	8	9⅛	8'-0
5C05	20'-2	16'-4	8	6⅝"	36'-6
5C07	10'-5	2'-1	12	9⅛"	12'-6
5C08	10'-8	0'-9	14	9⅛"	11'-5
5C09	10'-6	0'-7	14	9⅛"	11'-1
5C10	11'-4	1'-6	14	9⅛"	12'-10


HK = 7"

Mark	a	b	N	Incr.	Length
* 5C92	20'-6	17'-9	6	6⅝"	38'-3


* Bars to be hooked on one end

BILL OF MATERIALS


Epoxy Coated Reinforcing Steel			
Size or Mark	No. of Bars	Length	Weight (Lbs.)
601	144	6'-8	1442
501	28	5'-8	
5C02	8	9'-8	
5C03	20	8'-3	
5C04	8	8'-0	
5C05	8	36'-6	
5C06	8	44'-10	
5C07	12	12'-6	
5C08	14	11'-5	
5C09	14	11'-1	
5C10	14	12'-10	
#5	59	10'-6	
#5	69	7'-6	
#5	150	5'-9	
#5	150	4'-0	
	Total #5		4547
402	24	11'-0	
403	72	5'-9	
404	72	4'-0	
#4	16	39'-9	
Total #4			1070
Total Epoxy Coated R.S.			7059
CONCRETE			CYS
Class "A" in Substr.			13.5
Class. "C" in Superstr.			
Pour 1R & 1L (2@ 9.3 cyds. ea)			18.6
Pour 2R & 2L (2@ 8.6 cyds. ea.)			17.2
Total Class "C" Concrete			35.8
Miscellaneous			Qty.
Exp. Joint Class 33			80 Lft.
Surface Seal			6886 Sft.
Masonry Coating			7300 Sft.

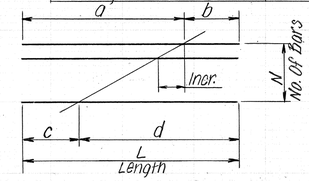


Mark	a	b	c	d	N	Incr.	L
5C06	29'-2	26'-0	27'-4	27'-10	4	5 7/16"	55'-2
5C11	23'-3	20'-2	21'-5	22'-0	4	5 5/16"	43'-5
* 5C93	23'-10	20'-9	22'-2	22'-5	6	3 3/8"	44'-7
* 5C94	29'-9	27'-2	28'-4	28'-7	6	2 13/16	56'-11

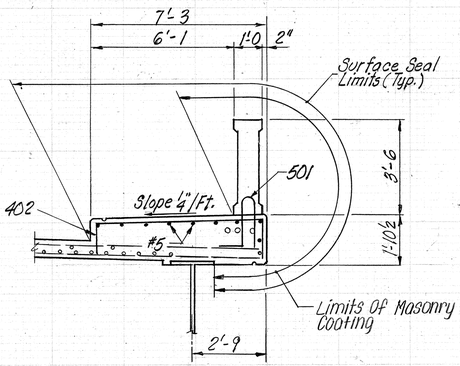


TYPICAL SECTION AT CURB AND WALK ON BRIDGE
Not to scale

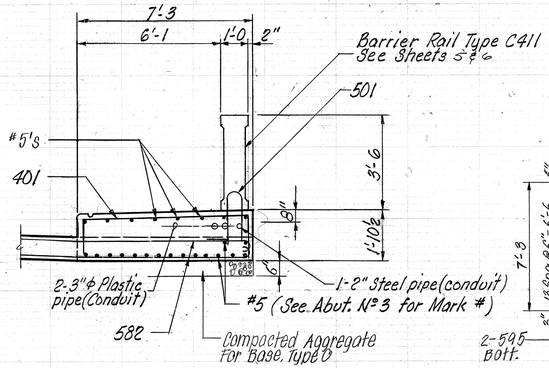

SECTION D-D
Not to scale

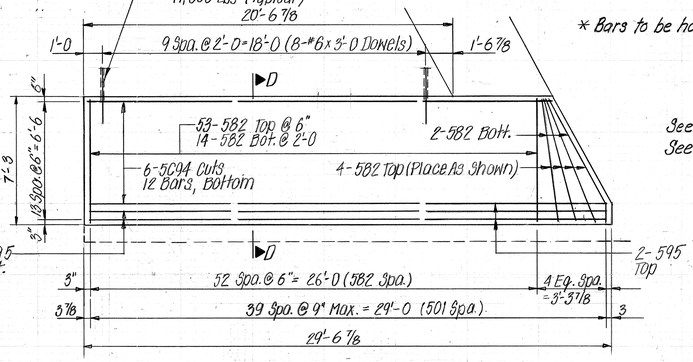

APPROACH SLAB EXTENSION DETAIL - WING "A"
Scale: ¼" = 1'-0

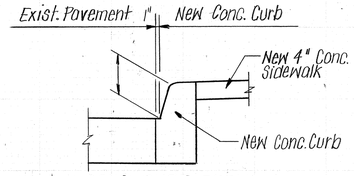

CONC. CURB DETAIL

See Bridge Std. C1 for Reinf. Bar Notes.
See Bridge Std. 33-1 & 33-2 for Exp. Jts. Class 33

REMOVAL AND RECONSTRUCTION DETAILS
INDIANA DEPARTMENT OF TRANSPORTATION

SCALE:- AS NOTED DATE:- November 7, 1991

SUBMITTED FOR APPROVAL: Richard T. O'Connor

DRAWING:- D-3 OF D-6 SHEET:- 4 OF 25

PROJECT: NH/65-3(245)III

BRIDGE CONTRACT NO. B-19752

BRIDGE FILE:- I-65-112-5723A


RICHARD T. O'CONNOR REGISTERED No. 17778 STATE OF INDIANA PROFESSIONAL ENGINEER

DESIGNED ____ C'K'D ____
DRAWN DJS C'K'D JET
TRACED ____ C'K'D ____


SF-22317

RQAW FILE: 91013/3311


TP118

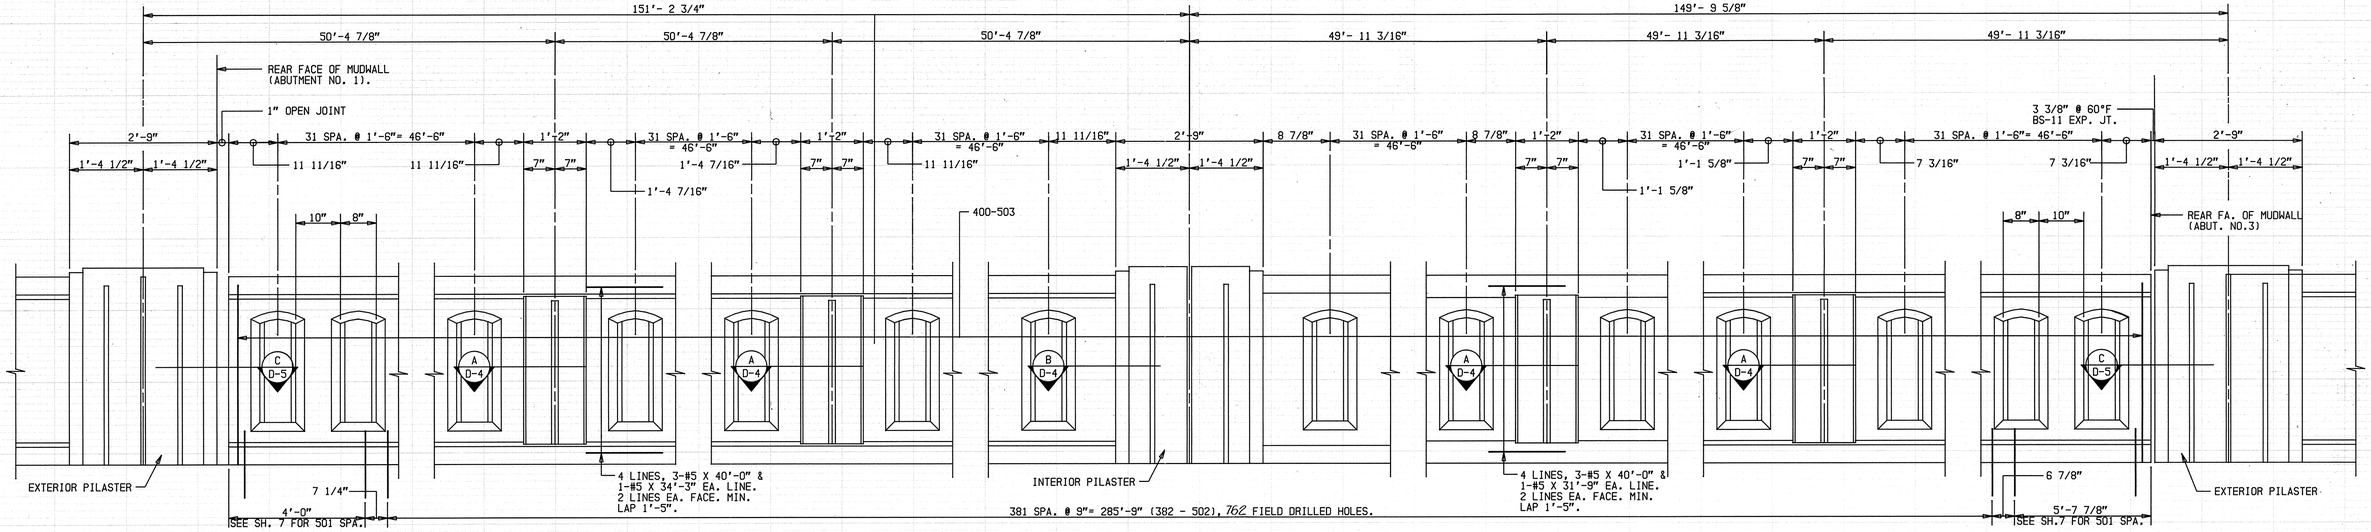


BARRIER RAIL ELEVATION
SCALE: 3/4" = 1'-0"

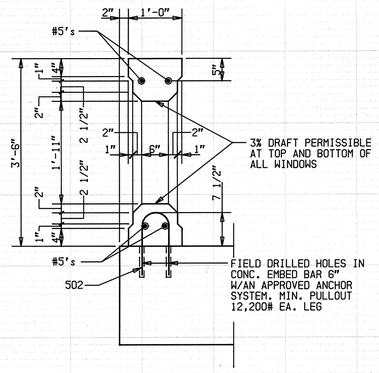


SECTION THRU WINDOW
SCALE: 3/4" = 1'-0"

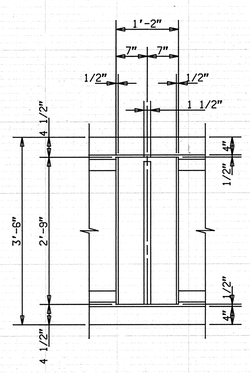


SPAN PILASTER DETAIL
SCALE: 3/4" = 1'-0"

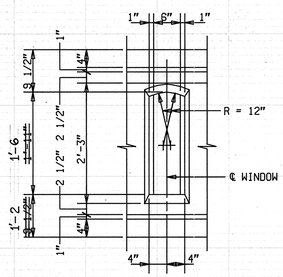


WINDOW DETAIL
SCALE: 3/4" = 1'-0"

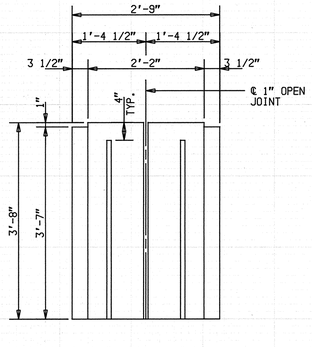


INTERIOR PILASTER DETAIL
SCALE: 3/4" = 1'-0"

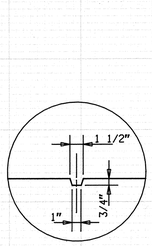


DETAIL "A"
SCALE: 1 1/2" = 1'-0"

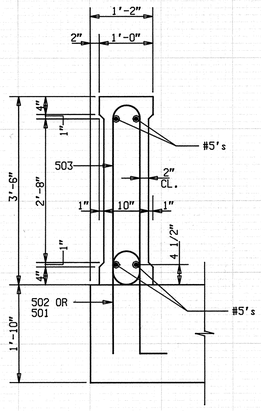

SECTION THRU POST
SCALE: 3/4" = 1'-0"

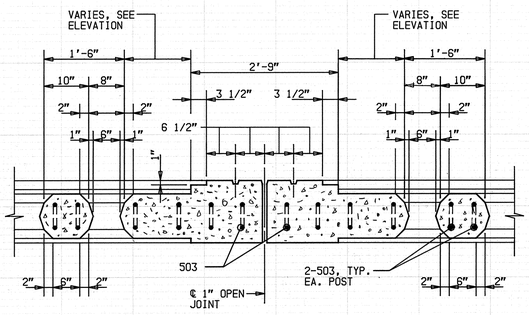

SECTION B D-4
SCALE: 3/4" = 1'-0"

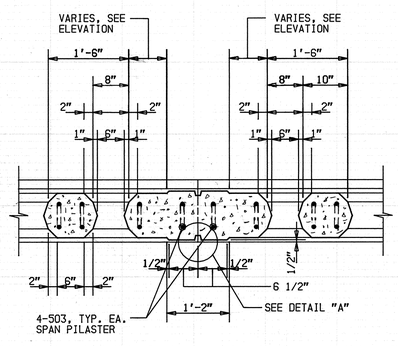

SECTION A D-4
SCALE: 3/4" = 1'-0"

NOTES:
FOR GENERAL NOTES, SEE DRAWING D-1

ALL LAPS SHOWN ARE MINIMUM LAP LENGTHS.

BARRIER RAIL TYPE C411 SHALL BE PAID FOR AS "RAILING, CONCRETE CLASS C" IN LFT.

FOR REINFORCING BAR NOTES, SEE BRIDGE STANDARD C1.

FOR ADDITIONAL DETAILS & BILL OF MATERIALS, SEE DRWG. D-5.

BARRIER RAIL TYPE C411 - DETAILS
INDIANA DEPARTMENT OF TRANSPORTATION

SCALE:— AS NOTED DATE:- November 7, 1991

SUBMITTED FOR APPROVAL: Richard T. O'Connor

DRAWING D-4 OF D-6 SHEET:- 5 OF 25

PROJECT:- NH/65-3(245)III

BRIDGE CONTRACT NO. B-19752

BRIDGE FILE:- I-65-112-5723A


RICHARD T. O'CONNOR REGISTERED No. 17778 STATE OF INDIANA PROFESSIONAL ENGINEER

DESIGNED		C'K'D
DRAWN	GKM	C'K'D
TRACED		C'K'D

SF-22317


RQAW FILE:91013/3311

TP118

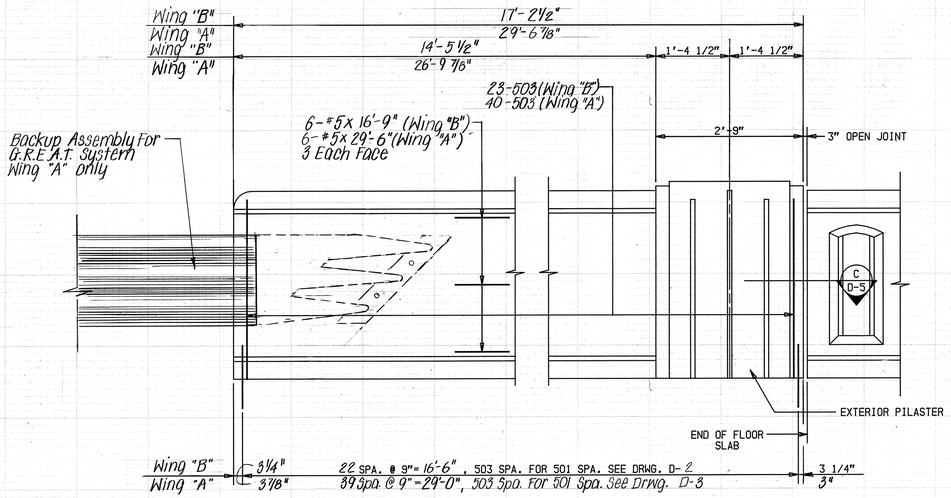


BARRIER RAIL TRANSITION - ABUT. NO.1

SCALE: 3/4" = 1'-0"

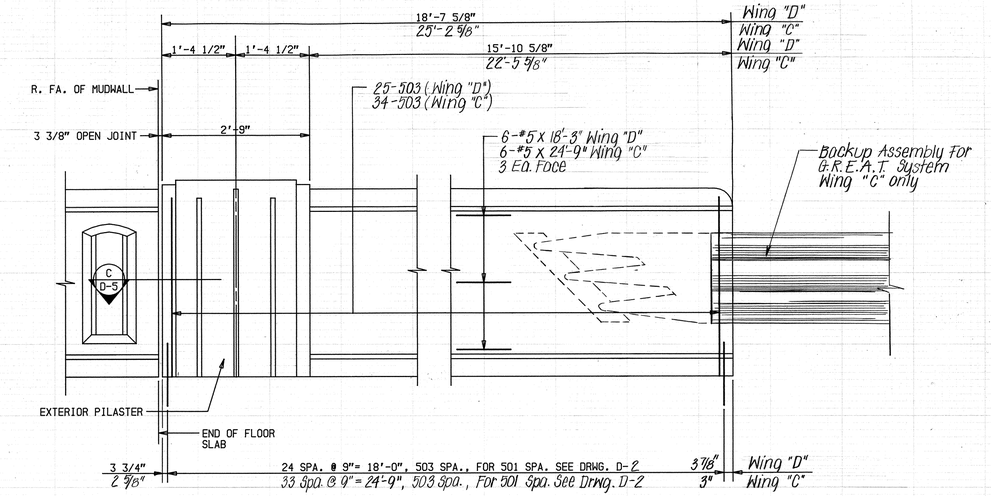


BARRIER RAIL TRANSITION - ABUT. NO.3

SCALE: 3/4" = 1'-0"

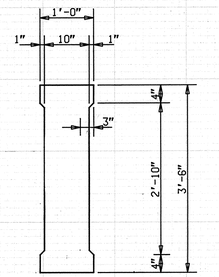


SECTION THRU TRANSITION WALL

SCALE: 3/4" = 1'-0"

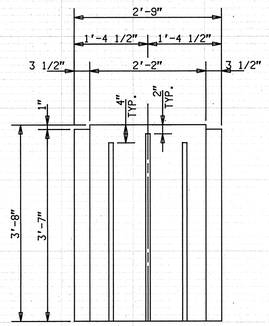


EXTERIOR PILASTER DETAIL


SCALE: 3/4" = 1'-0"

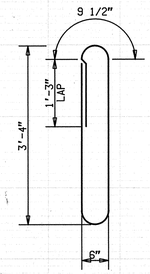

503 X 7'-11"

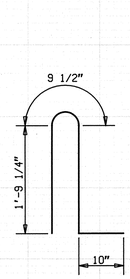


501 X 5'-2"

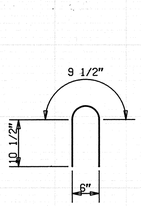

502 X 2'-6"


BILL OF MATERIALS

EPOXY COATED REINFORCING STEEL			
SIZE & MARK	NO. OF BARS	LENGTH	WEIGHT (LBS.)
502	764	2'-6	
503	922	7'-11	
#5	6	29'-6	
#5	6	24'-9	
#5	6	18'-3	
#5	6	16'-9	
#5	48	40'-0	
#5	8	34'-3	
#5	8	31'-9	
TOTAL #5			12,717
MISCELLANEOUS			(QTY.)
RAILING, CONCRETE CLASS "C"			687 LFT.
FIELD DRILLED HOLES			1,524 EACH
SURFACE SEAL (ESTIMATED)			5225 SFT.

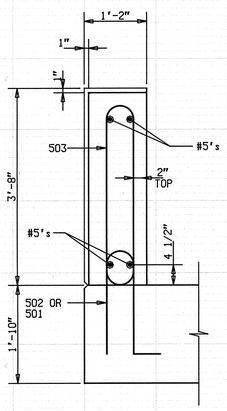

SECTION THRU POST

SCALE: 3/4" = 1'-0"

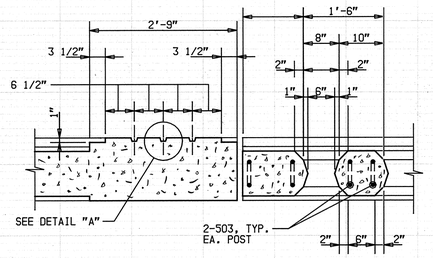

SECTION C D-5

SCALE: 3/4" = 1'-0"

NOTES:

FOR GENERAL NOTES, SEE DRAWING D-1

ALL LAPS SHOWN ARE MINIMUM LAP LENGTHS.

BARRIER RAIL TYPE C411 SHALL BE PAID FOR AS "RAILING, CONCRETE CLASS C" IN LFT.

FOR REINFORCING BAR NOTES, SEE BRIDGE STANDARD C1.

FOR ADDITIONAL DETAILS, SEE DRWG. D-4.

BARRIER RAIL TYPE C411 TRANSITION DETAILS

INDIANA DEPARTMENT OF TRANSPORTATION

SCALE:- AS NOTED DATE:- November 7, 1991

SUBMITTED FOR APPROVAL: Richard T. O'Connor

DESIGNED _____ C'K'D _____

DRAWN GKM C'K'D _____

TRACED _____ C'K'D _____

SF-22317

DRAWING: D-5 OF D-6 SHEET:- 6 OF 25


PROJECT: NH /65-3(245)III

BRIDGE CONTRACT NO. B-19752


BRIDGE FILE:- I-65-112-5723A

RICHARD T. O'CONNOR REGISTERED No. 17778 STATE OF INDIANA PROFESSIONAL ENGINEER


RQAW FILE: 91013/3311

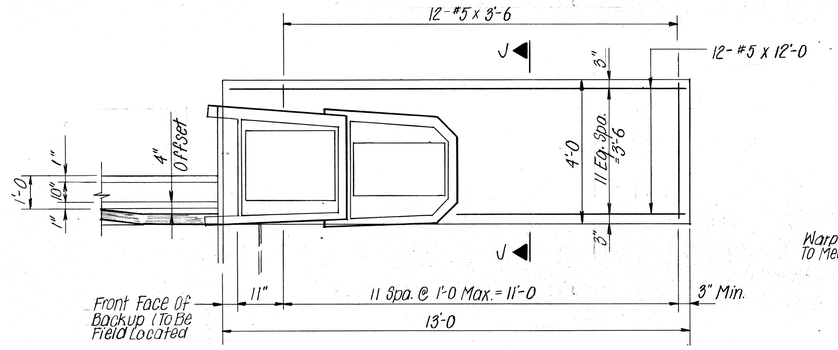


PLAN
No Scale

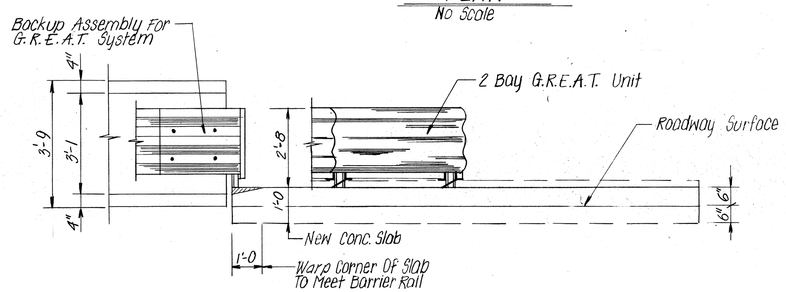

ELEVATION
No Scale

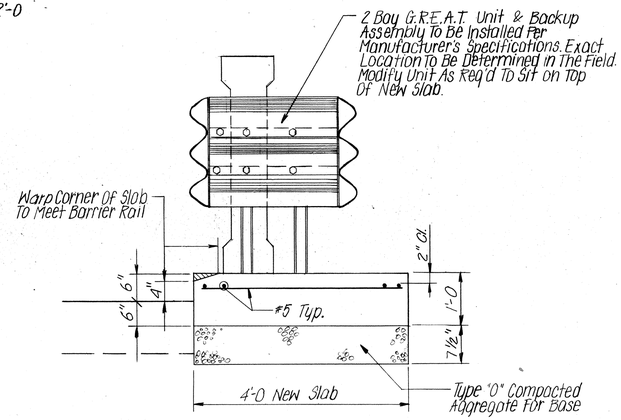


SECTION J-J
No Scale

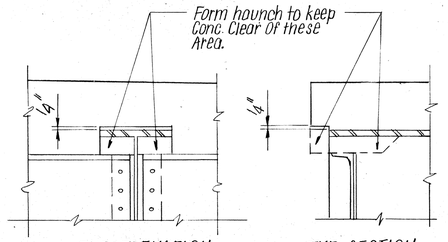


END ELEVATION

TYP. SECTION

BEAM BLOCKOUT AT HAUNCH
Not To Scale

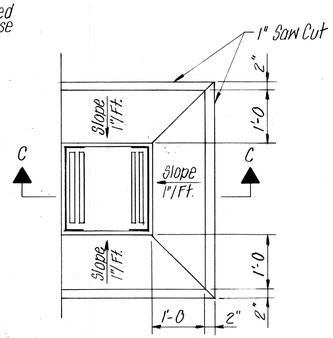


PLAN

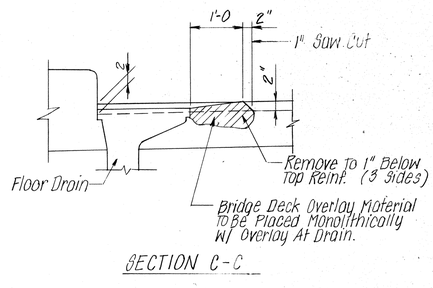

SECTION C-C

BRIDGE FLOOR DRAIN DETAIL
No Scale

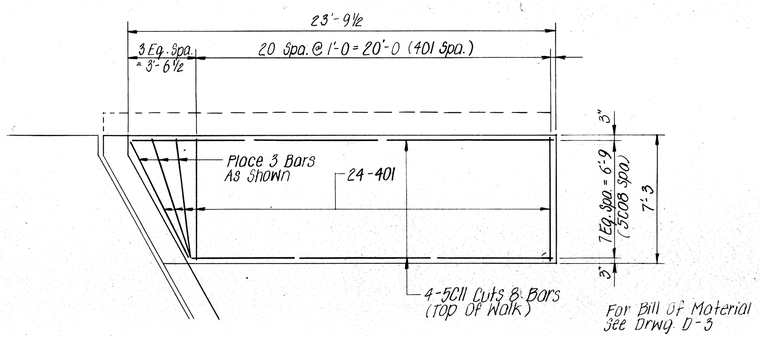

WING "C" - SIDEWALK REINF. DETAILS
Scale: ¼" = 1'-0

* BILL OF MATERIALS

Epoxy Coated Reinforcing Steel			
Size & Mark	No. Of Bars	Length	Weight (Lbs.)
#5	12	12'-0	
#5	12	3'-6	
Total			194
Miscellaneous			Qty
Concrete, A			1.9 cys.
Compacted Aggregate for Base, D			2.4 ton

* For One G.R.E.A.T. Unit Only

MISCELLANEOUS	(QTY.)
Bridge Deck Patching, Partial	
Depth	1552 SFt.
Surface Milling, Portland	
Cement. concrete	1724 Sys.
Bridge Deck Patching, Full	
Depth	100 SFt.
Bridge Deck Overlay (Additional)	15 cys.
Bridge Deck Overlay	1793 Sys.
Guard Rail, Remove	332.5 LFt.
Bridge Deck Overlay, Remove	1724 Sys.
Pavement, Remove	68 Sys.
Sidewalk, Concrete, Remove	219 Sys.
Curb, Concrete, Integral, Remove	323 LFt.
Sidewalk, Concrete	150 Sys.
Curb, Concrete	243 LFt.
Compacted Aggregate For	
Base, O, Size 53	51.1 Tons
G.R.E.A.T. Unit, 2 Bay	2 Each

NOTES:
For General Notes, See Drwg. D-1.
See Br. Std. C1, For Reinf. Bar Notes.

G.R.E.A.T. UNIT & RECONSTRUCTION DETAILS

INDIANA DEPARTMENT OF TRANSPORTATION

SCALE:- AS NOTED DATE:- November 7, 1991

SUBMITTED FOR APPROVAL: Richard T. O'Connor

DRAWING:- D-6 OF D-6 SHEET:- 7 OF 25

PROJECT:- NH/65-3(245)111

BRIDGE CONTRACT NO. B-19752

BRIDGE FILE:- I-65-112-5723A

RICHARD T. O'CONNOR REGISTERED No. 17778 STATE OF INDIANA PROFESSIONAL ENGINEER

DESIGNED		C'K'D
DRAWN	GKM	C'K'D
TRACED		C'K'D

SF-22317

91013/3311

TP118

CONTRACT NO. B-19752

BRIDGES OVER 20' SPAN

FEDERAL REGION NO.	STATE	PROJECT NO.	FISCAL YEAR	SHEET NO.	TOTAL SHEETS
5	IND	EACNHI-65-3 (245)III	1992	1	15

INDEX

PROJECT	STRUCTURE	TYPE	SPAN	OVER	STATION
EACNHI-65-3(245)III	I-65-111-5719A I-65-111-5720A I-65-112-5721A I-65-112-5722A I-65-112-5723A	N/A - SEE REHAB. PLANS	SEE REHAB. PLANS	N/A - SEE REHAB. PLANS	SEE REHAB. PLANS

SHEET NO.	SHEET DESIGNATION	SUBJECT	F.H.W.A. APPROVAL
1	ONE SHEET	TITLE SHEET & INDEX	
2	ONE SHEET	TRAFFIC MAINTENANCE TRAFFIC FLOW	
3-6	FOUR SHEETS	TRAFFIC MAINTENANCE	
7-9	THREE SHEETS	PAVEMENT MARKINGS	

B-19752 8-8

TRAFFIC DATA	SEE REHAB. PLANS	SEE REHAB. PLANS
A.D.T. (19)	V.P.D	V.P.D
A.D.T. (19 PROJECTED)	V.P.D	V.P.D
D.H.V. (19 PROJECTED)	V.P.D	V.P.D
TRUCKS	D.H.V. % A.D.T. %	D.H.V. % A.D.T. %
POSTED SPEED	M.P.H.	M.P.H.
ACCESS CONTROL		
FUNCTIONAL CLASSIFICATION	URBAN ARTERIAL	INTERSTATE

PREPARED & RECOMMENDED BY

RQAW

REID, QUEBE, ALLISON, WILCOX & ASSOCIATES, INC.
INDIANAPOLIS, INDIANA

RAMAN D. PATEL P.E.

RAMAN D. PATEL REGISTERED No. 13050 STATE OF INDIANA PROFESSIONAL ENGINEER


INDIANA DEPARTMENT OF TRANSPORTATION

BRIDGE PLANS

FOR SPANS OVER 20 FEET

PROJECT EACNHI-65-3(245)III
TRAFFIC MAINTENANCE

TRAFFIC MAINTENANCE PLANS FOR STRUCTURES: I-65-111-5719A, I-65-111-5720A, I-65-112-5721A, I-65-112-5722A, & I-65-112-5723A, ALL LOCATED IN R-3-E, T-15-N, IN MARION COUNTY, INDIANA.

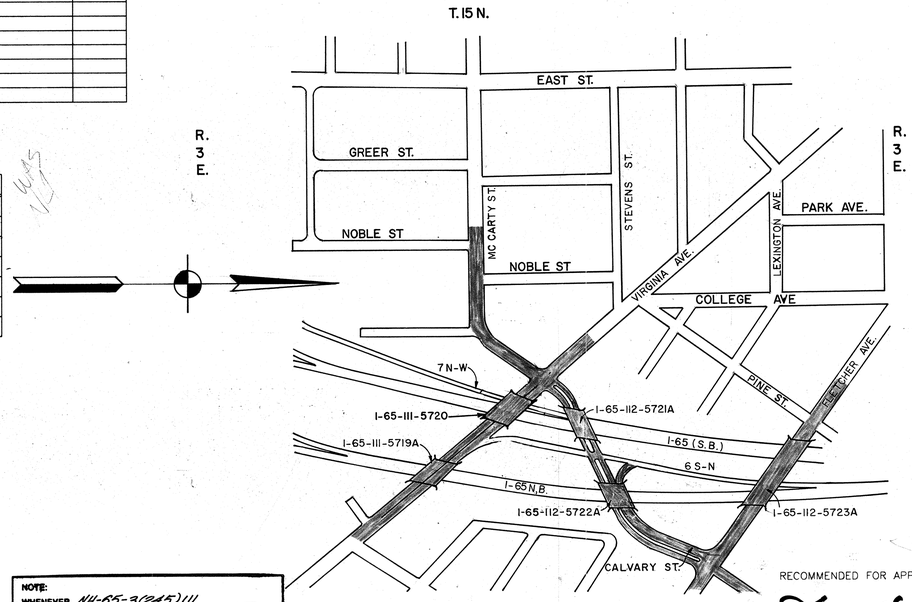

NOTE:
WHENEVER N11-65-3(245)111
APPEARS ON THESE PLANS OR CONTRACT DOCUMENTS
IT SHALL BE INTERPRETED AS EACNHI-65-3(245)III

INDEX CONTINUED
STANDARD DRAWINGS

SHEET NO.	SHEET DESIGNATION	SUBJECT	F.H.W.A. APPROVAL	ADOPTED "A" REVISION "R"
	BRIDGE STD. BR5	BRIDGE RAILING CONNECTION DETAILS		
	BRIDGE STD. C1	MISCELLANEOUS DETAILS		
	BRIDGE STD. C2	MISCELLANEOUS DETAILS		
	BRIDGE STD. C3	MISCELLANEOUS DETAILS		
	BRIDGE STD. C4	PRESTRESSED CONCRETE PILES		
	BRIDGE STD. C5	PRECAST DECK PANEL DETAILS		
	BRIDGE STD. D	CASTING DETAILS AND ROADWAY DRAINS		
	BRIDGE STD. D1	ADJUSTING FRAME DETAILS FOR ROADWAY DRAINS		
	BRIDGE STD. PB1	PRESTRESSED CONCRETE TYPE I I-BEAMS		
	BRIDGE STD. PB2	PRESTRESSED CONCRETE TYPE II I-BEAMS		
	BRIDGE STD. PB3	PRESTRESSED CONCRETE TYPE III I-BEAMS		
	BRIDGE STD. PB	PRESTRESSED CONCRETE TYPE I-BEAMS		
	BRIDGE STD. PB10	TOLERANCES FOR FABRICATION OF PRESTRESSED BEAMS		
	BRIDGE STD. PB11	ELASTOMERIC BEARING PADS FOR CONCRETE BEAMS		
	BRIDGE STD. R2A	BRIDGE LIGHTING DETAILS		
	BRIDGE STD. R2B	BRIDGE LIGHTING DETAILS		
	BRIDGE STD. S1	MISCELLANEOUS DETAILS		
	BRIDGE STD. SH1	STEEL SHOE DETAILS		
	BRIDGE STD.			
	BRIDGE STD.			
	BRIDGE STD. T SHEET A	STANDARD TEMPORARY BRIDGE		
	BRIDGE STD. T SHEET B	STANDARD TEMPORARY BRIDGE		
	ROAD STD. SHEET A	STANDARD PAVEMENT JOINTS		
	ROAD STD. SHEET B	STANDARD PAVEMENT JOINTS		
	ROAD STD. SHEET MA	MISCELLANEOUS STANDARDS		
	ROAD STD. SHEET MB	MISCELLANEOUS STANDARDS		
	ROAD STD. SHEET MB-2	MISCELLANEOUS STANDARDS		
	ROAD STD. SHEET MB-4	MISCELLANEOUS STANDARDS		
	ROAD STD. SHEET MC	MISCELLANEOUS STANDARDS		
	ROAD STD. SHEET MC-1	MISCELLANEOUS STANDARDS		
	ROAD STD. SHEET	MISCELLANEOUS STANDARDS		
	ROAD STD. SHEET MD	MISCELLANEOUS STANDARDS		
	ROAD STD. SHEET MD	MISCELLANEOUS STANDARDS		
	ROAD STD. SHEET MD	MISCELLANEOUS STANDARDS		
	ROAD STD. SHEET ME	MISCELLANEOUS STANDARDS		
	ROAD STD. SHEET ME	MISCELLANEOUS STANDARDS		
	ROAD STD. SHEET ME	MISCELLANEOUS STANDARDS		
	ROAD STD. SHEET	MISCELLANEOUS STANDARDS		
	ROAD STD. SHEET MH	MISCELLANEOUS STANDARDS		
	ROAD STD. SHEET MH-1	MISCELLANEOUS STANDARDS		
	ROAD STD. SHEET MH-2	MISCELLANEOUS STANDARDS		
	ROAD STD. SHEET MI	MISCELLANEOUS STANDARDS		
	ROAD STD. SHEET MI-1	MISCELLANEOUS STANDARDS		
	ROAD STD. SHEET MI-2	MISCELLANEOUS STANDARDS		
	ROAD STD. SHEET	MISCELLANEOUS STANDARDS		
	ROAD STD. SHEET MI	MISCELLANEOUS STANDARDS		
	ROAD STD. SHEET	MISCELLANEOUS STANDARDS		
	ROAD STD. SHEET MN	MISCELLANEOUS STANDARDS		
	ROAD STD. SHEET MN-1	MISCELLANEOUS STANDARDS		
	ROAD STD. SHEET MP	MISCELLANEOUS STANDARDS		
	ROAD STD. SHEET MQ	MISCELLANEOUS STANDARDS		
	ROAD STD. SHEET MR	MISCELLANEOUS STANDARDS		
	ROAD STD. SHEET MT	MISCELLANEOUS STANDARDS		
	ROAD STD. SHEET MT	MISCELLANEOUS STANDARDS		
	ROAD STD. SHEET GR1	GUARD RAIL CLASS 4S		
	ROAD STD. SHEET GR2	GUARD RAIL CLASS 3S, 3X, 2S & HS		
	ROAD STD. SHEET GR4A	GUARD RAIL CLASS 1S		
	ROAD STD. SHEET GR7	GUARD RAIL FIER CONNECTION DETAILS		
	ROAD STD. SHEET GR8	STEEL BEAM GUARD RAIL		
	ROAD STD. SHEET GR10	GUARD RAIL BUFFER ENDS		
	ROAD STD. SHEET GR10A	GUARD RAIL BREAKAWAY CABLE TERMINAL		
	ROAD STD. SHEET GR10B	W-BEAM GUARD RAIL TERMINAL SECTION		
	ROAD STD. SHEET CB-1	CONCRETE MEDIAN BARRIER		
	ROAD STD. SHEET CB-2	TEMPORARY CONCRETE BARRIER		
	ROAD STD. SHEET 1 DETOURS	STANDARD DETOUR SIGNS		
10	ROAD STD. SHEET 1A DETOURS	STANDARD DETOUR SIGNS	6-20-91	R 4-1-91
	ROAD STD. SHEET 1B DETOURS	STANDARD DETOUR SIGNS		
	ROAD STD. SHEET 2 DETOURS	STANDARD DETOUR SIGNS		
11	ROAD STD. SHEET 2A DETOURS	STANDARD DETOUR SIGNS	*	A SEPT 88
12	ROAD STD. SHEET 3 DETOURS	STANDARD DETOUR SIGNS	*	R 9-1-88
13	ROAD STD. SHEET 3A DETOURS	STANDARD DETOUR SIGNS	*	R 9-1-88
14	ROAD STD. SHEET 4 DETOURS	STANDARD DETOUR SIGNS	1-11-89	R 9-1-88
15	ROAD STD. SHEET 5 DETOURS	STANDARD DETOUR SIGNS	*	R 9-1-88
	ROAD STD. SHEET 5A DETOURS	STANDARD DETOUR SIGNS		

* F.H.W.A. APPROVAL PENDING

RECOMMENDED FOR APPROVAL 10-26-92
BRIDGE REHABILITATION ENGINEER, INDIANA DEPARTMENT OF TRANSPORTATION

JAMES C. KARR REGISTERED No. 16000 STATE OF INDIANA PROFESSIONAL ENGINEER

APPROVED 10-26-92
CHIEF, DIVISION OF DESIGN, BUREAU OF DEPARTMENT OF TRANSPORTATION

RECOMMENDED FOR APPROVAL 10-26-92
DESIGN CONSULTANT SERVICES MANAGER
INDIANA DEPARTMENT OF TRANSPORTATION

DAVID M. PLUCKEBAUM REGISTERED No. 20674 STATE OF INDIANA PROFESSIONAL ENGINEER

FEDERAL HIGHWAY ADMINISTRATION
DEPARTMENT OF TRANSPORTATION
APPROVED:
DIVISION ADMINISTRATOR DATE


REVISIONS	
DATE	SHEET NO.
11/20/92	Shts. 1 through 6

REVISIONS	
DATE	SHEET NO.


INDIANA DEPARTMENT OF HIGHWAYS
STANDARD SPECIFICATIONS DATED 1988
TO BE USED WITH THESE PLANS.

BRIDGE FILE: I-65-111-5719/I-65-111-5720/I-65-112-5721 I-65-112-5722/I-65-112-5723

RQAW FILE: 91013/3307-3308-3309-3310

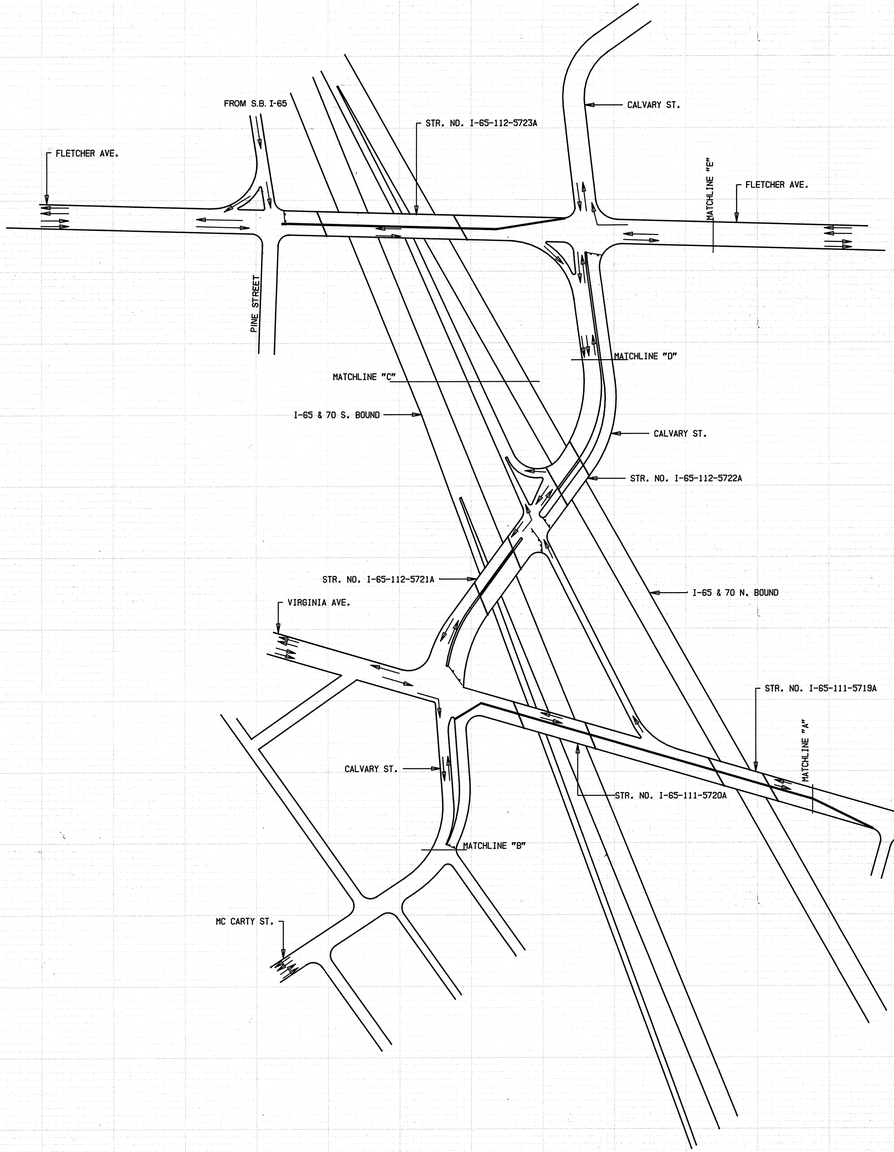

PHASE I CONSTRUCTION TRAFFIC FLOW

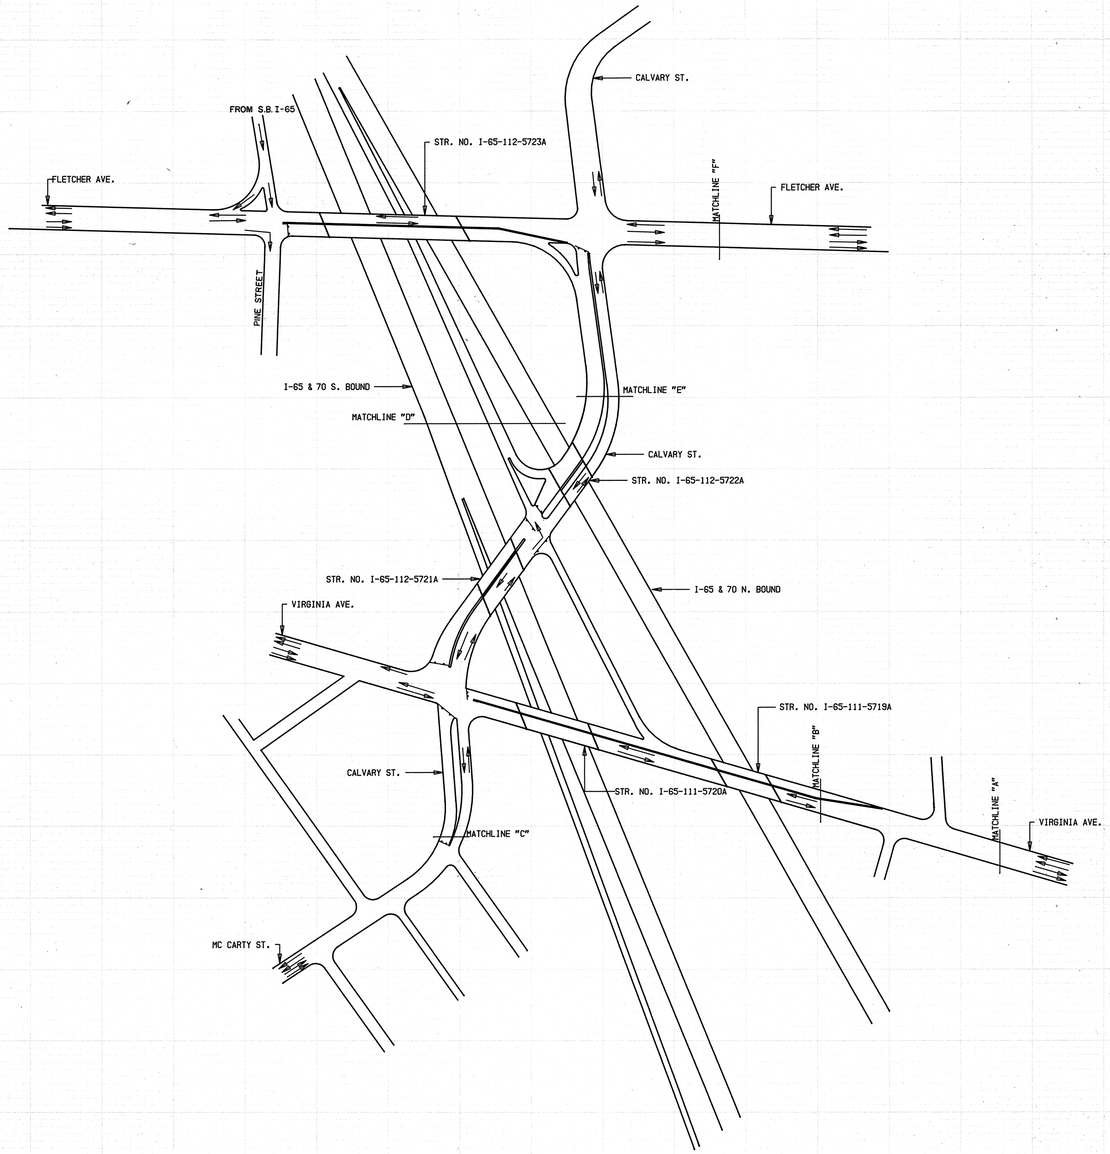

PHASE II CONSTRUCTION TRAFFIC FLOW

NOTE: TRUCK TRAFFIC WILL BE DETOURED AS ADVISED BY THE DISTRICT.

ALL TRAFFIC SIGNAL PHASING (PERMANENT AND TEMPORARY) SHALL BE COORDINATED WITH THE INDIANAPOLIS DEPARTMENT OF TRANSPORTATION AND I.N.D.O.T.

TRAFFIC MAINTENANCE

INDIANA DEPARTMENT OF TRANSPORTATION

SCALE:- AS NOTED DATE:- November 7, 1991

SUBMITTED FOR APPROVAL: Richard T. O'Connor

DRAWING:- OF SHEET:- 2 OF 15

PROJECT:- NH/65-3(245)111

BRIDGE CONTRACT NO. B-19752

BRIDGE FILE:- I-65-111-5719A THRU I-65-112-5723A

RICHARD T. O'CONNOR REGISTERED No. 17778 STATE OF INDIANA PROFESSIONAL ENGINEER

DESIGNED	JET	C'K'D	
DRAWN	DJS	C'K'D	JET
TRACED		C'K'D	

SF-22317

91013/3307, 3308, 3309, 3310

REV. 11/20/92 ADDED STREET NAMES

TP118

SIGN LEGEND

1. END CONSTRUCTION SIGN, (X6-20-2).
2. XW1-2-B(R).
3. CONSTRUCTION SIGN ASSEMBLY: (XW1-3-B)(L,R) SPEED SIGN (XW-13-1-A).
4. DETOUR ROUTE ASSEMBLY: DO NOT PASS SIGN (R4-1-B)(XW-6-3-B).
5. DETOUR ROUTE ASSEMBLY: ROAD CLOSED SIGN (R11-2) DETOUR SIGN (XM4-10)(L,R).
6. RIGHT LANE EXIT ONLY SIGN (XW-105-1-A).
1. TYPE III-A BARRICADE WITH (R11-2) & DETOUR SIGN (XM4-10)(L,R).
7. TEMPORARY STOP SIGN (R-1-1A).

NOTES:

FOR GENERAL NOTES, SEE DRWG. D-2


FOR CONSTRUCTION SIGN DETAILS, SEE ROAD STANDARDS 1,1A, & 2.

LANE CLOSURE NOTICE SIGNS (XG-20-5) SHOULD BE PLACED AS DIRECTED BY THE ENGINEER. (SEE SPECIAL PROVISIONS).

SIGNAL HEADS SHALL BE REALIGNED AS DIRECTED BY THE ENGINEER. COST SHALL BE INCLUDED IN THE COST OF MAINTAINING TRAFFIC.

RAMP 6-S.-N. WILL BE CLOSED DURING PHASE II CONSTRUCTION AND ALL TRAFFIC DETOURED TO CALVARY ST.

THE COST OF ALL TEMPORARY "STOP" SIGNS AND "RIGHT LANE MUST TURN" SIGNS SHALL BE INCLUDED IN "MAINTAINING TRAFFIC".

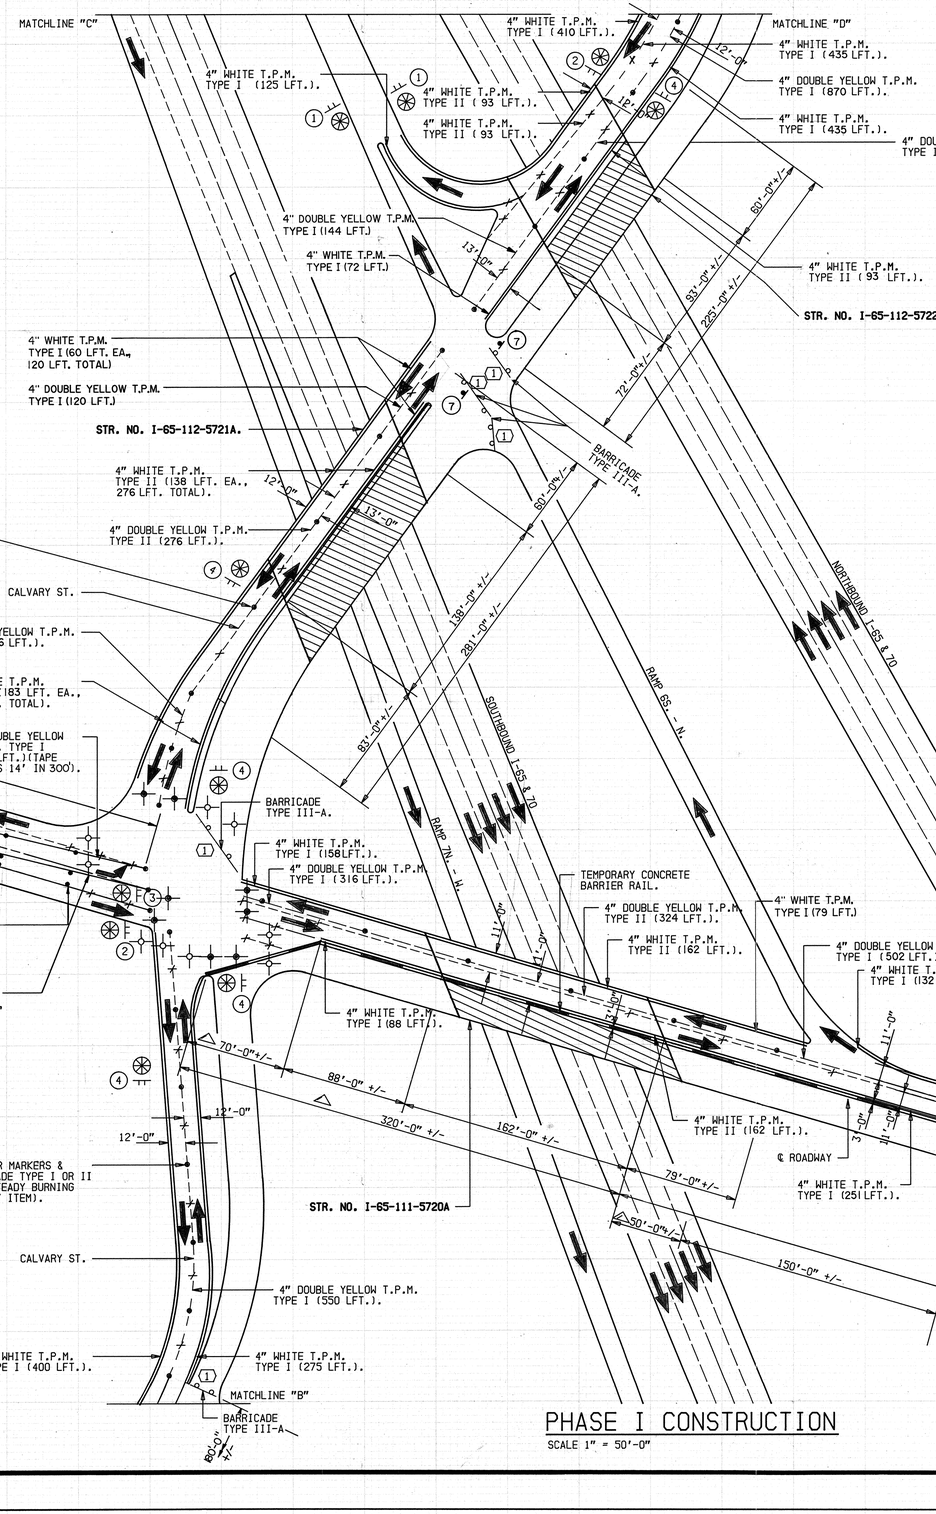

LEGEND

- TEMPORARY CONCRETE BARRIER.
- CONSTRUCTION AREA.
- T.P.M. TEMPORARY PAVEMENT MARKINGS.
- EXISTING PAVEMENT MARKING REMOVAL.
- ANCHORED BARRIER RAIL LIMITS.
- INDICATES DIRECTION OF TRAFFIC FLOW.
- INDICATES LOW INTENSITY FLASHING YELLOW LIGHT, TYPE "A".
- EXISTING SIGNAL HEADS.
- TEMPORARY SIGNAL HEADS.

PHASE I CONSTRUCTION

SCALE 1" = 50'-0"

ALL TRAFFIC SIGNAL PHASING (PERMANENT AND TEMPORARY) SHALL BE COORDINATED WITH THE INDIANAPOLIS DEPARTMENT OF TRANSPORTATION AND I.N.D.O.T.

TRAFFIC MAINTENANCE PHASE I CONSTRUCTION

INDIANA DEPARTMENT OF TRANSPORTATION

SCALE:- AS NOTED DATE:- November 7, 1991

SUBMITTED FOR APPROVAL: Richard J. O'Connor

DRAWING:- OF SHEET:- 3 OF 15

PROJECT:- NH/65-3(245)111

BRIDGE CONTRACT NO. B-19752

BRIDGE FILE:- I-65-111-5719A THRU I-65-112-5722A

RICHARD T. O'CONNOR REGISTERED No. 17778 STATE OF INDIANA PROFESSIONAL ENGINEER

DESIGNED JET C'K'D
DRAWN DJS C'K'D JET
TRACED C'K'D

DRD 6:PM - 9:PM 3 Hours 11-7-91

91013/3307,3308,3309,3310

REV. 11/20/92 LENGTHENED TAPERS ON TRAFFIC MAINT.

TP118

SIGN LEGEND

(1) END CONSTRUCTION SIGN. (X6-20-2).

(2) XW1-2-B(R).

(3) CONSTRUCTION SIGN ASSEMBLY: (XW1-3-B)(L,R) SPEED SIGN (XW-13-1-A).

(4) DETOUR ROUTE ASSEMBLY: DO NOT PASS SIGN (R4-1-B)(XW-6-3-B).

(5) DETOUR ROUTE ASSEMBLY: ROAD CLOSED SIGN (R11-2) DETOUR SIGN (XM4-10)(L,R).

(6) RIGHT LANE EXIT ONLY SIGN (XW105-1-A).

(1) TYPE III-A BARRICADE WITH (R11-2) & DETOUR SIGN (XM4-10)(L,R).

(9) LEFT LANE MUST TURN (R3-7L)- TEMPORARY

NOTES:

FOR GENERAL NOTES, SEE DRW. D-2

FOR CONSTRUCTION SIGN DETAILS, SEE ROAD STANDARDS 1,1A, & 2.


LANE CLOSURE NOTICE SIGNS (XG-20-5) SHOULD BE PLACED AS DIRECTED BY THE ENGINEER. (SEE SPECIAL PROVISIONS).

SIGNAL HEADS SHALL BE REALIGNED AS DIRECTED BY THE ENGINEER. COST SHALL BE INCLUDED IN THE COST OF MAINTAINING TRAFFIC.

RAMP 6-S.-N. WILL BE CLOSED DURING PHASE II CONSTRUCTION AND ALL TRAFFIC DETOURED TO CALVARY ST.

LEGEND

- TEMPORARY CONCRETE BARRIER.
- CONSTRUCTION AREA.
- T.P.M. TEMPORARAY PAVEMENT MARKING.
- EXISTING PAVEMENT MARKING REMOVAL.
- ANCHORED BARRIER RAIL LIMITS.
- INDICATES DIRECTION OF TRAFFIC FLOW.
- INDICATES LOW INTENSITY FLASHING YELLOW LIGHT, TYPE "A".
- EXISTING SIGNAL HEADS.
- TEMPORARY SIGNAL HEADS.

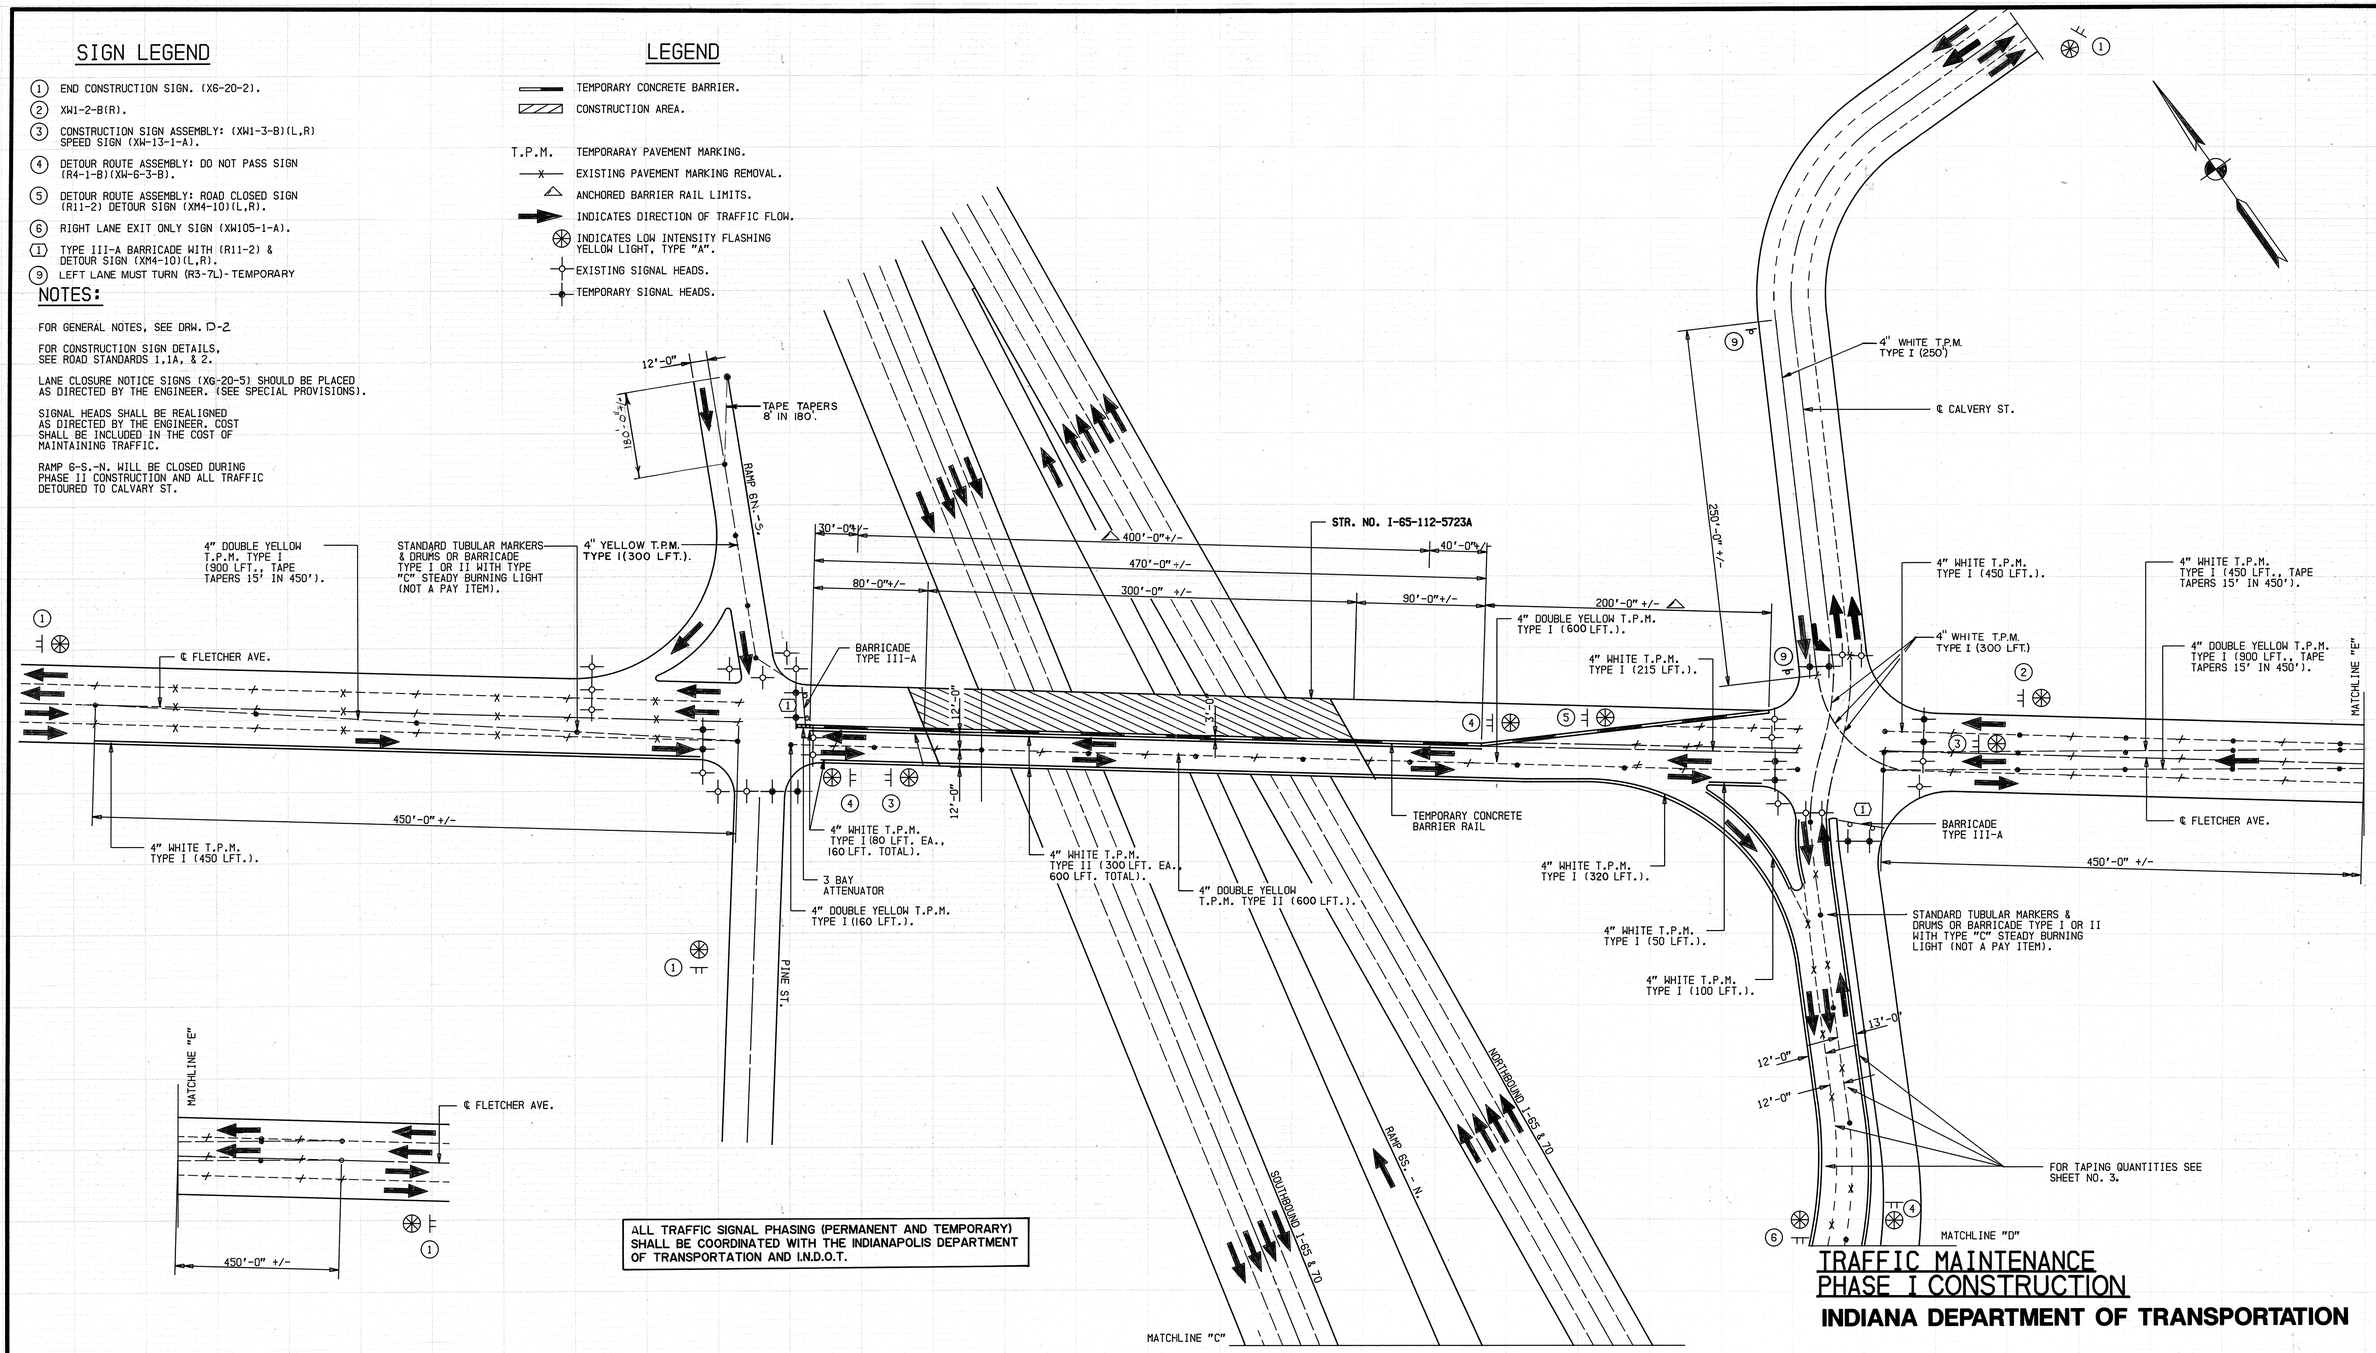

ALL TRAFFIC SIGNAL PHASING (PERMANENT AND TEMPORARY) SHALL BE COORDINATED WITH THE INDIANAPOLIS DEPARTMENT OF TRANSPORTATION AND I.N.D.O.T.

PHASE I CONSTRUCTION

SCALE 1" = 50'-0"

TRAFFIC MAINTENANCE PHASE I CONSTRUCTION

INDIANA DEPARTMENT OF TRANSPORTATION

SCALE:- AS NOTED DATE:- November 7, 1991

SUBMITTED FOR APPROVAL: Richard T. O'Connor

DRAWING:- OF SHEET:- 4 OF 15

PROJECT:- NH/65-3(245)III

BRIDGE CONTRACT NO. B-19752

BRIDGE FILE:-I-65-112-5723A

RICHARD T. O'CONNOR REGISTERED No. 17778 STATE OF INDIANA PROFESSIONAL ENGINEER

DESIGNED JET C'K'D

DRAWN DJS C'K'D JET

TRACED C'K'D

SF-22317

11-7-91 9:PM - 9:25 PM . 92 hours SRS

91013/3311

TP118

REV. 11/20/92 ADDED TURN LINES

SIGN LEGEND

(1) END CONSTRUCTION SIGN, (X6-20-2).

(2) XW1-2-B(R).

(3) CONSTRUCTION SIGN ASSEMBLY: (XW1-3-B)(L,R) SPEED SIGN (XW-13-1-A).

(4) DETOUR ROUTE ASSEMBLY: DO NOT PASS SIGN (R4-1-B)(XW-6-3-B).

(5) DETOUR ROUTE ASSEMBLY: ROAD CLOSED SIGN (R11-2) DETOUR SIGN (XM4-10)(L,R).

(6) RIGHT LANE EXIT ONLY SIGN (XW-105-1-A).

(1) TYPE III-A BARRICADE WITH (R11-2) & DETOUR SIGN (XM4-10)(L,R).

(8) RIGHT LANE MUST TURN (R3-7 R)-TEMPORARY

NOTES:

FOR GENERAL NOTES, SEE DRWG. D-2

FOR CONSTRUCTION SIGN DETAILS, SEE ROAD STANDARDS 1, 1A, & 2.


LANE CLOSURE NOTICE SIGNS (XG-20-5) SHOULD BE PLACED AS DIRECTED BY THE ENGINEER. (SEE SPECIAL PROVISIONS).

SIGNAL HEADS SHALL BE REALIGNED AS DIRECTED BY THE ENGINEER. COST SHALL BE INCLUDED IN THE COST OF MAINTAINING TRAFFIC.

RAMP 6-S.-N. WILL BE CLOSED DURING PHASE II CONSTRUCTION AND ALL TRAFFIC DETOURED TO CALVARY ST.

THE COST OF ALL TEMPORARY "STOP SIGNS" AND "RIGHT LANE MUST TURN" SIGNS SHALL BE INCLUDED IN "MAINTAINING TRAFFIC".

ALL TRAFFIC SIGNAL PHASING (PERMANENT AND TEMPORARY) SHALL BE COORDINATED WITH THE INDIANAPOLIS DEPARTMENT OF TRANSPORTATION AND I.N.D.O.T.

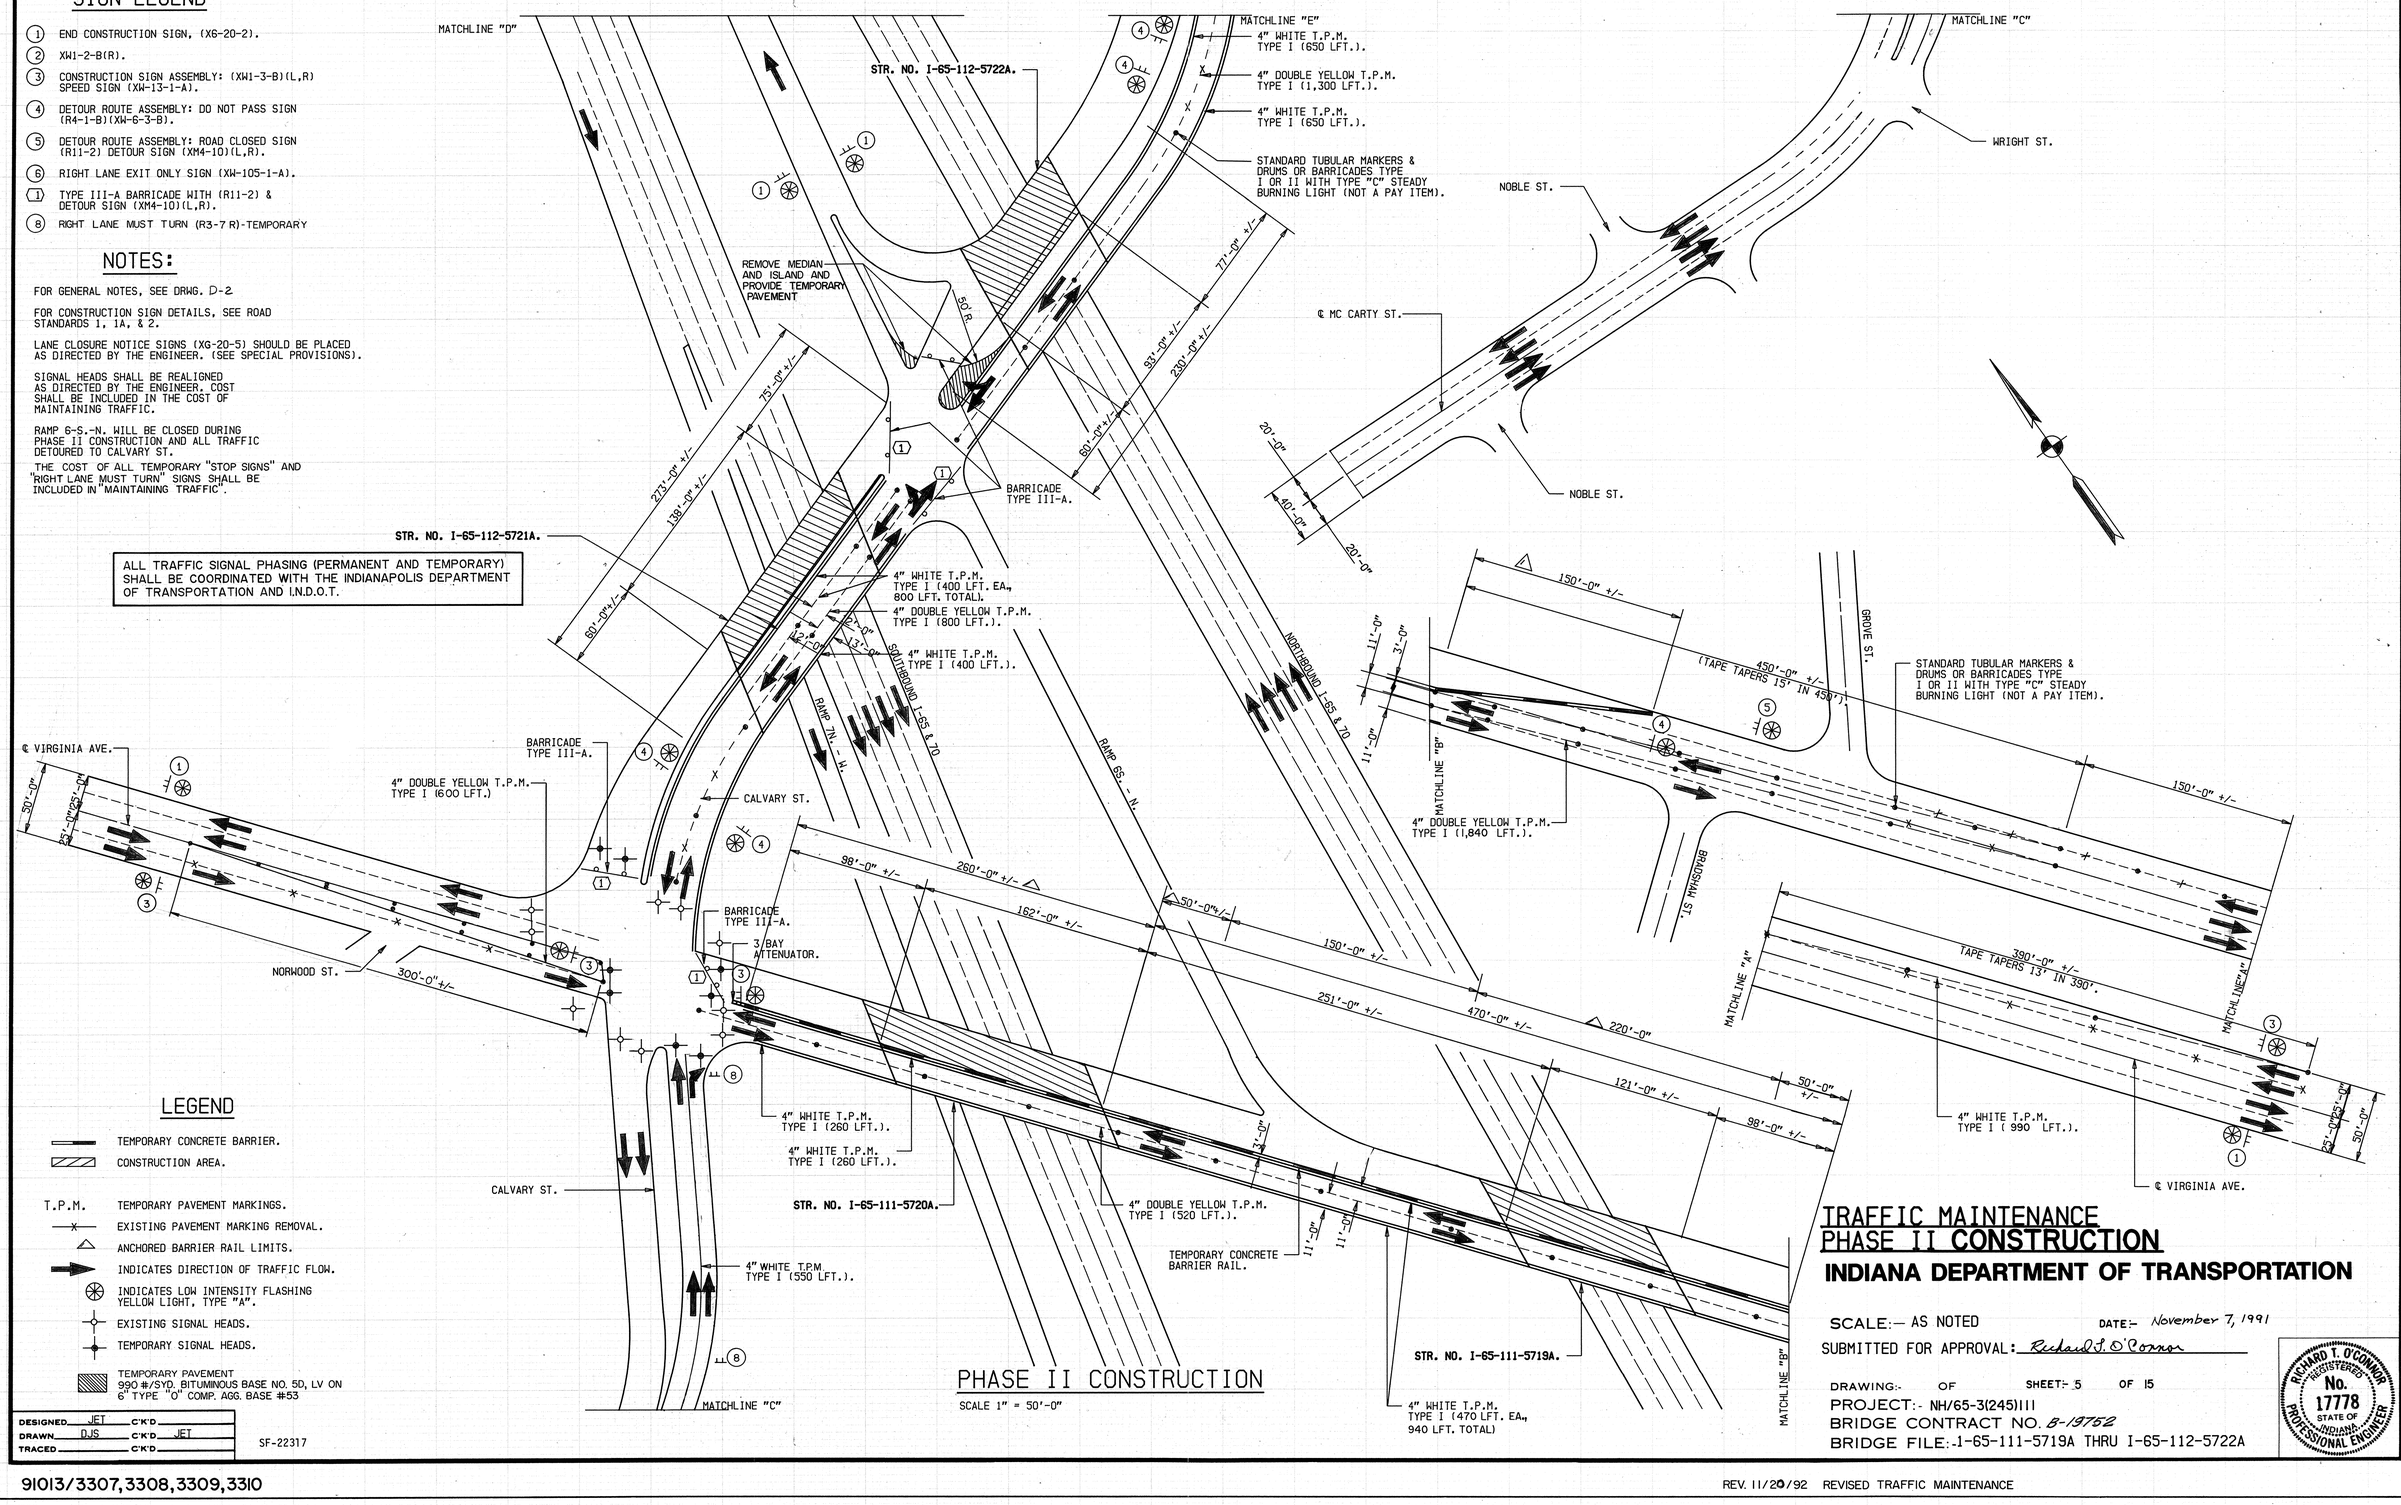

LEGEND

- TEMPORARY CONCRETE BARRIER.
- CONSTRUCTION AREA.
- T.P.M. TEMPORARY PAVEMENT MARKINGS.
- EXISTING PAVEMENT MARKING REMOVAL.
- ANCHORED BARRIER RAIL LIMITS.
- INDICATES DIRECTION OF TRAFFIC FLOW.
- INDICATES LOW INTENSITY FLASHING YELLOW LIGHT, TYPE "A".
- EXISTING SIGNAL HEADS.
- TEMPORARY SIGNAL HEADS.
- TEMPORARY PAVEMENT 990 #/SYD. BITUMINOUS BASE NO. 5D, LV ON 6" TYPE "O" COMP. AGG. BASE #53

PHASE II CONSTRUCTION

SCALE 1" = 50'-0"

TRAFFIC MAINTENANCE PHASE II CONSTRUCTION

INDIANA DEPARTMENT OF TRANSPORTATION

SCALE:- AS NOTED DATE:- November 7, 1991

SUBMITTED FOR APPROVAL: Richard T. O'Connor

DRAWING:- OF SHEET:- 5 OF 15

PROJECT:- NH/65-3(245)III

BRIDGE CONTRACT NO. B-19752

BRIDGE FILE:- I-65-111-5719A THRU I-65-112-5722A

RICHARD T. O'CONNOR REGISTERED No. 17778 STATE OF INDIANA PROFESSIONAL ENGINEER

DESIGNED	JET	C'K'D	
DRAWN	DJS	C'K'D	JET
TRACED		C'K'D	

SF-22317

9:25 pm - 10:50 PM 11-7-91 QRJ 1083 Hours

91013/3307,3308,3309,3310

REV. 11/20/92 REVISED TRAFFIC MAINTENANCE

TP118

SIGN LEGEND

1. END CONSTRUCTION SIGN, (XG-20-2).
2. XW1-2-B(R).
3. CONSTRUCTION SIGN ASSEMBLY: (XW1-3-B)(L,R) SPEED SIGN (XW-13-1-A).
4. DETOUR ROUTE ASSEMBLY: DO NOT PASS SIGN (R4-1-B)(XW-6-3-B).
5. DETOUR ROUTE ASSEMBLY: ROAD CLOSED SIGN (R11-2) DETOUR SIGN (XM4-10)(L,R).
6. RIGHT LANE EXIT ONLY SIGN (XW-105-1-A).
7. TYPE III-A BARRICADE WITH (R11-2) & DETOUR SIGN (XM4-10)(L,R).
8. RIGHT LANE MUST TURN (R3-7R) - TEMPORARY

NOTES:

FOR GENERAL NOTES, SEE DRWG. D-2

FOR CONSTRUCTION SIGN DETAILS, SEE ROAD STANDARDS 1, 1A, & 2.

LANE CLOSURE NOTICE SIGNS (XG-20-5) SHOULD BE PLACED AS DIRECTED BY THE ENGINEER. (SEE SPECIAL PROVISIONS).


SIGNAL HEADS SHALL BE REALIGNED AS DIRECTED BY THE ENGINEER. COST SHALL BE INCLUDED IN THE COST OF MAINTAINING TRAFFIC.

RAMP 6-S.-N. WILL BE CLOSED DURING PHASE II CONSTRUCTION AND ALL TRAFFIC DETOURED TO CALVARY ST.

THE COST OF ALL TEMPORARY "STOP" SIGNS AND "RIGHT LANE MUST TURN" SIGNS SHALL BE INCLUDED IN "MAINTAINING TRAFFIC".

LEGEND

- TEMPORARY CONCRETE BARRIER.
- CONSTRUCTION AREA.
- T.P.M. TEMPORARY PAVEMENT MARKINGS.
- EXISTING PAVEMENT MARKING REMOVAL.
- ANCHORED BARRIER RAIL LIMITS.
- INDICATES DIRECTION OF TRAFFIC FLOW.
- INDICATES LOW INTENSITY FLASHING YELLOW LIGHT, TYPE "A".
- EXISTING SIGNAL HEADS.
- TEMPORARY SIGNAL HEADS.

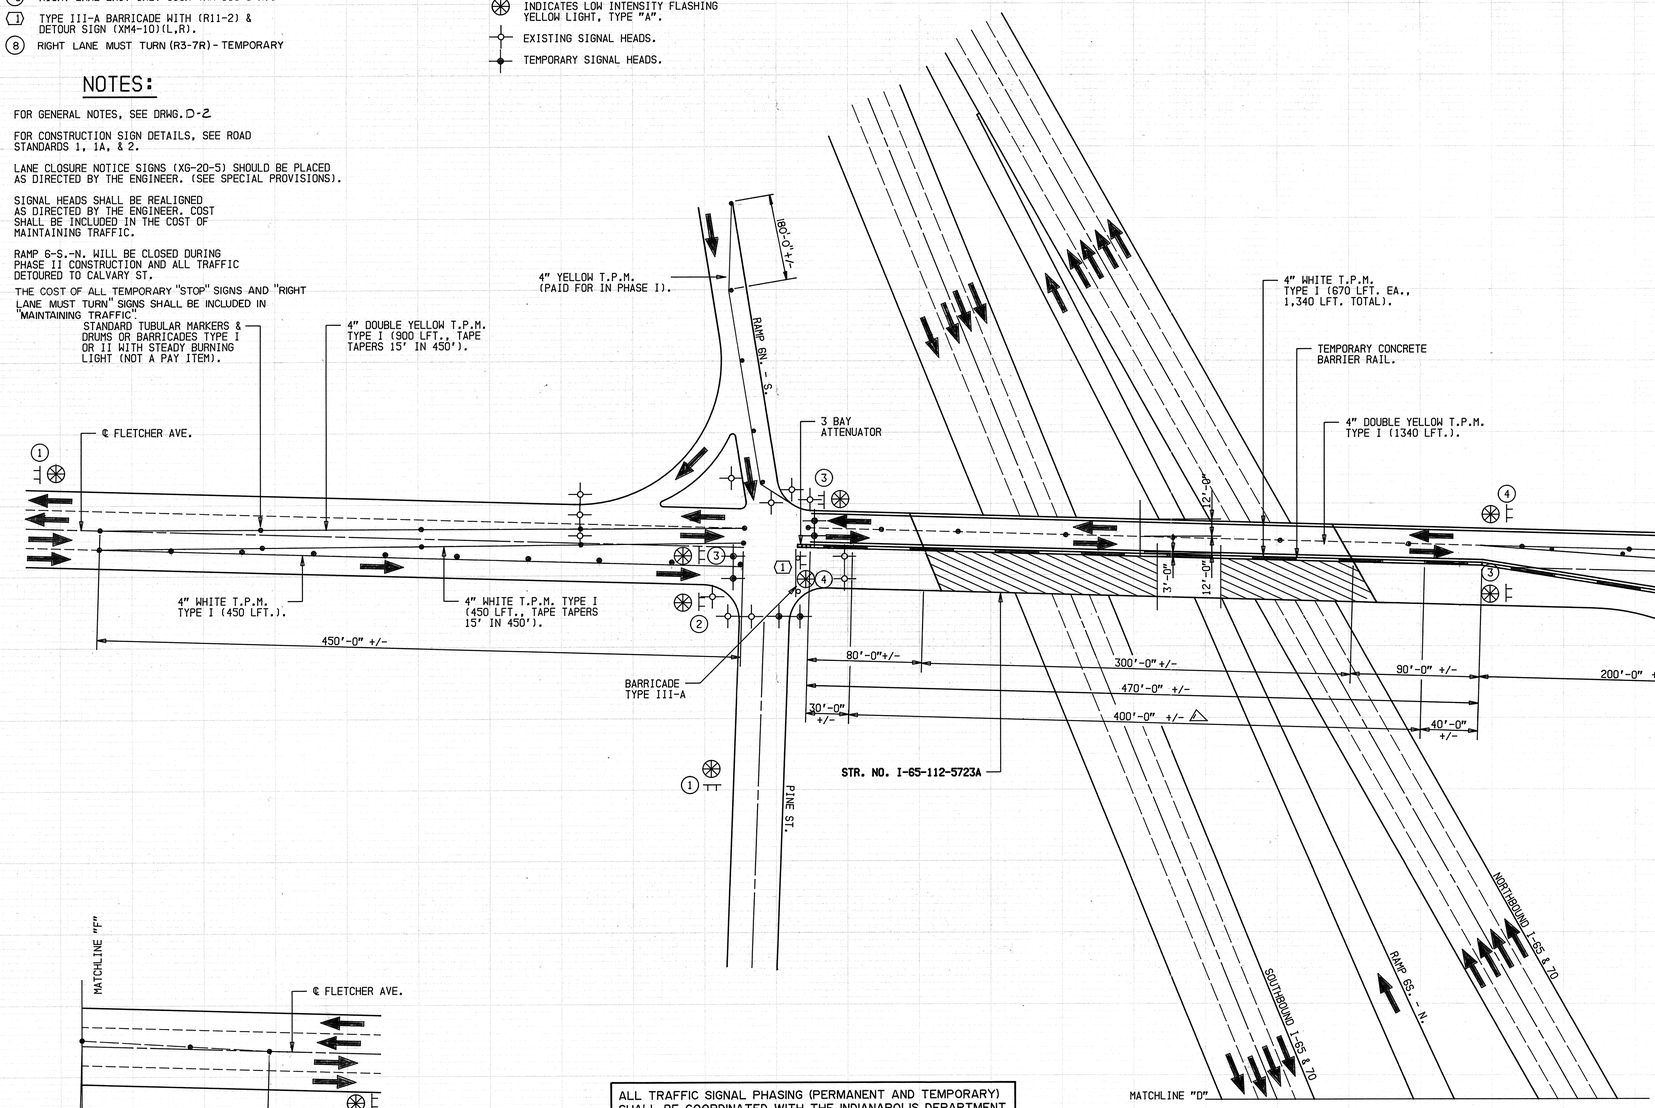

ALL TRAFFIC SIGNAL PHASING (PERMANENT AND TEMPORARY) SHALL BE COORDINATED WITH THE INDIANAPOLIS DEPARTMENT OF TRANSPORTATION AND I.N.D.O.T.

PHASE II CONSTRUCTION

TRAFFIC MAINTENANCE PHASE II CONSTRUCTION

INDIANA DEPARTMENT OF TRANSPORTATION

SCALE:- AS NOTED DATE:- November 7, 1991

SUBMITTED FOR APPROVAL: Richard T. O'Connor

DRAWING:- OF SHEET:- 6 OF 15

PROJECT:- NH/65-3(245)111

BRIDGE CONTRACT NO. B-19752

BRIDGE FILE:- I-65-112-5723A

RICHARD T. O'CONNOR REGISTERED No. 17778 STATE OF INDIANA PROFESSIONAL ENGINEER

DESIGNED	JET	C'K'D	
DRAWN	DJS	C'K'D	JET
TRACED		C'K'D	


SF-22317

91013/3311

REV. 11/20/92 REVISED TRAFFIC MAINTENANCE AT INTERSECTIONS

TP118

9-11-91 10:40 PM - 10:55 PM .25 Hours DRS

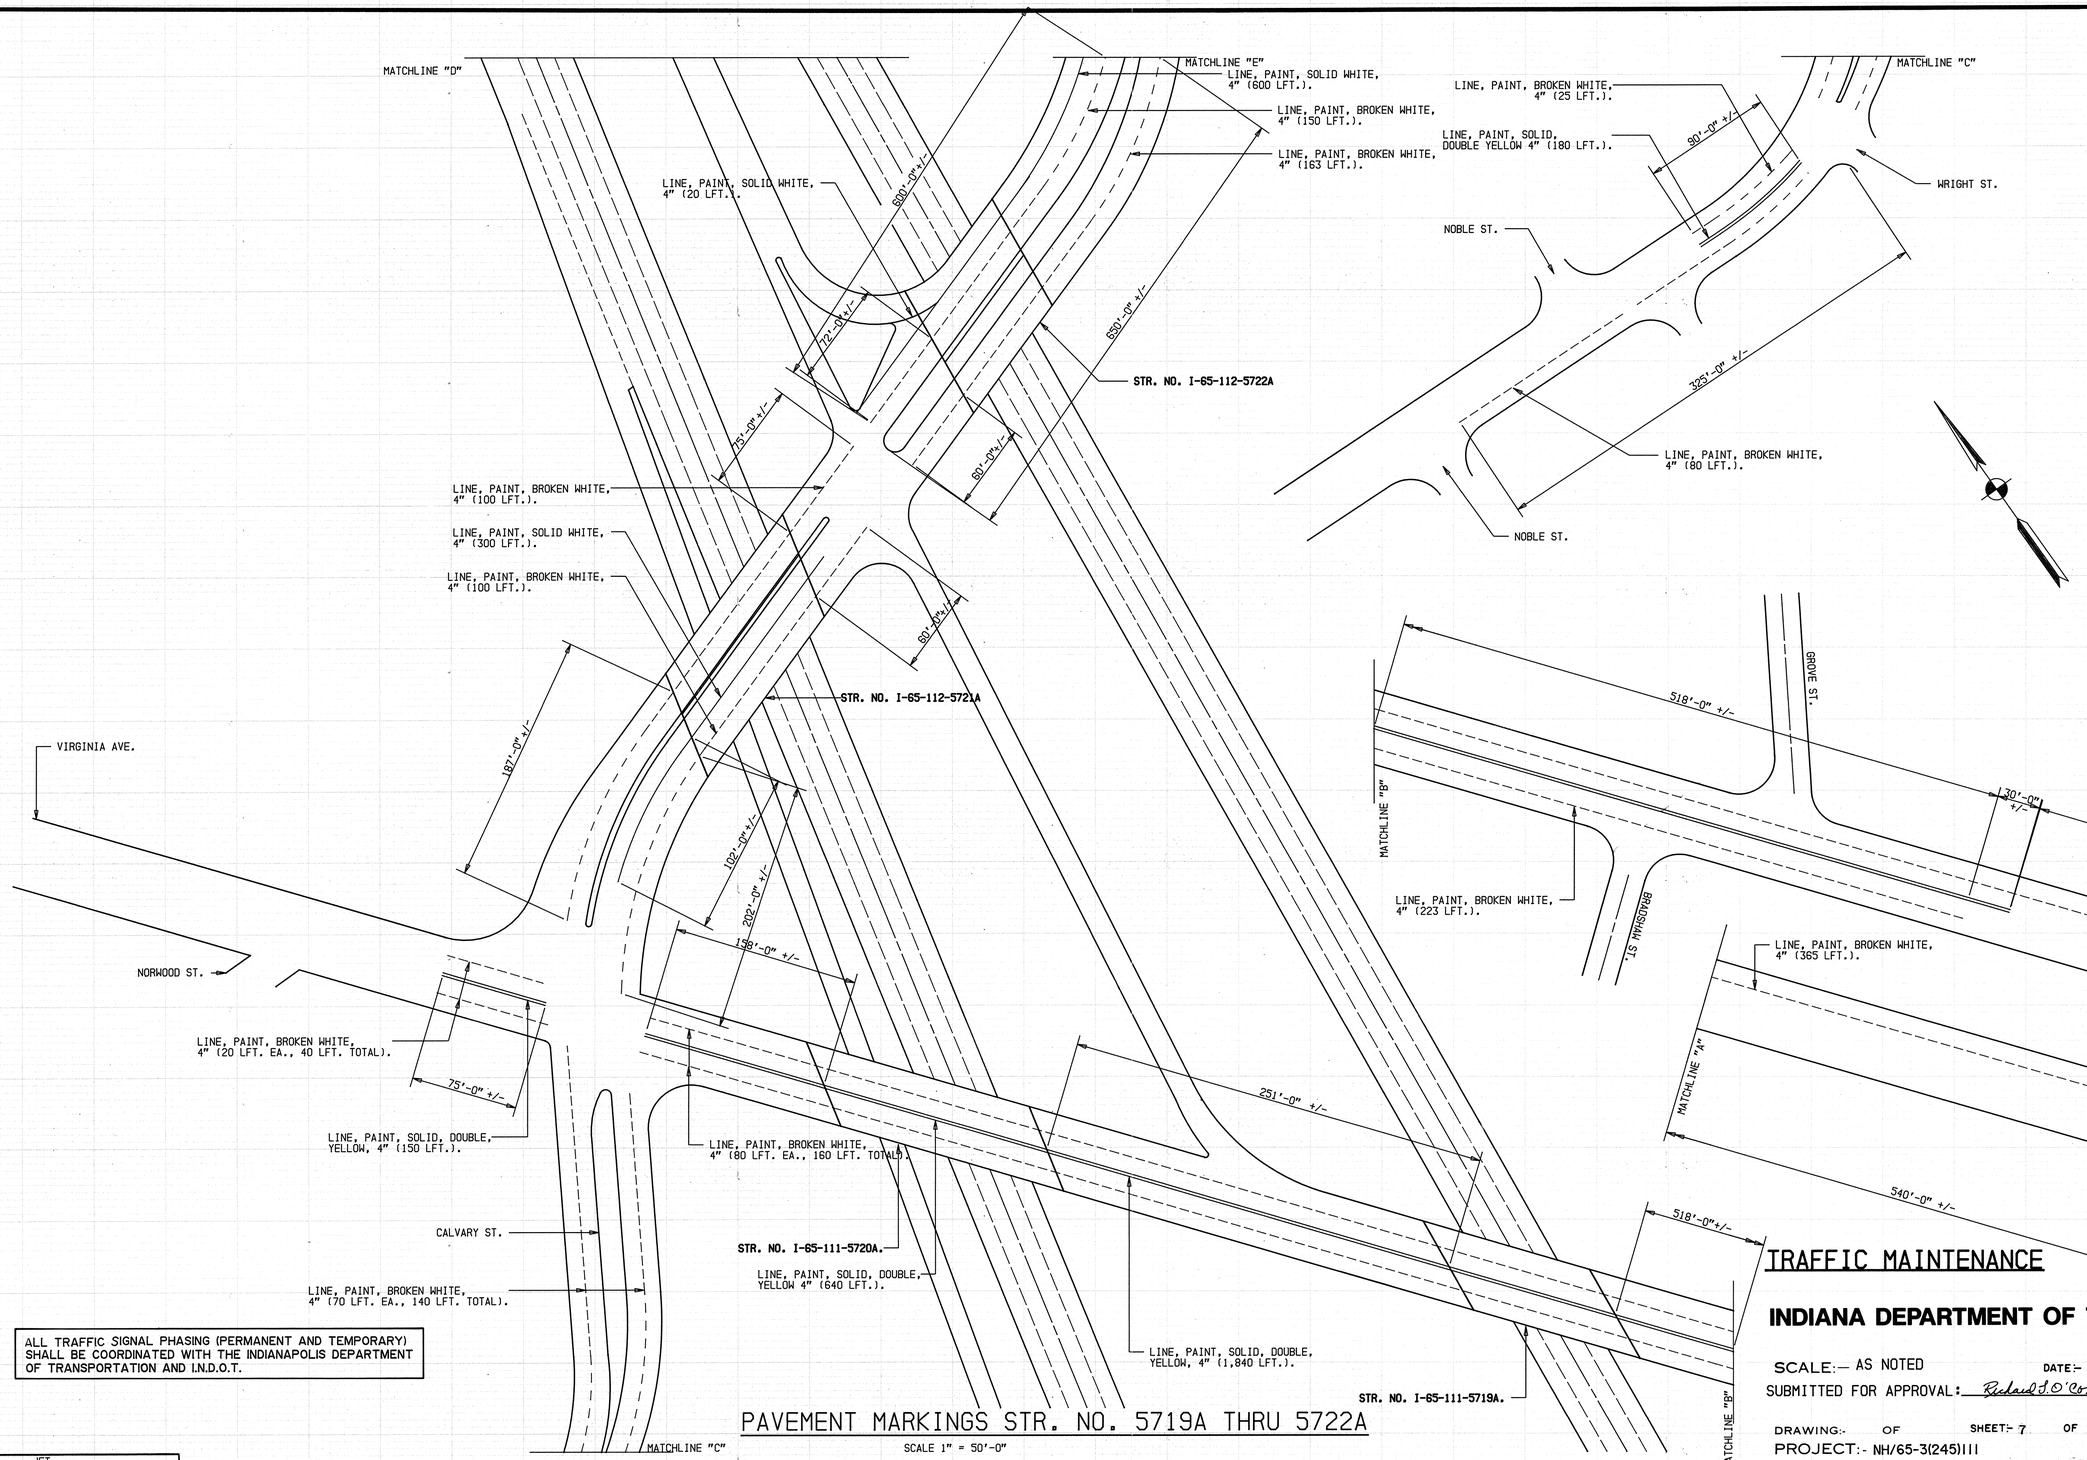

ALL TRAFFIC SIGNAL PHASING (PERMANENT AND TEMPORARY) SHALL BE COORDINATED WITH THE INDIANAPOLIS DEPARTMENT OF TRANSPORTATION AND I.N.D.O.T.

PAVEMENT MARKINGS STR. NO. 5719A THRU 5722A

SCALE 1" = 50'-0"

TRAFFIC MAINTENANCE

INDIANA DEPARTMENT OF TRANSPORTATION

SCALE:— AS NOTED DATE:- November 7, 1991

SUBMITTED FOR APPROVAL: Richard J. O'Connor

DRAWING:- OF SHEET:- 7 OF 15

PROJECT:- NH/65-3(245)111

BRIDGE CONTRACT NO. B-19752


BRIDGE FILE:- I-65-111-5719A THRU I-65-112-5722A

RICHARD T. O'CONNOR REGISTERED No. 17778 STATE OF INDIANA PROFESSIONAL ENGINEER


DESIGNED	JET	C'K'D	
DRAWN	DJS	C'K'D	JET
TRACED		C'K'D	

SF-22317


91013/3307,3308,3309,3310

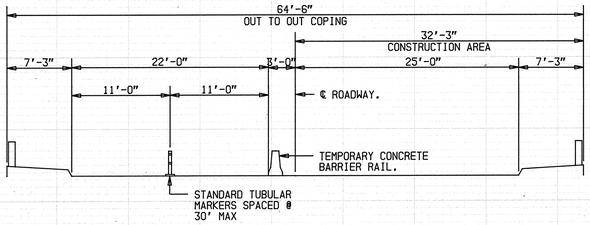


TYPICAL SECTION PHASE I STR. NO. 5719A & 5720A

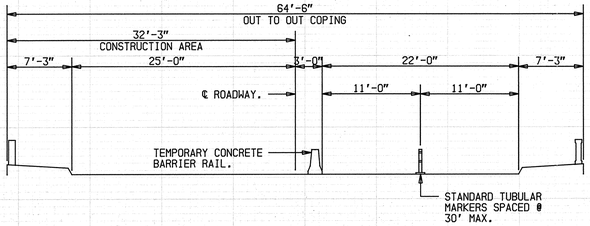


TYPICAL SECTION PHASE II STR. NO. 5719A & 5720A

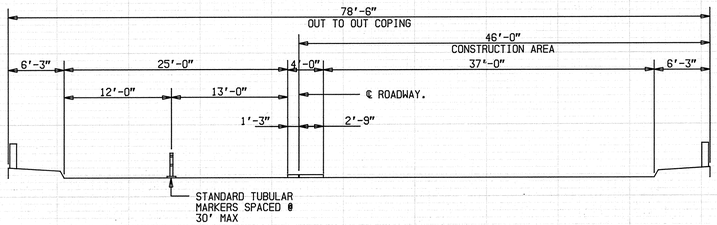


TYPICAL SECTION PHASE I STR. NO. 5721A

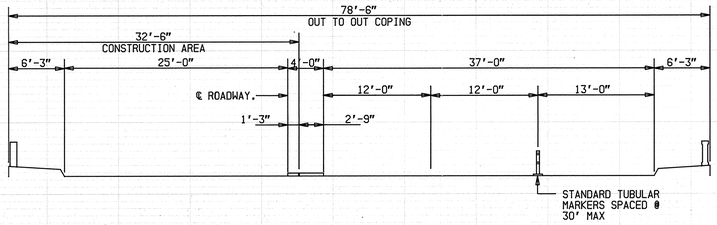

TYPICAL SECTION PHASE II STR. NO. 5721A

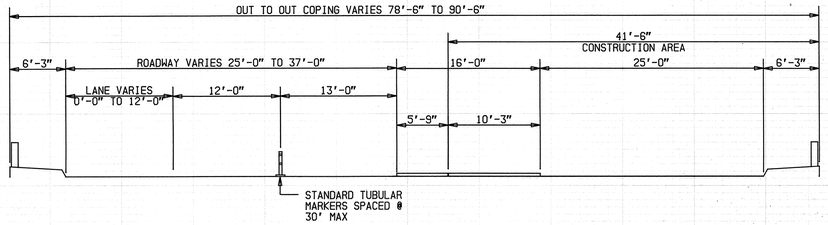

TYPICAL SECTION PHASE I STR. NO. 5722A

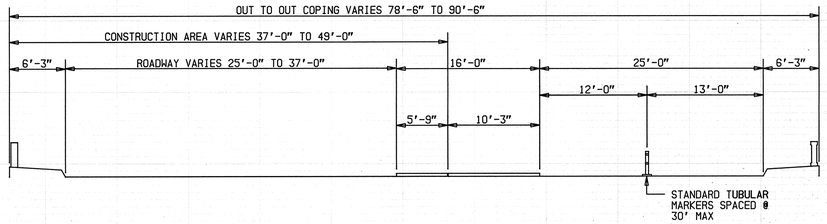

TYPICAL SECTION PHASE II STR. NO. 5722A

SEPARATE PAY ITEMS

	5719A	5720A	5721A	5722A
MAINTAINING TRAFFIC	* 1 LSUM	* 1 LSUM	* 1 LSUM	* 1 LSUM
TEMPORARY TRAFFIC SIGNALS	** 1 LSUM	** 1 LSUM	** 1 LSUM	** 1 LSUM
TEMPORARY CONCRETE BARRIER RAIL	200 LFT.	0 LFT.	0 LFT.	0 LFT.
TEMPORARY CONCRETE BARRIER RAIL (ANCHORED)	420 LFT.	320 LFT.	0 LFT.	0 LFT.
CONSTRUCTION SIGNS (TYPE A)	11 EACH	21 EACH	5 EACH	6 EACH
CONSTRUCTION SIGNS (TYPE B)	4 EACH	4 EACH	0 EACH	0 EACH
LINE, PAINT, SOLID, YELLOW, 4"	1,840 LFT.	970 LFT.	0 LFT.	0 LFT.
LINE, PAINT, BROKEN, WHITE, 4"	588 LFT.	445 LFT.	200 LFT.	313 LFT.
LINE, PAINT, SOLID, WHITE, 4"	0 LFT.	0 LFT.	300 LFT.	620 LFT.
REMOVAL OF LINE, PAINT	883 LFT.	1,004 LFT.	127 LFT.	905 LFT.
TEMPORARY PAVEMENT MARKING, TYPE I, WHITE, 4"	2,422 LFT.	1,453 LFT.	3,236 LFT.	3,797 LFT.
TEMPORARY PAVEMENT MARKING, TYPE I, YELLOW, 4"	2,708 LFT.	1,638 LFT.	2,981 LFT.	3,364 LFT.
TEMPORARY PAVEMENT MARKING, TYPE II, WHITE, 4"	242 LFT.	324 LFT.	276 LFT.	279 LFT.
TEMPORARY PAVEMENT MARKING, TYPE II, YELLOW, 4"	242 LFT.	324 LFT.	276 LFT.	186 LFT.
BARRICADE TYPE III-A	0 EACH	2 EACH	2 EACH	2 EACH
3 BAY G.R.E.A.T. CZ.	0 EACH	1 EACH	0 EACH	0 EACH

* - COST OF STANDARD TUBULAR MARKERS AND STANDARD DRUMS OR BARRICADES TYPE I OR II SHALL BE INCLUDED IN THE COST OF "MAINTAINING TRAFFIC" (1 LSUM)

** - MAINTENANCE OF SIGNALS IS TO BE BY THE CONTRACTOR DURING THE CONSTRUCTION PERIOD. SEE THE "SPECIAL PROVISIONS."

NOTES

APPROVED LIGHTS SHALL MARK SIGNS AND BARRICADES CONTINUOUSLY AT NIGHT.

ALL TRAFFIC SIGNAL PHASING (PERMANENT AND TEMPORARY) SHALL BE COORDINATED WITH THE INDIANAPOLIS DEPARTMENT OF TRANSPORTATION AND I.N.D.O.T.

TRAFFIC MAINTENANCE

INDIANA DEPARTMENT OF TRANSPORTATION

SCALE:- AS NOTED DATE:- November 7, 1991

SUBMITTED FOR APPROVAL: Richard T. O'Connor

DRAWING:- OF SHEET:- 8 OF 15

PROJECT: NH/65-3(245)111

BRIDGE CONTRACT NO. B-19752


BRIDGE FILE:- I-65-111-5719A THRU I-65-112-5722A

RICHARD T. O'CONNOR REGISTERED No. 17778 STATE OF INDIANA PROFESSIONAL ENGINEER


DESIGNED	JET	C'K'D	
DRAWN	DJS	C'K'D	JET
TRACED		C'K'D	

SF-22317


91013/3307,3308,3309,3310

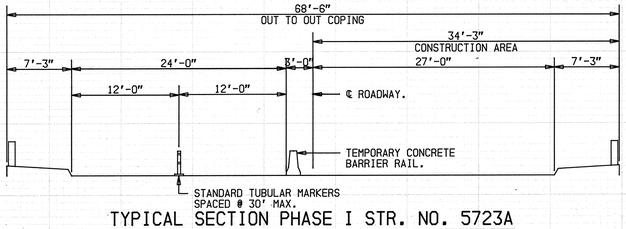


TYPICAL SECTION PHASE I STR. NO. 5723A

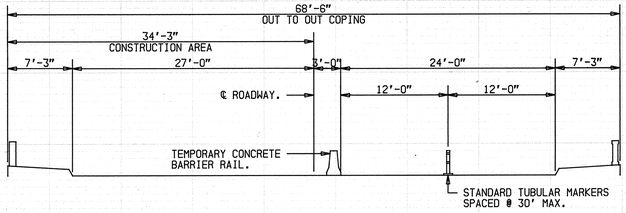

TYPICAL SECTION PHASE II STR. NO. 5723A

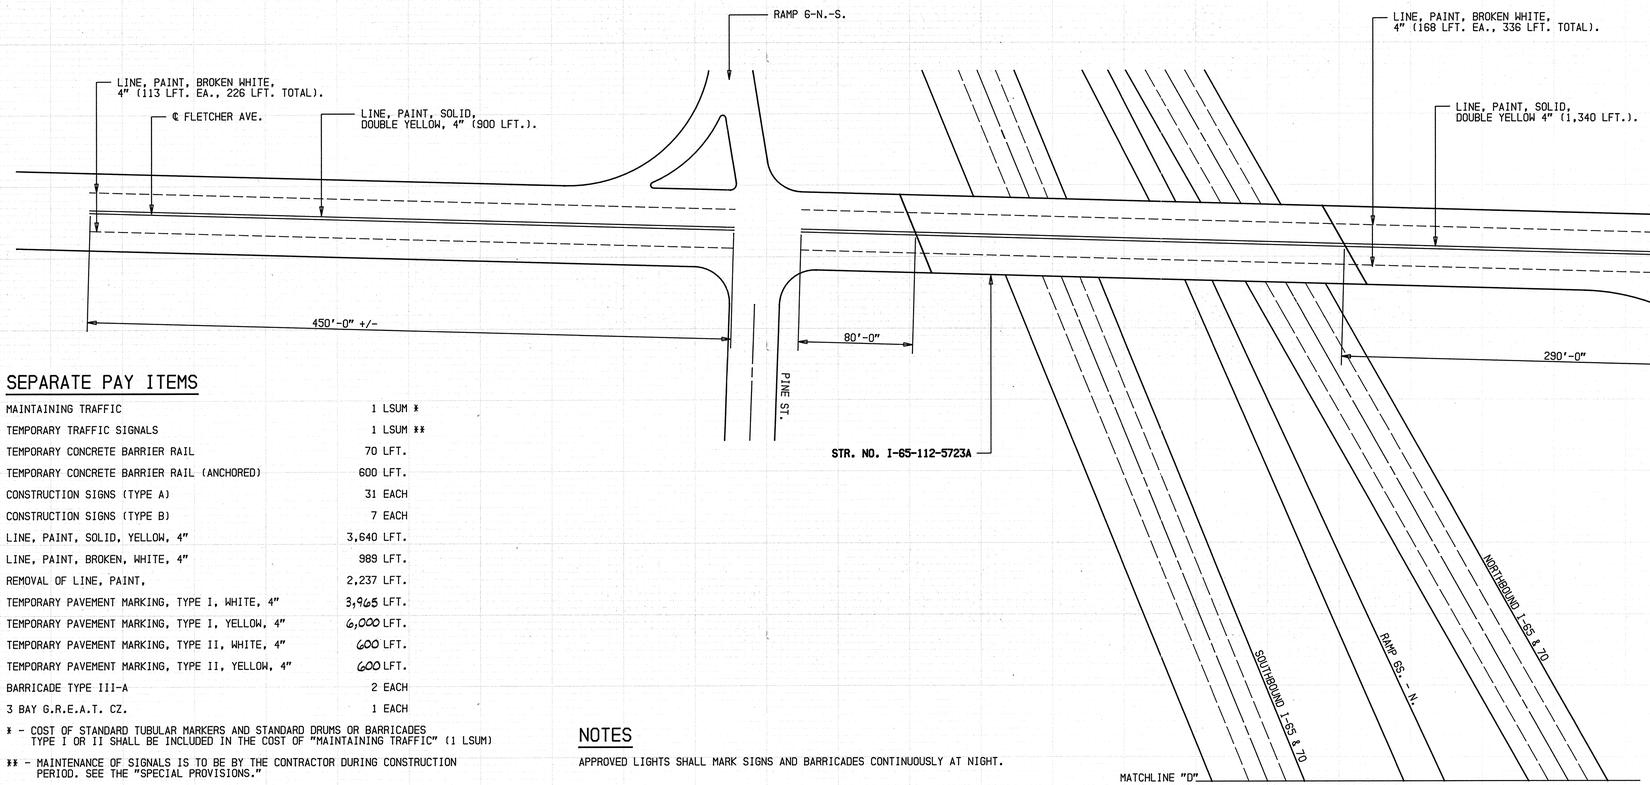

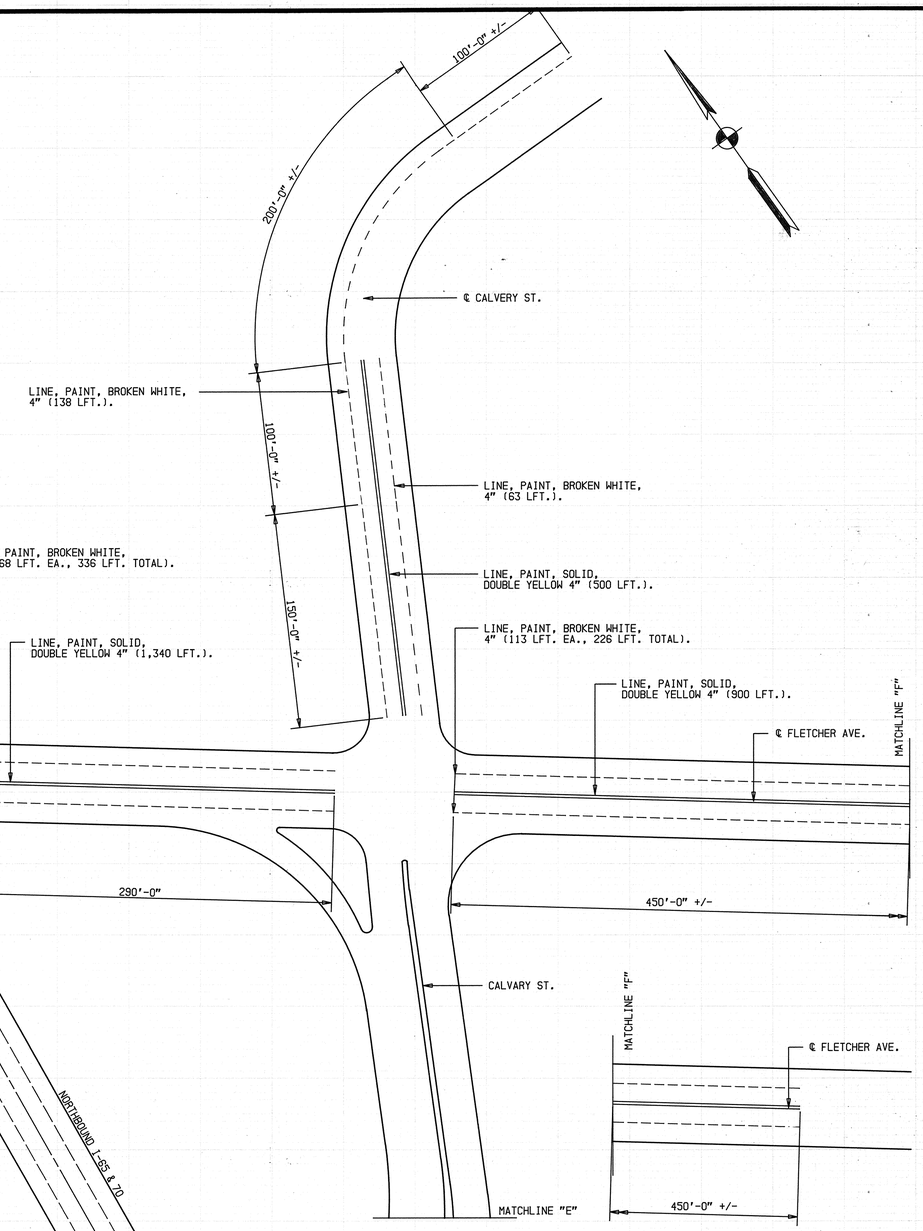

SEPARATE PAY ITEMS

MAINTAINING TRAFFIC	1 LSUM *
TEMPORARY TRAFFIC SIGNALS	1 LSUM **
TEMPORARY CONCRETE BARRIER RAIL	70 LFT.
TEMPORARY CONCRETE BARRIER RAIL (ANCHORED)	600 LFT.
CONSTRUCTION SIGNS (TYPE A)	31 EACH
CONSTRUCTION SIGNS (TYPE B)	7 EACH
LINE, PAINT, SOLID, YELLOW, 4"	3,640 LFT.
LINE, PAINT, BROKEN, WHITE, 4"	989 LFT.
REMOVAL OF LINE, PAINT,	2,237 LFT.
TEMPORARY PAVEMENT MARKING, TYPE I, WHITE, 4"	3,965 LFT.
TEMPORARY PAVEMENT MARKING, TYPE I, YELLOW, 4"	6,000 LFT.
TEMPORARY PAVEMENT MARKING, TYPE II, WHITE, 4"	600 LFT.
TEMPORARY PAVEMENT MARKING, TYPE II, YELLOW, 4"	600 LFT.
BARRICADE TYPE III-A	2 EACH
3 BAY G.R.E.A.T. CZ.	1 EACH

* - COST OF STANDARD TUBULAR MARKERS AND STANDARD DRUMS OR BARRICADES TYPE I OR II SHALL BE INCLUDED IN THE COST OF "MAINTAINING TRAFFIC" (1 LSUM)

** - MAINTENANCE OF SIGNALS IS TO BE BY THE CONTRACTOR DURING CONSTRUCTION PERIOD. SEE THE "SPECIAL PROVISIONS."

NOTES

APPROVED LIGHTS SHALL MARK SIGNS AND BARRICADES CONTINUOUSLY AT NIGHT.

PAVEMENT MARKINGS STR. NO. I-65-112-5723A

ALL TRAFFIC SIGNAL PHASING (PERMANENT AND TEMPORARY) SHALL BE COORDINATED WITH THE INDIANAPOLIS DEPARTMENT OF TRANSPORTATION AND I.N.D.O.T.

TRAFFIC MAINTENANCE

INDIANA DEPARTMENT OF TRANSPORTATION

SCALE:- AS NOTED DATE:- November 7, 1991

SUBMITTED FOR APPROVAL: Richard T. O'Connor

DRAWING:- OF SHEET:- 9 OF 15

PROJECT:- NH/65-3(245)111

BRIDGE CONTRACT NO. B-19752

BRIDGE FILE:- I-65-112-5723A

RICHARD T. O'CONNOR REGISTERED No. 17778 STATE OF INDIANA PROFESSIONAL ENGINEER

DESIGNED	JET	C'K'D	
DRAWN	DJS	C'K'D	JET
TRACED		C'K'D	

SF-22317

91013/3311

TP118

CONTRACT No. B-6877

INDEX

PROJECT	STRUCTURE	TYPE	SPAN	OVER	STATION	CONTRACT NO.
I-65-3(106)III	I-65-112-5723	STEEL GIRDER	2 @ 147'-0 SKEW: 28°-47'-15" Lt.	FLETCHER AVE OVER I-65 & RAMP '6S-N'	388+40.43 I-65(S.B.) & 15125.80 FLETCHER 387+83.86 I-65(N.B.) &14+33.61 FLETCHER	B-6877

SHEET NO.	SHEET DESIGNATION	SUBJECT	R.P.E. APPROVAL
1	ONE SHEET	INDEX	
2	ONE SHEET	TEST BORINGS	
3	S1	LAYOUT	
4	S2	GENERAL PLAN	
5	S3	ABUT 1	
6	S4	ABUT 1 DETAILS	
7	S5	ABUT 3	
8	S6	ABUT 3 DETAILS	
9	S7	PIER 2	
10	S8	FRAMING PLAN	
11	S9	STEEL DETAILS	
12	S10	STEEL DETAILS	
13	S11	STEEL DETAILS	
14	S12	STEEL DETAILS	
15	S13	STEEL DETAILS	
16	S14	STEEL DETAILS	
17	S15	STEEL DETAILS	
18	S16	FLOOR DETAILS	
19	S17	FLOOR DETAILS	
20	S18	FLOOR DETAILS	
21	ONE SHEET	SUMMARY SHEET	
20A	S18A	DETAILS-C.T.I.P.C. OVERLAY AND EXP. JOINT-TYPE BS6	

STATE OF INDIANA
INDIANA STATE HIGHWAY COMMISSION

BRIDGE PLANS
FOR SPANS OVER 20 FEET
ON
PROJECT NO. I-65-3 { (59) III P.E. PHASE I; (78) III P.E. FINAL PHASE; (106) III CONSTR.; (79) III R/W

FLETCHER AVE. OVER I-65 & RAMP 6S-N

BEGINNING AT A POINT ON ℄ OF EXISTING FLETCHER AVE., APPROX. 97.76 FT SOUTHEAST OF IT'S INTERSECTION WITH ℄ OF PROPOSED I-65 (N.B.) AND EXTENDING IN A NORTHWESTERLY DIRECTION FOR APPROX. 299.70 FT. TO A POINT ON ℄ OF EXISTING FLETCHER AVE. APPROX 201.94 NORTHWEST OF ITS INTERSECTION WITH ℄ OF PROPOSED I-65 (N.B.) ALL IN SECTION 12, T.15 N., R.3N., CENTER TOWNSHIP, MARION COUNTY.

ROADWAY LENGTH: 0.000 MILES
BRIDGE LENGTH: 0.056 MILES
TOTAL LENGTH: 0.056 MILES

MAX. GRADE: -1.62 %


BRIDGES OVER 20' SPAN

PUBLIC ROAD MILEAGE NO.	STATE	PROJECT NO.	FISCAL YEAR	SHEET NO.	TOTAL SHEETS
4	IND.	I-65-3(106)III	1971	1	33


INDEX CONTINUED
STANDARD DRAWINGS

SHEET NO.	SHEET DESIGNATION	SUBJECT	R.P.E. APPROVAL	ADOPTED "A" REVISION "R"
22	BRIDGE STD. C1	STANDARD MISCELLANEOUS DETAILS		R-5-1-72
23	BRIDGE STD. C3	STANDARD MISCELLANEOUS DETAILS		R-5-1-72
24	BRIDGE STD. D	CASTING DETAILS ROADWAY DRAINS		R-5-1-72
	BRIDGE STD. F	ROADWAY DRAIN OUTLET DETAILS	3-16-72	R-1-1-72
	BRIDGE STD.			
	BRIDGE STD. J	EXPANSION JOINT		
	BRIDGE STD. M	MISCELLANEOUS APPROACH DETAILS		
	BRIDGE STD. M4	R.C. BRIDGE APPROACH TURNOUT DETAILS-12'6" SHOULDERS		
	BRIDGE STD. M5	SLOPEWALL AND DRAINAGE DETAILS		
	BRIDGE STD.			
	BRIDGE STD. PB	PRESTRESSED CONCRETE TYP I-BEAMS		
	BRIDGE STD. PBX	PRESTRESSED BOX BEAMS		
	BRIDGE STD. PB	PRESTRESSED COMPOSITE BOX BEAMS WIDE		
	BRIDGE STD. PB10	TOLERANCES FOR FABRICATION OF PRESTRESSED BEAMS		
	BRIDGE STD. PB11	ELASTOMERIC BEARING PAD DETAILS		
25	BRIDGE STD. BR1	ALUMINUM RAILING-TYPE 6	7-26-71	R-3-1-71
26	BRIDGE STD. BR2	ALUMINUM RAILING DETAILS	7-26-71	R-3-1-71
27	BRIDGE STD. BR3	STEEL RAILING-TYPE 6	7-26-71	R-3-1-71
28	BRIDGE STD. BR4	STEEL RAILING DETAILS	7-26-71	R-3-1-71
28A	BRIDGE STD. REA	BRIDGE LIGHTING DETAILS	7-17-72	R-8-2-71
	BRIDGE STD.			
	BRIDGE STD.			
29	BRIDGE S1 J S1	TYPICAL DETAILS FOR PLACING "B" BORROW	1-17-72	R-8-2-71
	BRIDGE STD. S2	TYPICAL DETAILS FOR PLACING GRADE "B" SPECIAL BORROW		
	BRIDGE STD. T SHEET A	STANDARD TEMPORARY BRIDGE		
	BRIDGE STD. T SHEET B	STANDARD TEMPORARY BRIDGE		
	ROAD STD. SHEET A	STANDARD PAVEMENT JOINTS		
	ROAD STD. SHEET	MISCELLANEOUS STANDARDS		
30	ROAD STD. SHEET MBE	MISCELLANEOUS STANDARDS		
31	ROAD STD. SHEET MBH	MISCELLANEOUS STANDARDS	3-7-72	R-1-1-72
32	ROAD STD. SHEET MC	MISCELLANEOUS STANDARDS	4-11-68	R-1-12-68
33	ROAD STD. SHEET ME	MISCELLANEOUS STANDARDS	7-2-71	R-8-1-71
	ROAD STD. SHEET	MISCELLANEOUS STANDARDS	7-2-71	R-8-1-71
	ROAD STD. SHEET M	MISCELLANEOUS STANDARDS		
	ROAD STD. SHEET ME1	MISCELLANEOUS STANDARDS		
	ROAD STD. SHEET MF	MISCELLANEOUS STRUCTURE STANDARDS		
	ROAD STD. SHEET MG	MISCELLANEOUS STRUCTURE STANDARDS		
	ROAD STD. SHEET K	MISCELLANEOUS STANDARDS		
	ROAD STD. SHEET MH	MISCELLANEOUS STANDARDS		
	ROAD STD. SHEET MJ	MISCELLANEOUS STANDARDS		
	ROAD STD. SHEET N	MISCELLANEOUS STANDARDS		
	ROAD STD. SHEET MN	MISCELLANEOUS STANDARDS		
	ROAD STD. SHEET MP	MISCELLANEOUS STANDARDS		
	ROAD STD. SHEET MP1	MISCELLANEOUS STANDARDS		
	ROAD STD. SHEET MQ	MISCELLANEOUS STANDARDS		
	ROAD STD. SHEET MR	MISCELLANEOUS STANDARDS		
	ROAD STD. SHEET MR1	MISCELLANEOUS STANDARDS		
	ROAD STD. SHEET S	MISCELLANEOUS STANDARDS CENTER DITCH INLETS		
	ROAD STD. SHEET S1	MISCELLANEOUS STANDARDS CENTER DITCH INLETS		
	ROAD STD. SHEET MT	MISCELLANEOUS STANDARDS		
	ROAD STD. SHEET	MISCELLANEOUS STANDARDS		
	ROAD STD. SHEET	MISCELLANEOUS STANDARDS		
	ROAD STD. SHEET	MISCELLANEOUS STANDARDS		
	ROAD STD. SHEET	MISCELLANEOUS STANDARDS		
	ROAD STD. SHEET	MISCELLANEOUS STANDARDS		
	ROAD STD. SHEET	MISCELLANEOUS STANDARDS		
	ROAD STD.	STANDARD STRUCTURE CONNECTIONS FOR EXTENSION		
	ROAD STD.	STANDARD REINF. CONC. BOX CULVERTS		
	ROAD STD.	STANDARD REINF. CONC. BOX CULVERTS-SK. END & WING DETAILS		
	ROAD STD.	STANDARD REINF. CONC. CULVERTS-SLAB TOP TYPE (W.F.)		
	ROAD STD.	STANDARD REINF. CONC. CULVERTS-SLAB TOP TYPE (U.F.)		
	ROAD STD. SHEET GR1	BEAM GUARD RAIL		
	ROAD STD.	STANDARD REINF. CONCRETE ARCH-12' SPAN		
	ROAD STD.	STANDARD HEADWALLS		
	ROAD STD.	STANDARD STRUCTURAL PLATE ARCH		
	ROAD STD.	CONCRETE WINGS FOR STD. STRUCTURAL PLATE ARCHES		
	ROAD STD.	STANDARDS FOR SUPERELEVATION		
	ROAD STD. SHEET 1 DETOURS	STANDARD DETOUR SIGNS		
	ROAD STD. SHEET 2 DETOURS	STANDARD DETOUR SIGNS		
	ROAD STD. SHEET 3 DETOURS	STANDARD DETOUR SIGNS		
	ROAD STD. SHEET 3A DETOURS	STANDARD DETOUR SIGNS		
	ROAD STD. SHEET 1 DETOURS	CONSTRUCTION IDENTIFICATION SIGNS		

TRAFFIC DATA	I-65	FLETCHER AVE.
A.D.T. (1972)	37,930 V.P.D.	10,070 V.P.D.
A.D.T. (1992 PROJECTED)	70,000 V.P.D.	23,043 V.P.D.
A.D.T. (19 PROJECTED)		V.P.D.
TRUCKS	A.D.T.=14%, D.H.V.=7%	A.D.T.=14%, D.H.V.=7 %
DESIGN SPEED	50 M.P.H.	30 M.P.H.
ACCESS CONTROL	FULL	FULL

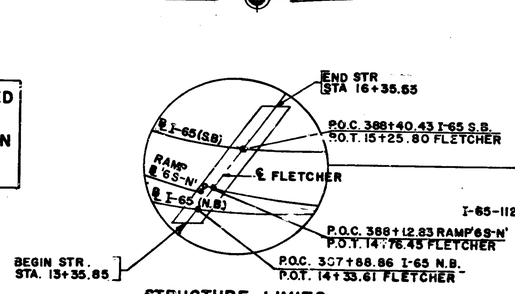

STRUCTURE LIMITS
I-65-112-5723

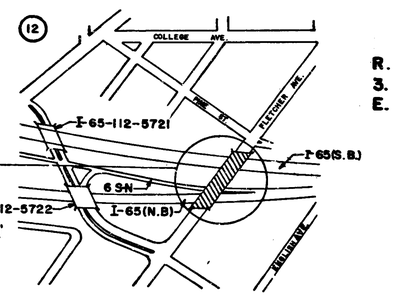

MARION COUNTY
T. 15 N.

R. 3. E.

THESE PLANS PREPARED BY
CHAS. W. COLE & SON
ENGINEERS
SOUTH BEND, INDIANA

INDIANA STATE HIGHWAY COMMISSION
STANDARD SPECIFICATIONS DATED 1971
TO BE USED WITH THESE PLANS.

FINAL PHASE
SUBMITTED for APPROVAL 3-29-71

REGISTERED PROFESSIONAL ENGINEER
STATE of INDIANA

REVISIONS	
DATE	SHEET NO.
12-16-71	3,4 thru 8, 12, 18 thru 21, 28, 29, 31 thru 33; 28A Added.
2-23-72	1, 2 thru 8, 18 thru 21
2-23-72	9, 11, 12, 15
8-3-73	1, 4, 5&7, 12, 16 thru 21; 20A Added.

RECOMMENDED FOR APPROVAL 5/27/71

ENGINEER OF BRIDGE DESIGN-INDIANA STATE HIGHWAY COMMISSION

F. N. RICHARDSON
REGISTERED No. 3042
STATE OF INDIANA
PROFESSIONAL ENGINEER

APPROVED 5-28-1971

CHIEF HIGHWAY ENGINEER-INDIANA STATE HIGHWAY COMMISSION

DEPARTMENT OF COMMERCE
BUREAU OF PUBLIC ROADS
APPROVED:-

DIVISION ENGINEER — DATE

BRIDGE FILE:- I-65-112-5723

Rev. 12-16-71 Markup E.B. Chk. J.J.W.
Rev. 2-23-72 Revised J.J.W. Chk. A.W.M.
Rev. 12-28-72 J.D.M.
Rev. 8-3-73 H.R.P./C.M.

PUBLIC ROAD REGION NO.	STATE	PROJECT NO.	FISCAL YEAR	SHEET NO.	TOTAL SHEETS
4	IND.	I-65-3(106)111	1971	2	33

BORING NO.	B-42
STATION	388+90
OFFSET	3' Lt. ℄ I-65 S.B.
GROUND EL.	723.8

SAMPLE NO.	EL.	N	DESCRIPTION
	723.8		Ground Level
C-1	723.3	Push	Black slightly moist sandy SILT (Topsoil)
2	721.3	21	Brown slightly moist med. dense sandy SILT with a trace of clay.
3	716.8	24	
	717.8		
4	713.8	44	Brown moist medium dense to dense fine to medium SAND with a trace of gravel.
	711.3		
W.L.C. ▼ 5	709.8	32	Gray and brown moist to wet dense fine to coarse SAND with some fine to coarse gravel.
	707.8		
6	703.8	21	Brown moist hard sandy SILT with a trace of gravel (hardpan).
	701.3		Green and gray moist very stiff silty CLAY with a trace of sand and gravel.
7	698.8	34	
8	693.8	28	Gray moist very stiff to hard clayey SILT with some sand and a trace of fine gravel.
9	688.8	36	
10	683.8	38	
C-2	683.3		
11	678.8	49	Gray to brownish gray dense fine SAND.
12	675.3	48	
C-3	674.8		
C-4	673.8		Brown wet dense to very dense fine to coarse SAND with a trace of gravel.
			END OF BORING
			Depth of Boring 50'
			W.L.C. 23.8'

723 B-1
387+81
40' Lt. ℄ I-65 N.B.
724.5


SAMPLE NO.	EL.	N	DESCRIPTION
	724.5		Ground Level
1	721.0	5	Brown moist soft LOAM
	719.5		
2	718.5	27	Brown moist medium dense fine SAND with trace of gravel.
	717.5		
	716.5		Brown moist hard LOAM.
C-3	716.0	19	Brown moist medium dense fine SAND.
	712.5		
4	711.0	26	
W.L.C. ▼			Brown wet medium dense fine to coarse Sand and fine to medium GRAVEL.
5	706.0	26	
	705.0		
6	701.0	27	Gray moist very stiff silty clay LOAM
			Bott. Ftg. Pier 2 El. 698.59
7	696.0	25	
	692.5		
8	691.0	23	Gray and brown moist very stiff silty CLAY with trace of bits of organic matter.
	687.5		
9	686.0	20	Gray moist very stiff sandy LOAM.
	682.5		
10	681.0	48	Gray moist very stiff silty clay LOAM
C-4	680.5		
11	676.0	35	Brown wet dense to very dense fine to coarse SAND
12	671.0	58	
13	666.0	62	
14	661.0	56	
C-5	658.5		Brown wet very dense fine to coarse SAND and fine to coarse GRAVEL.
15	656.0	119	
C-6	655.5		Gray and brown dry hard LOAM.
C-7	654.5		END OF BORING
			Depth of Boring 70'
			W.L.24 14.5' W.L.C. 16.0'

723 B-2
387+87
61' Rt. ℄ I-65 N.B.
724.5

SAMPLE NO.	EL.	N	DESCRIPTION
	724.5		Ground Level
	722.0		Brown dry stiff silty LOAM.
1	721.0	12	Brown moist stiff silty clay LOAM
	719.0		
C-2	718.5	18	Brown moist very stiff LOAM.
	716.5		
C-3	716.0	15	Brown moist medium dense fine SAND
C-4	714.5		
4	711.0	20	Brown moist to wet medium dense fine to medium SAND with a little gravel.
W.L.C. ▼			
5	706.0	20	
	702.5		Gray moist very stiff silty clay LOAM
6	701.0	22	Gray wet med. stiff LOAM
C-5	700.5		Gray moist very stiff silty LOAM with trace 1" clay seams.
	697.5		
7	696.0	29	Dark gray moist very stiff CLAY.
	692.5		
8	691.0	21	Gray and brown moist very stiff silty CLAY with trace of bits of organic matter.
	687.5		
9	686.0	25	Gray moist very stiff silty LOAM.
10	681.0	52	
			Brown wet very dense fine to coarse SAND and fine to coarse GRAVEL- medium dense at 48.5'.
11	676.0	29	
C-6	674.5		Brown wet medium dense fine SAND
			END OF BORING
			Depth of Boring 50'
			W.L.C. 13.0'
			W.L.24 Filled

723 B-3
388+44
74' Lt. ℄ I-65 S.B.
724.5

SAMPLE NO.	EL.	N	DESCRIPTION
	724.5		Ground Level
1	721.0	16	Brown moist very stiff silty LOAM
2	718.5	21	
	717.0		
3	716.0	31	Brown moist dense fine SAND
4	711.5	101/2"	
	707.0		
5	705.0	28	Gray moist very stiff silty LOAM
6	701.0	23	
	697.5		
7	696.0	31	Gray moist hard to stiff silty clay LOAM.
8	691.0	26	
C-7	690.0		Black moist very stiff CLAY.
	689.5		Gray and brown moist hard silty clay LOAM with trace of bits of organic matter.
	687.5		
9	686.0	26	Gray moist very stiff silty CLAY.
	682.5		
10	681.0	89	Brown to gray moist hard silty LOAM.
11	676.0	53	
C-8	675.5		Brown wet very dense fine SAND.
C-9	674.5		
			END OF BORING
			Depth of Boring 50'
			W.L.C. Dry
			W.L.6 Dry

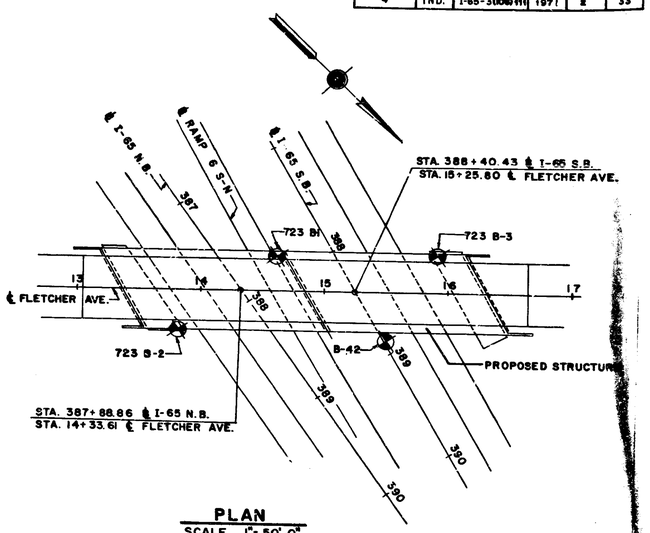

PLAN
SCALE 1"=50'-0"

NOTES:

N = Indicates the number of blows required to drive a 1⅜" I.D., 2" O.D. Split Spoon Sampler 12", or the length given in the Table by means of a 140# Weight falling 30".

See Art. 102.05 of the Specifications Regarding Test Boring Data.

W.L.C. = Denotes Ground Water Table at Completion of drilling hole.

W.L.24 = Denotes Ground Water Table after 24 hours.

TEST BORINGS

INDIANA STATE HIGHWAY COMMISSION


SCALE:- AS NOTED

MARCH 29, 1971

SUBMITTED FOR APPROVAL:- Richard Rolf

PROJECT:- I-65-3(106)111
CONTRACT NO. B-8577
BRIDGE FILE:- I-65-112-5723

BRIDGES OVER 20' SPAN					
FAS ROAD SEC.P.O.	STATE	PROJECT NO.	FISCAL YEAR	SHEET NO.	TOTAL SHEETS
4	IND.	I-65-3 (106)111	1971	3	33

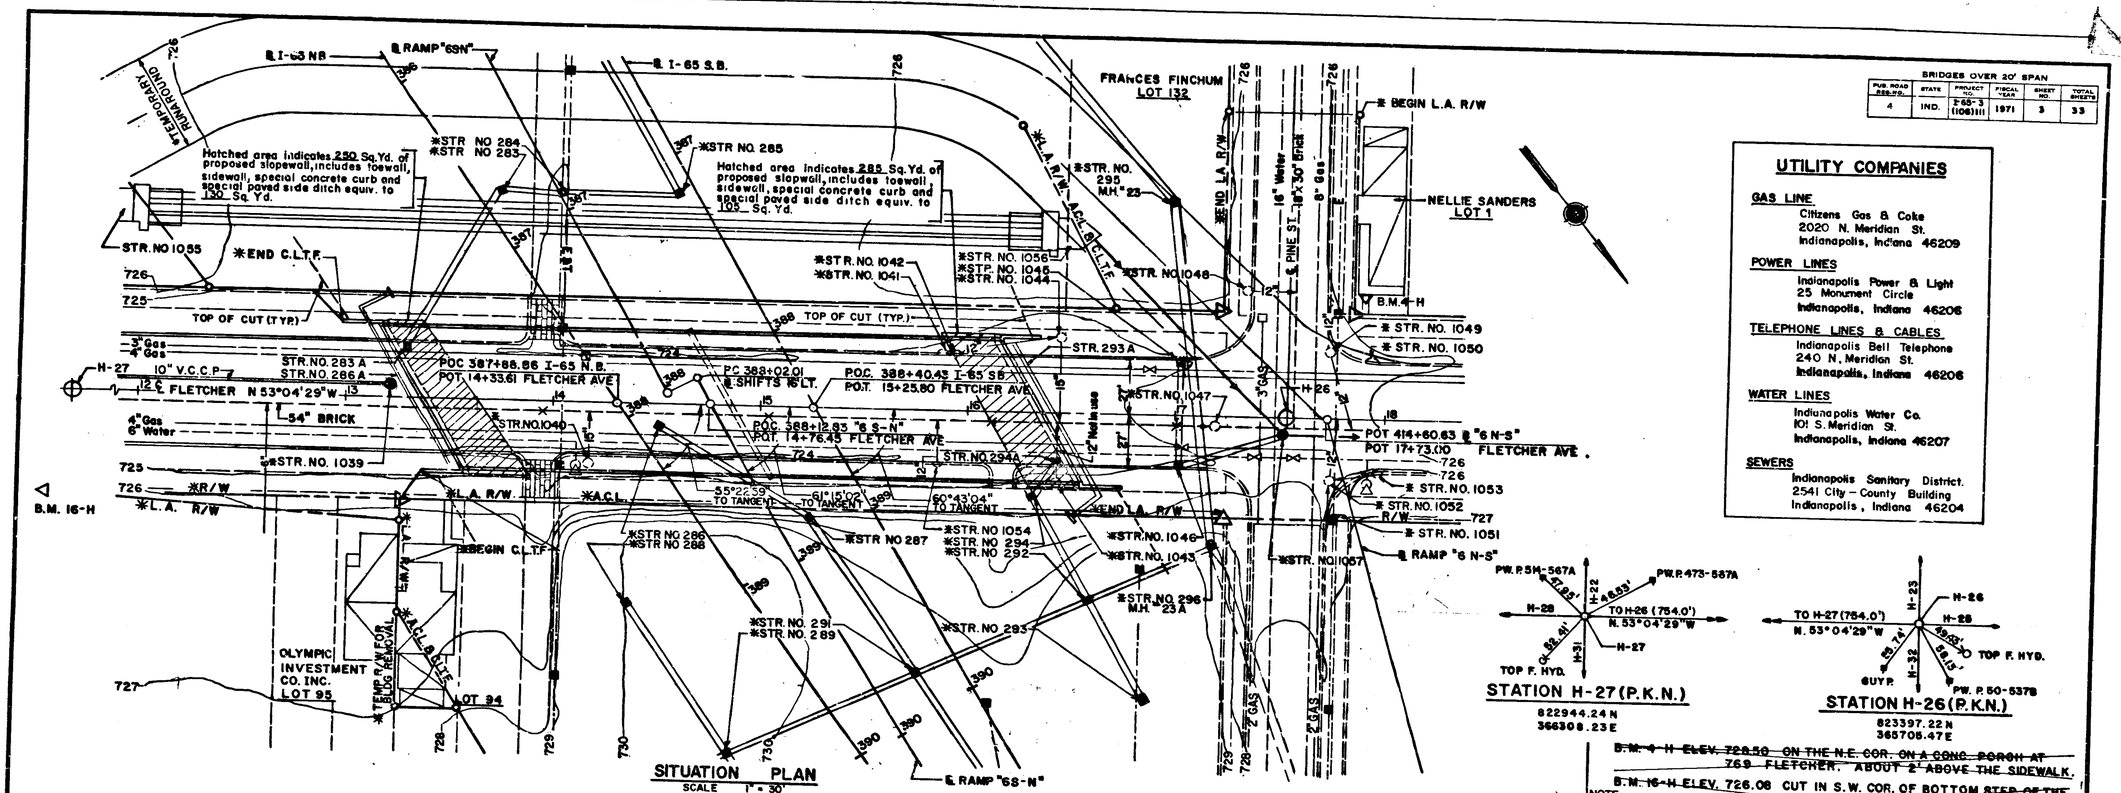

SITUATION PLAN
SCALE 1" = 30'

STATION H-27 (P.K.N.)
822944.24 N
366308.23 E

STATION H-26 (P.K.N.)
823397.22 N
365705.47 E

UTILITY COMPANIES

GAS LINE
Citizens Gas & Coke
2020 N. Meridian St.
Indianapolis, Indiana 46209

POWER LINES
Indianapolis Power & Light
25 Monument Circle
Indianapolis, Indiana 46206

TELEPHONE LINES & CABLES
Indianapolis Bell Telephone
240 N. Meridian St.
Indianapolis, Indiana 46206

WATER LINES
Indianapolis Water Co.
101 S. Meridian St.
Indianapolis, Indiana 46207

SEWERS
Indianapolis Sanitary District.
2541 City – County Building
Indianapolis, Indiana 46204


B.M. 4-H ELEV. 728.50 ON THE N.E. COR. ON A CONC. PORCH AT 769 FLETCHER, ABOUT 2' ABOVE THE SIDEWALK.

B.M. 16-H ELEV. 726.08 CUT IN S.W. COR. OF BOTTOM STEP OF THE CALVARY TABERNACLE ON THE N.E. COR. OF CEDAR AND FLETCHER.

NOTE:
SEE SHEET 37 OF ROAD PLANS FOR BENCH MARKS

CURVE DATA

CURVE 2 I-65 N.B.	CURVE 3 RAMP "6S-N"	CURVE 2 I-65 S.B.
P.I. Sta. 383+56.17	P.I. Sta. 389+39.31	P.I. Sta. 388+09.21
N. 822,771.38	N. 823,355.60	N. 823,218.82
E. 365,949.22	E. 365,945.93	E. 365,932.61
Δ= 5°-30'-52" Lt.	Δ= 5°-34'-18.25 Lt.	Δ= 12°-19'-00" Lt.
D= 0°-30'-00"	D= 2°-00'-00"	D= 0°-40'-00"
R= 11,459.16'	R= 2,864.79'	R= 8,594.37'
L= 1,102.89'	L= 278.587'	L= 1,847.50'
T= 551.87'	T= 139.40'	T= 927.32'
E= 13.26'	E= 3.39'	E= 49.88'

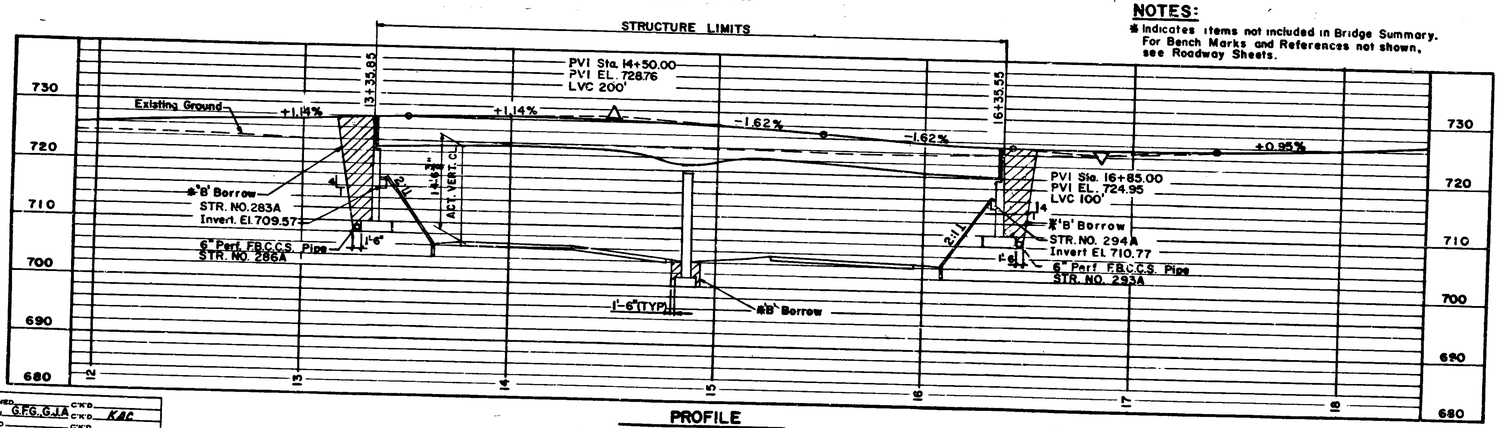

PROFILE
HOR. SCALE 1" = 30' VERT. SCALE 1" = 10'

NOTES:
* Indicates items not included in Bridge Summary. For Bench Marks and References not shown, see Roadway Sheets.

See Article 102.05 of the Specifications regarding test pit data.

REV. 12-16-71 B.M.

LAYOUT
STEEL GIRDER BRIDGE
2 SPANS: @ 147'-0" SKEW: 28° 47' 15" LT.
54'-0" ROADWAY; TWO 6'-0" SIDEWALKS

FLETCHER AVE. OVER I-65 & RAMP 6S-N

INDIANA STATE HIGHWAY COMMISSION
MARION COUNTY

SCALE:- AS NOTED

SUBMITTED FOR APPROVAL:


MARCH 29, 1971

DRAWING:- S1 OF 18
PROJECT:- I-65-3(106)111
CONTRACT NO. B-8877
BRIDGE FILE:- I-65-112-5723

DESIGNED
DRAWN G.F.G. G.J.A. C'K'D
TRACED C'K'D K.R.C.

PROJECT NO.	LINE	SHEET NO.	TOTAL SHEETS	FILE

BRIDGES OVER 20' SPAN					
FED. ROAD SEQ. NO.	STATE	PROJECT NO.	FISCAL YEAR	SHEET NO.	TOTAL SHEETS
4	IND.	I-65-3 (106) III	1971	4	3

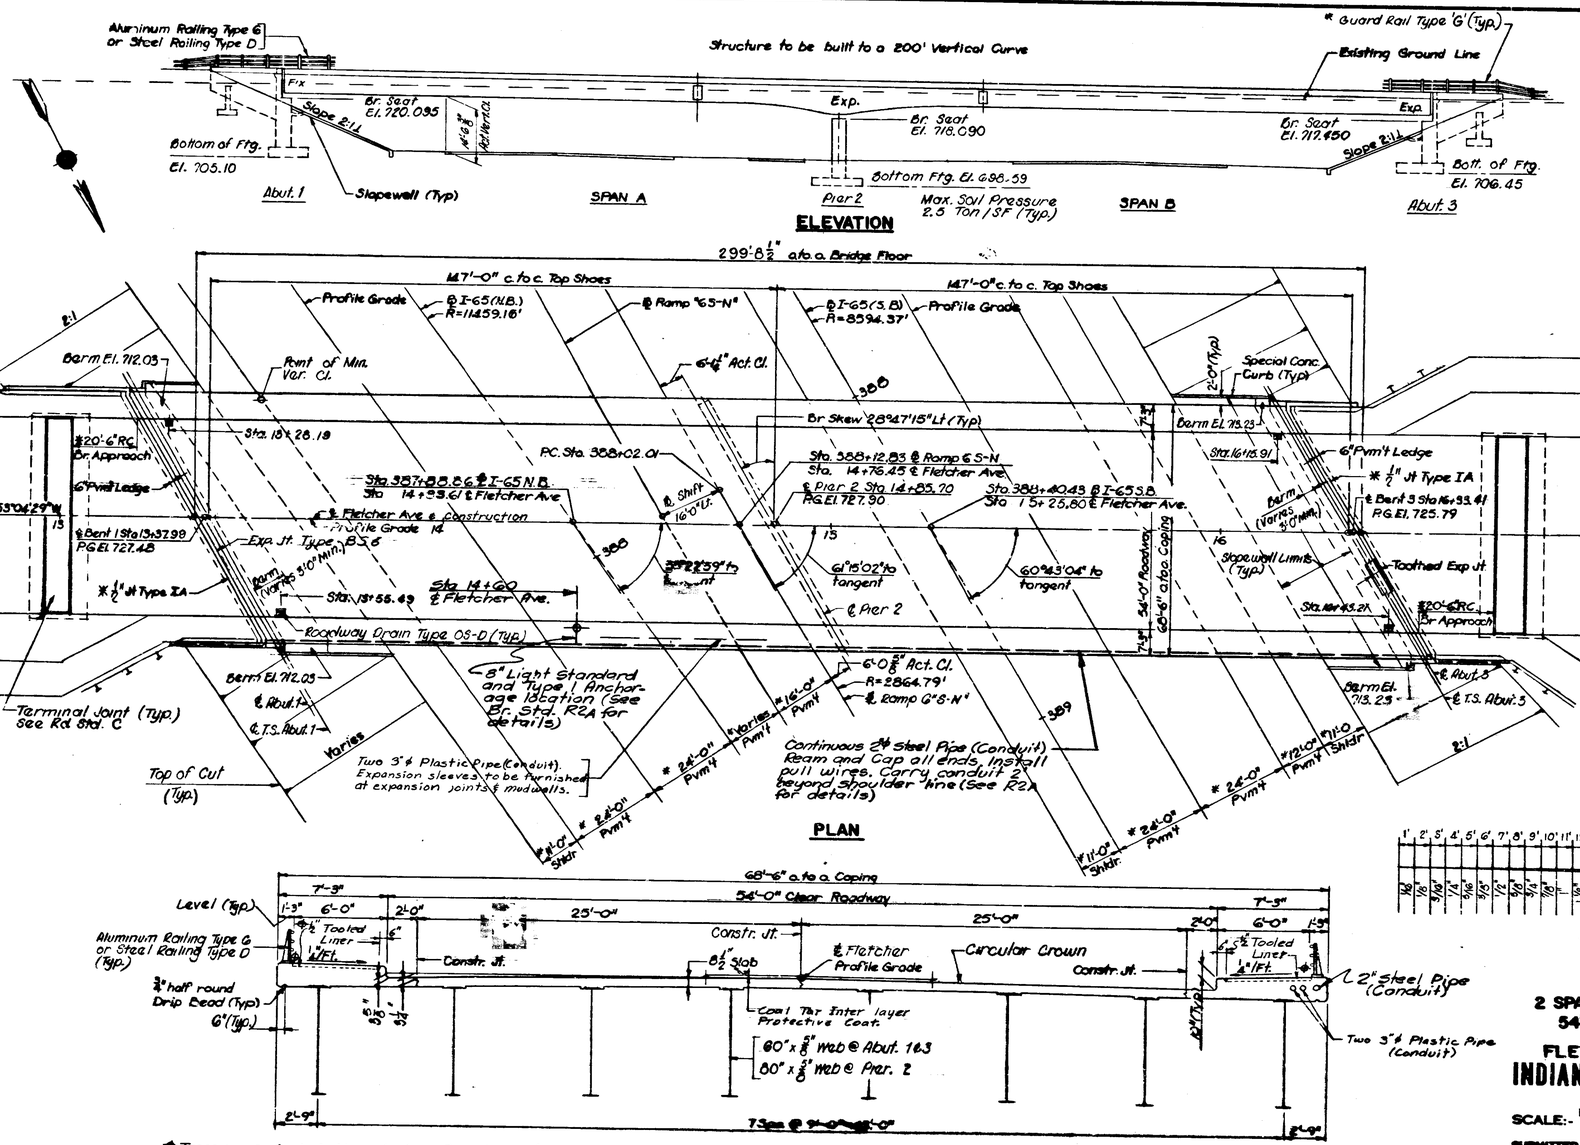

TYPICAL CROSS SECTION OF ROADWAY

Scale: ¼" = 1'-0"

GENERAL NOTES:

No present structure at proposed bridge site.
Depth of footing to be extened if found necessary. See Art. 206-11 (c) of the Specifications.
Reinforcing Steel covering shall be 2 inches in top and 1 inch min. in bottom of floor slabs, 3 inches in footing except bottom steel which shall be 4 inches, and 2 inches in all other parts, unless noted.
Concrete in Abuts and Pier to be Class 'B'
Concrete in superstructure, to be Class 'C'.
Concrete in paved side ditch & slope wall to be Class 'A'
Concrete in structures not noted above to be class 'A'
Continuous concrete pours shall be required between construction joints as shown on detail plans.
Waterproof backs of Abutments and Wingwalls in accordance with Art 702.22 of the Specs.
For future light post installation, see Br. Std. R2A.
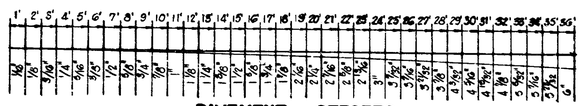
Bevel forms ½" under copings; and chamfer exposed edges 1 inch unless noted.
℄ Standard type OS-D roadway drains to be placed as shown on this drawing.
Construct Slopewall at location shown on layout.
All railing posts to be constructed Perpendicular to grade.
For pay items covering this structure See Bridge Summary
See Special Provisions for items included in this contract.
Only the top of Abut. Caps and front face of mudwalls to be sealed in accordance with Article 702.20 of the specifications.
* Indicates items not included in Bridge Summary.

DESIGN DATA

Designed for HS 20-44 loading in accordance with 1969 AASHO Specifications.

STANDARD DRAWINGS

BR. STD.	RD. STD.	DESCRIPTION
C1 & C3		Standard Miscellaneous Details
D		Roadway Drains
BR1 & BR2		Bridge Railing Type G & Details
BR3 & BR4		Bridge Railing Type D & Details
S1		Typ. Details for Placing 'B' Borrow
	MB 2	Slopewall Curb Details
	MB 4	Slopewall and Drainage Details
	Mc	Type G Casting
	MD	Type D Inlet
R2A		Bridge Lighting Details.



PAVEMENT OFFSETS

GENERAL PLAN
STEEL GIRDER BRIDGE
2 SPANS: @ 147'-0" SKEW: 28°47'15" LT
54'-0" ROADWAY; TWO 6'-0" SIDEWALKS
FLETCHER AVE. OVER I-65 & RAMP 6S-N


INDIANA STATE HIGHWAY COMMISSION
MARION COUNTY

SCALE:- 1/16" = 1'-0" Unless Noted
MARCH 29, 1971
SUBMITTED FOR APPROVAL:
DRAWING:- S2 OF 18
PROJECT:- I-65-3(106)III
CONTRACT NO. B-6877
BRIDGE FILE:- I-65-112-5723

DESIGNED — CH'D
DRAWN GFG GJA CH'K. KAC
TRACED — CH'D

Rev. 8-3-73 Notes, Exp. Jt Type BSS & Cross Section
Rev. 2-23-72 3" ℄ Plastic Pipe (conduit)
Rev 12-16-71 Notes, Std. Drwgs., Steel Pipe (Conduit) 2" ℄ Light Post Anchorage.


Rev. 8-3-73 HMP/GMH

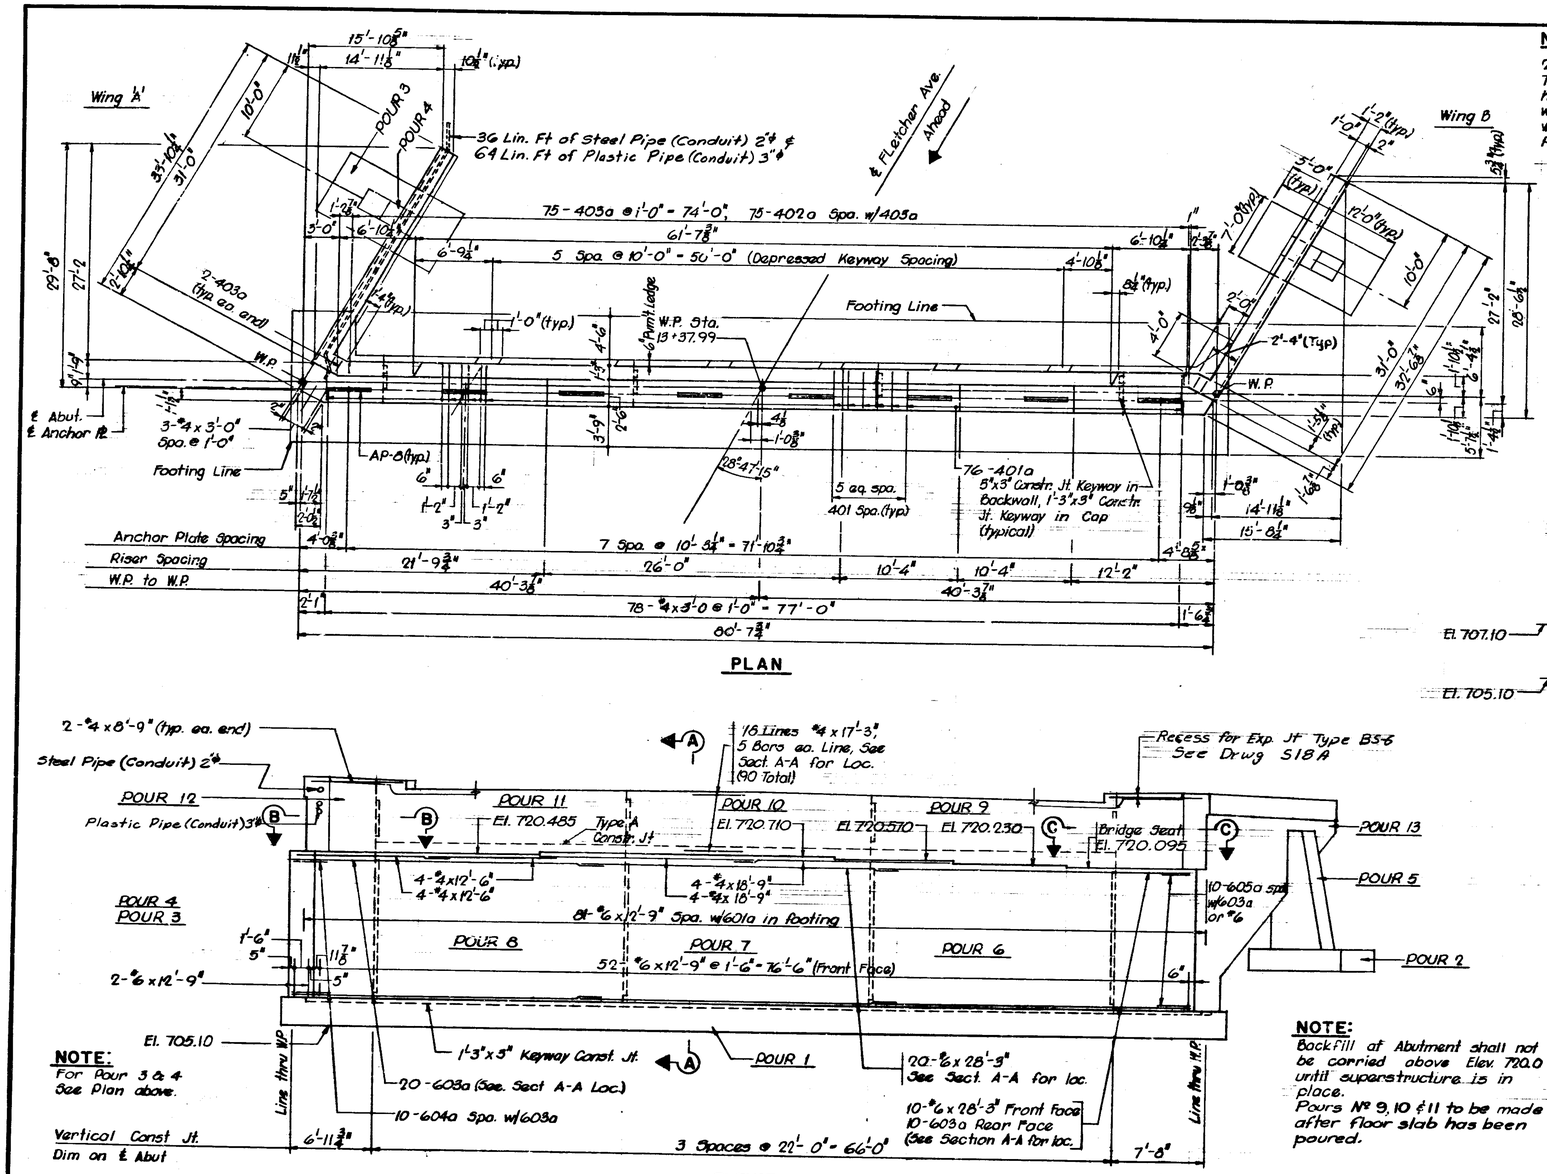

NOTE:
2"x 2'-0" Depressed Keyway Trowel smooth and cover horizontal bearing area with one layer of med. wgt. roofing felt. See Plan for location.

BRIDGES OVER 20' SPAN

PUB. ROAD RSB NO.	STATE	PROJECT NO.	FISCAL YEAR	SHEET NO.	TOTAL SHEETS
4	IND.	I-65-3 (106)111	1971	5	33

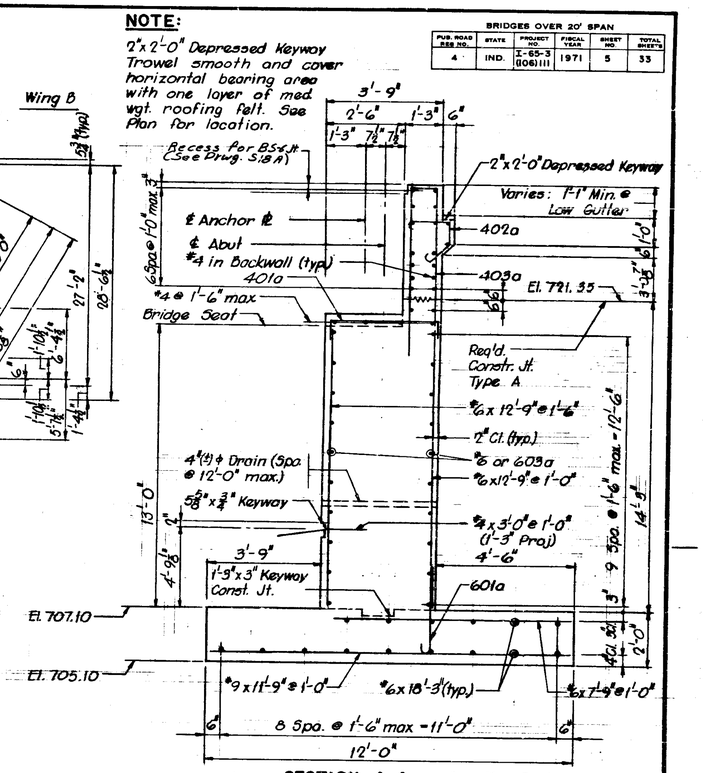

SECTION A-A

Max. Design Soil Pressure 2.5 Tons Per Sq. Ft.

NOTE:
Backfill at Abutment shall not be carried above Elev. 720.0 until superstructure is in place.
Pours Nº 9, 10 & 11 to be made after floor slab has been poured.

NOTES:
See Drawing S-2 for General Notes.
See Bridge Standard C1 for Reinforcing bar Notes.
Anchor Plates MK AP8 shall be preset in concrete.
See Drawing S-4 for Anchor ℔ AP8 details.
See Drawing S-4 for Bill of Materials and Wing Elevations.
Top of Backwall to be constructed to the Roadway crown.
See Bridge Std. C1 for 4"(±) ϕ Drain in End Bent.
For Req'd Constr. Jt. Type A See Br. Std. C-3.
4"(±) ϕ Drain to be included in cost of Concrete.

ABUT. 1

INDIANA STATE HIGHWAY COMMISSION

SCALE:- 3/16" = 1'-0", OR AS NOTED
MARCH 25, 1971
SUBMITTED FOR APPROVAL:
DRAWING:- S3 OF 18
PROJECT:- I-65-3(106)111
CONTRACT NO. B-8877
BRIDGE FILE:- I-65-112-5723


CHAS. W. COLE JR. REGISTERED No. 3653 STATE OF INDIANA PROFESSIONAL ENGINEER

DESIGNED ____ C'K'D ____
DRAWN MC C'K'D KAC
TRACED ____ C'K'D ____


Rev. 8-3-73 Exp. Jt. Type BS6
Rev. 2-23-72 3"ϕ Plastic Pipe (Conduit)
Rev 12-16-71 Notes, 2"ϕ Steel Pipe (Conduit) Added.

Rev. 2-23-72 AWM
Rev. 8-3-73 HRR/CHM


PROJECT NO.	LINE	SHEET NO.	TOTAL SHEETS	FILE

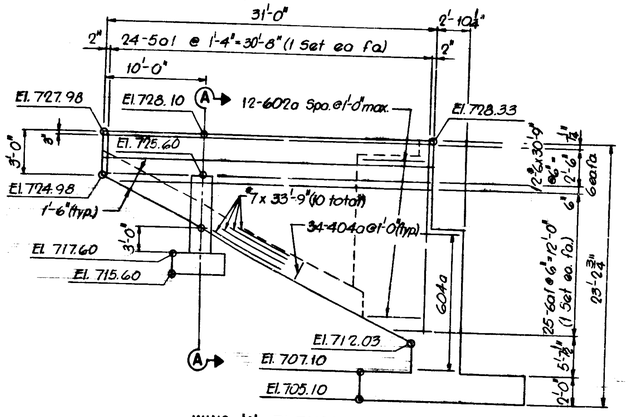

WING 'A' ELEVATION

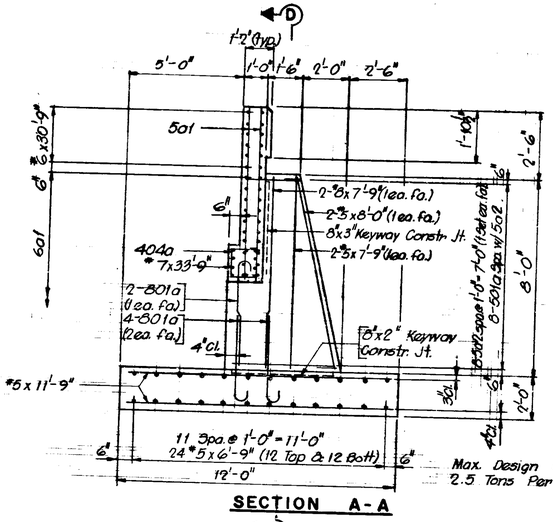

SECTION A-A

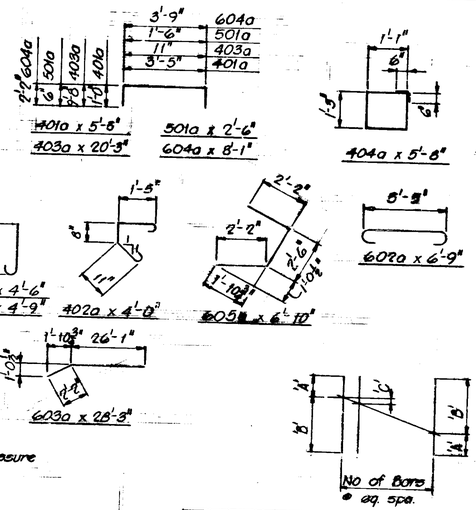

MARK	'A'	'B'	'C'	Length	No. Bars
601	2'-6"	30'-0"	1'-12"	32'-6"	25
501	2'-9"	16'-2"	7"	18'-11"	24
502	2'-2"	4'-6"	4"	6'-8"	8

BRIDGES OVER 20' SPAN

PUB. ROAD REG. NO.	STATE	PROJECT NO.	FISCAL YEAR	SHEET NO.	TOTAL SHEETS
4	IND.	I-65-3 (106) 111	1971	6	33


BILL OF MATERIALS
REINFORCING STEEL

MARK & SIZE	NO. OF BARS	LENGTH	WEIGHT (LBS.)
#9	83	11'-9"	
Total No. 9 Bars			3,316
801a	12	4'-9"	
#8	4	7'-9"	
Total No. 8 Bars			235
#7	20	38'-9"	
Total No. 7 Bars			1,350
601	50	32'-6"	
601a	81	4'-8"	
602a	24	6'-9"	
603a	30	29'-3"	
604a	10	8'-1"	
605a	10	6'-10"	
#6	24	30'-9"	
#6	30	28'-3"	
#6	75	16'-3"	
#6	135	12'-9"	
#6	85	7'-9"	
Total No. 6 Bars			12,717
501a	16	2'-6"	
501	48	18'-11"	
502	16	6'-8"	
#5	28	11'-9"	
#5	4	8'-0"	
#5	4	7'-9"	
#5	48	6'-9"	
Total No. 5 Bars			1,847
401a	76	5'-5"	
402a	75	4'-0"	
403a	79	20'-3"	
404a	68	5'-8"	
#4	8	18'-9"	
#4	90	17'-3"	
#4	8	16'-6"	
#4	4	8'-9"	
#4	81	3'-0"	
Total No. 4 Bars			3,191
Total Reinf. Steel			22,686

CONCRETE QUANTITIES


Class	Conc. in Mtg.	Cu. Yds.
	No. 1	78.3
Total	No. 1 Conc. in Mtg.	78.3
Class of Above Mtg.		Cu. Yds.
Pour No. 2		6.2
Pour No. 3		6.2
Pour No. 4		1.8
Pour No. 5		1.8
Pour No. 6		41.4

CONC. QUANTITIES CONT.	
Pour No. 7	42.2
Pour No. 8	41.9
Pour No. 9	6.6
Pour No. 10	6.9
Pour No. 11	6.9
Pour No. 12	31.5
Pour No. 13	32.7
Total Class B Above Mtg	226.1
MISCELLANEOUS	
Anchor Pl. Mk. AP-8	8 each
Steel Pipe (Conduit) 2"	36 Lin. Ft.
Plastic Pipe (Conduit) 3"	64 Lin. Ft.

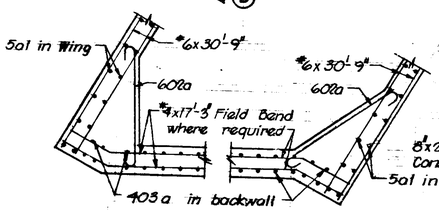


SECTION B-B

SECTION C-C

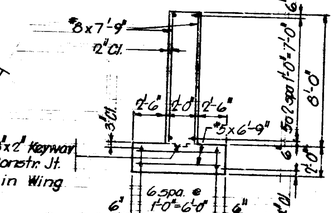


SECTION D-D

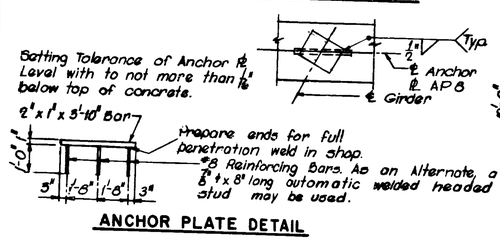

WING 'B' ELEVATION

ANCHOR PLATE DETAIL

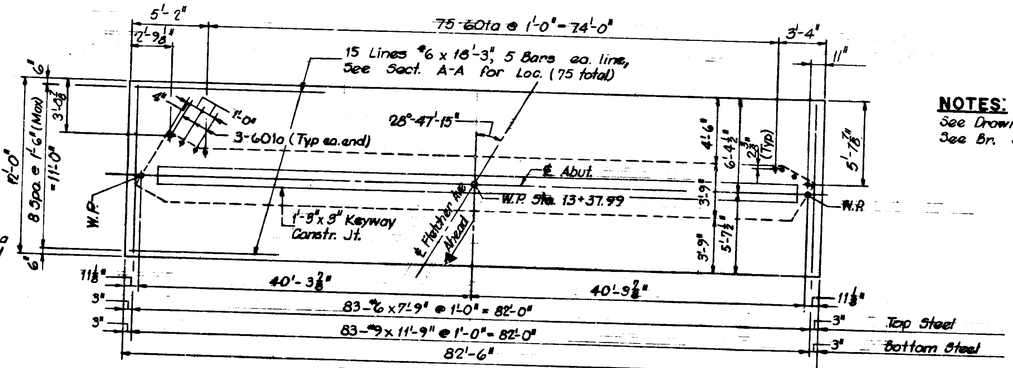

FOOTING PLAN

NOTES:
See Drawing 5-2 for General Notes.
See Br. Std C1 for Reinforcing Bar Notes.

Rev. 8-3-73 Bill of Materials
Rev. 2-23-72 Bill of Materials
Rev. 12-16-71 Bill of Materials.

ABUT. 1 DETAILS

INDIANA STATE HIGHWAY COMMISSION

SCALE: 1/4"=1'-0", OR AS NOTED. MARCH 29, 1971

SUBMITTED FOR APPROVAL: Charles W. Cole

DRAWING:- S4 OF 18
PROJECT:- I-65-3(106)111
CONTRACT NO. B-8877
BRIDGE FILE:- I-65-112-5723

CHARLES W. COLE JR. REGISTERED No. 3683 PROFESSIONAL ENGINEER


DESIGNED ____ C'K'D ____
DRAWN MC C'K'D KAC
TRACED ____ C'K'D ____

PROJECT NO.	LINE	SHEET NO.	TOTAL SHEETS	FILE

R-12-16-71 J.J.W. Chk. A.W.M.
Rev. 2-23-72 AWM
Rev 8-3-73 H.R.P./CMH

BRIDGES OVER 20' SPAN					
PUB. ROAD REF. NO.	STATE	PROJECT NO.	FISCAL YEAR	SHEET NO.	TOTAL SHEETS
4	IND.	I-65-3 (106)111	1971	7	33

R 12-16-71 J.J.W. Chk. A.W.M.
Rev. 2-23-72 AW/M

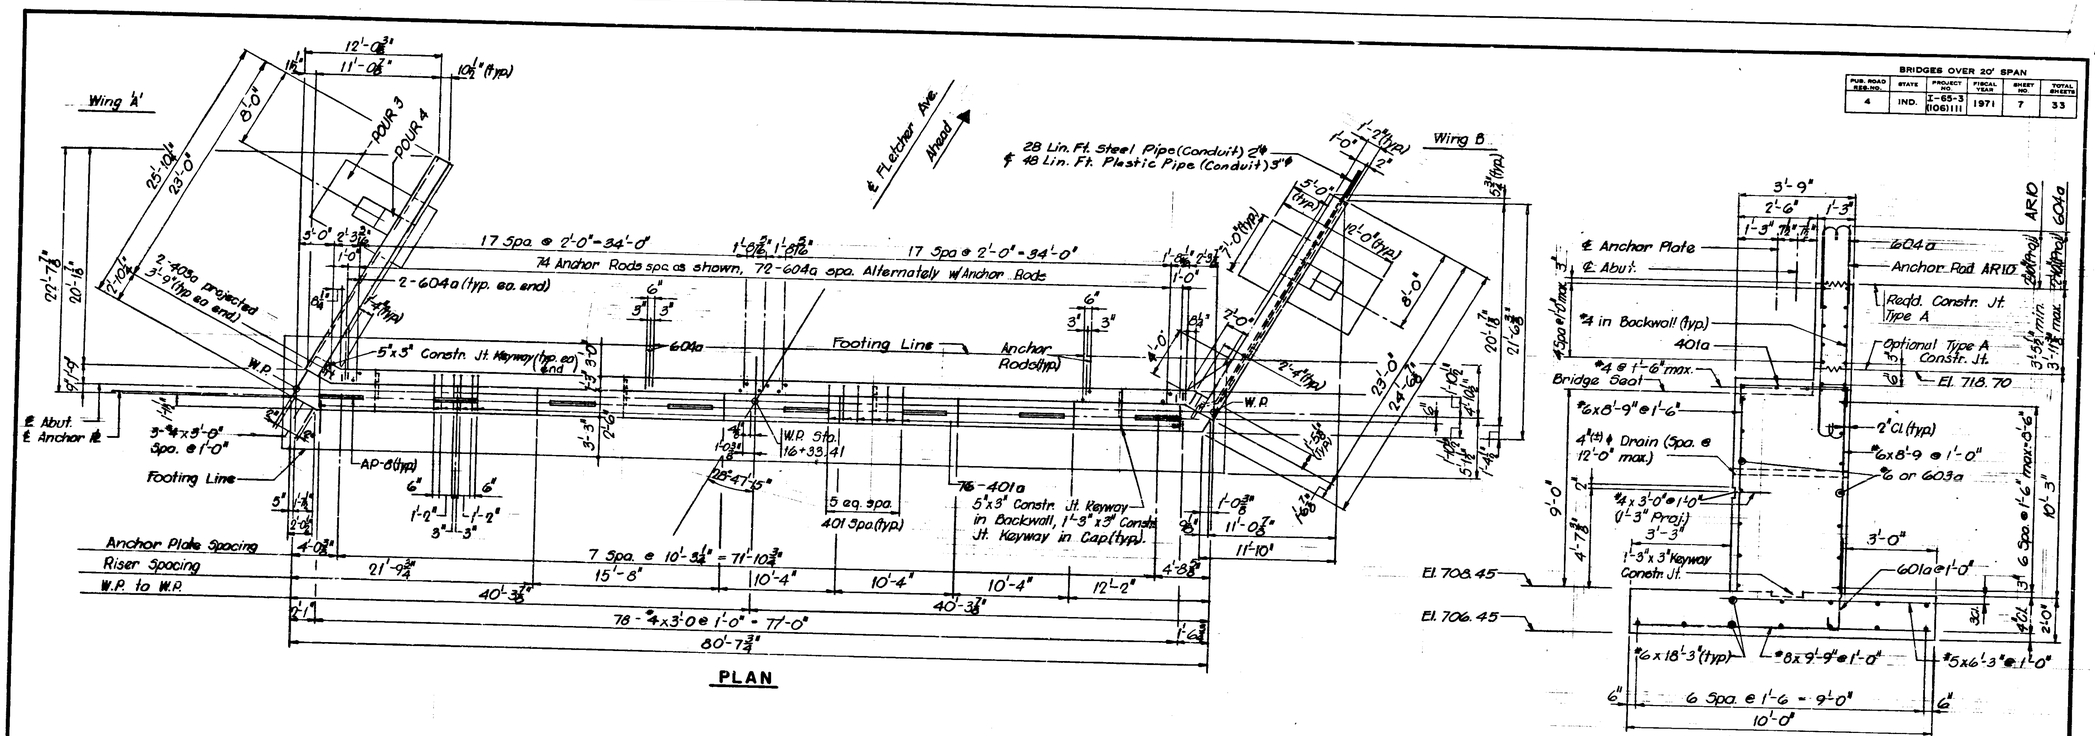

NOTE:
For Pours 3 & 4
See Plan above.

Vertical Const. Jt.
Dim on ℄ Abut

NOTE:
Backfill at Abutment shall not be carried above Elev. 717.00 until superstructure is in place.

NOTES:
See Drawing S-2 for General Notes.
See Bridge Standard C1 for Reinforcing Bar Notes.
Anchor Plates MK APB shall be preset in concrete.
See Drawing S-4 for Anchor ℄ APB details.
See Drawing S-6 for Bill of Materials and Wing Elevations.
Top of Backwall to be constructed to the Roadway crown.
See Bridge Std. C1 for 4"(±) ϕ Drain in End Bent.
For Reqd Constr. Jt. Type A See Br. Std C-3.
4"(±) ϕ Drain to be included in cost of Concrete.

ABUT. 3

INDIANA STATE HIGHWAY COMMISSION

SCALE: 3/16"=1'-0" OR AS NOTED

MARCH 29, 1971


SUBMITTED FOR APPROVAL:


DRAWING: S5 OF 18
PROJECT: I-65-3(106)111
CONTRACT NO. B-8877
BRIDGE FILE: I-65-112-5723


DESIGNED ___ C'K'D ___
DRAWN MC C'K'D KAC
TRACED ___ C'K'D ___


Rev. 8-3-73 AR10 Projection.
Rev. 2-23-72 3"ϕ Plastic Pipe (Conduit)
Rev. 12-16-71 2"ϕ Steel Pipe (Conduit) Added.


PROJECT NO.	LINE	SHEET NO.	TOTAL SHEETS	FILE

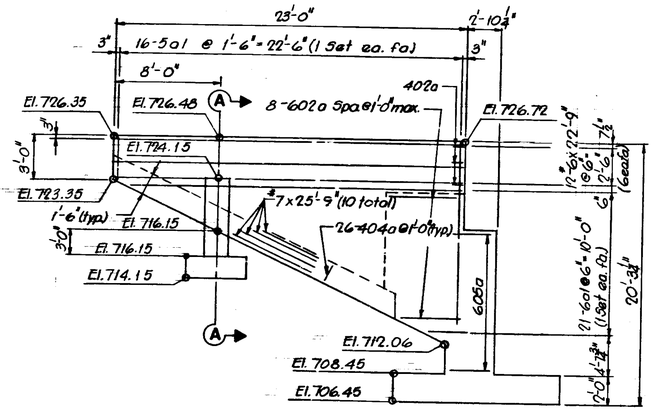


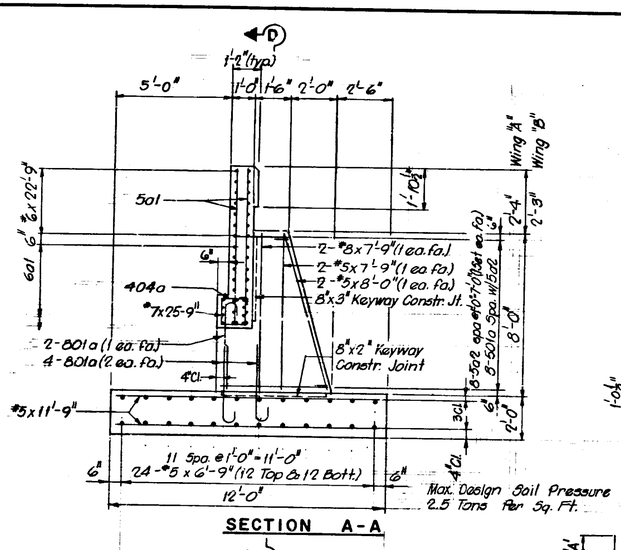

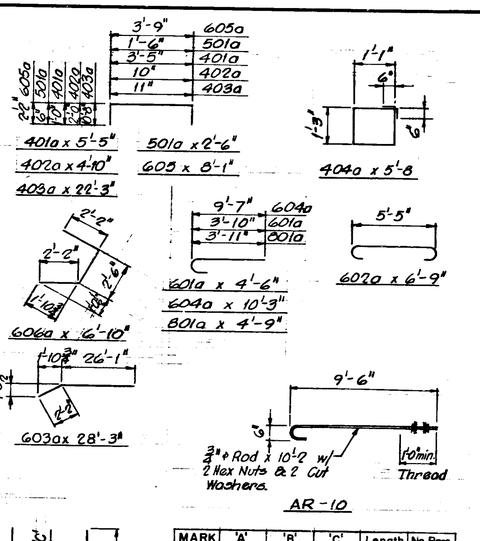

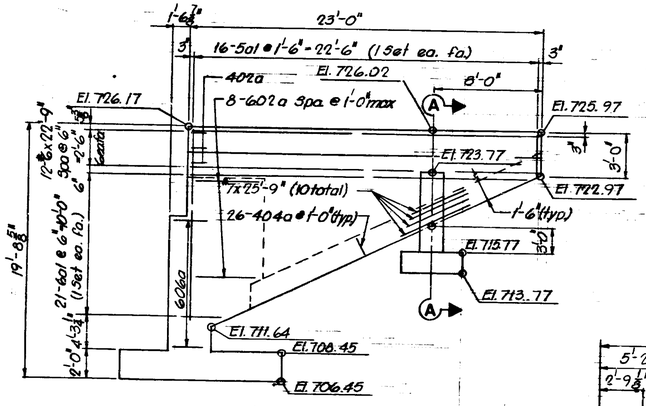

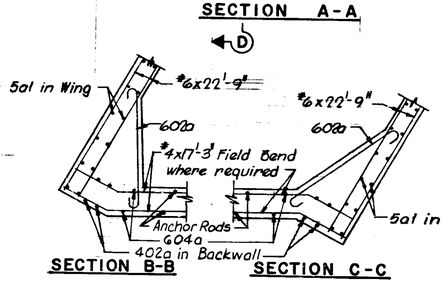


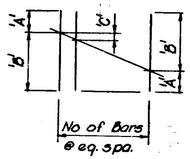


MARK	'A'	'B'	'C'	Length	No. Bars
601	3'-0"	22'-2"	11½"	25'-2"	21
501	2'-9"	14'-0"	9"	16'-9"	16
5a2	2'-2"	4'-6"	4"	6'-8"	8

CONC. QUANTITIES CONT.	
Pour No. 9	3.8
Pour No. 10	3.8
Pour No. 11	3.8
Pour No. 12	21.3
Pour No 13	22.1
Total Class B Above Ftg.	160.4

MISCELLANEOUS	
Anchor Rd. MK. AP-8	8 each
Anchor Rods MK. AR-10	74 each
Steel Pipe (Conduit) 2" ø	28 Lin. Ft.
Plastic Pipe (Conduit) 3" ø	48 Lin. Ft.

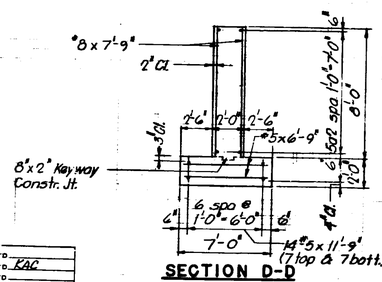

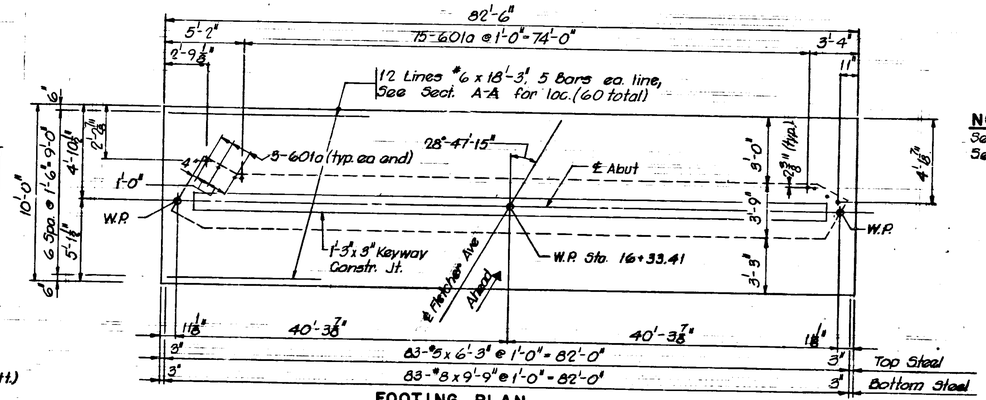

Rev 2-23-72 Bill of Materials
Rev. 12-16-71 Bill of Materials.

NOTES:
See Drawing 3-2 for General Notes.
See Brd Std C1 for Reinforcing Bar Notes.

BRIDGES OVER 20' SPAN					
PUB. ROAD SER. NO.	STATE	PROJECT NO.	FISCAL YEAR	SHEET NO.	TOTAL SHEETS
4	IND.	I-65-3 (106) III	1971	8	33

BILL OF MATERIALS
REINFORCING STEEL

MARK & SIZE	NO. OF BARS	LENGTH	WEIGHT (LBS)
801a	12	4'-9"	
#8	83	9'-9"	
#8	4	7'-9"	
Total No. 8 Bars			2396
#7	20	25'-9"	
Total No. 7 Bars			1053
601	42	25'-2"	
601a	81	4'-6"	
602a	16	6'-9"	
603a	21	28'-3"	
604a	76	10'-3"	
605a	7	8'-1"	
606a	7	6'-10"	
#6	21	28'-3"	
#6	24	22'-9"	
#6	60	18'-3"	
#6	135	8'-9"	
Total No. 6 Bars			9648
5a1	32	16'-9"	
5a2	16	6'-8"	
501a	16	2'-6"	
#5	28	11'-9"	
#5	4	8'-0"	
#5	4	7'-9"	
#5	48	6'-9"	
#5	83	6'-3"	
Total No. 5 Bars			2,000
401a	76	5'-5"	
402a	6	4'-10"	
403a	4	22'-3"	
404a	52	5'-8"	
#4	60	17'-3"	
#4	4	15'-6"	
#4	8	10'-6"	
#4	8	11'-3"	
Total No. 4 Bars			1,413
Total Reinf. Steel			16,507

CONCRETE QUANTITIES

Class B Conc. in Ftg.	Cu. Yds.
Pour NO. 1	61.1
Total Class B Conc. in Ftg.	61.1
Class B Conc. Above Ftg.	Cu. Yds.
Pour No. 2	6.2
Pour No. 3	6.2
Pour No. 4	1.8
Pour No. 5	1.8
Pour No. 6	29.3
Pour No. 7	30.1
Pour No. 8	30.0

ABUT. 3 DETAILS


INDIANA STATE HIGHWAY COMMISSION

SCALE:- 1/4" = 1'-0", OR AS NOTED
SUBMITTED FOR APPROVAL:
MARCH 29, 1971
DRAWING:- S6 OF 18
PROJECT:- I-65-3(106)111
CONTRACT NO. B-8877
BRIDGE FILE:- I-65-112-5723

DESIGNED
DRAWN MK C'K'D KAC
TRACED C'K'D

PROJECT NO.	LINE	SHEET NO.	TOTAL SHEETS	FILE

R. 12-16-71 J.J.W. Chk. A.W.M.
Rev. 2-23-72 A.W.M.

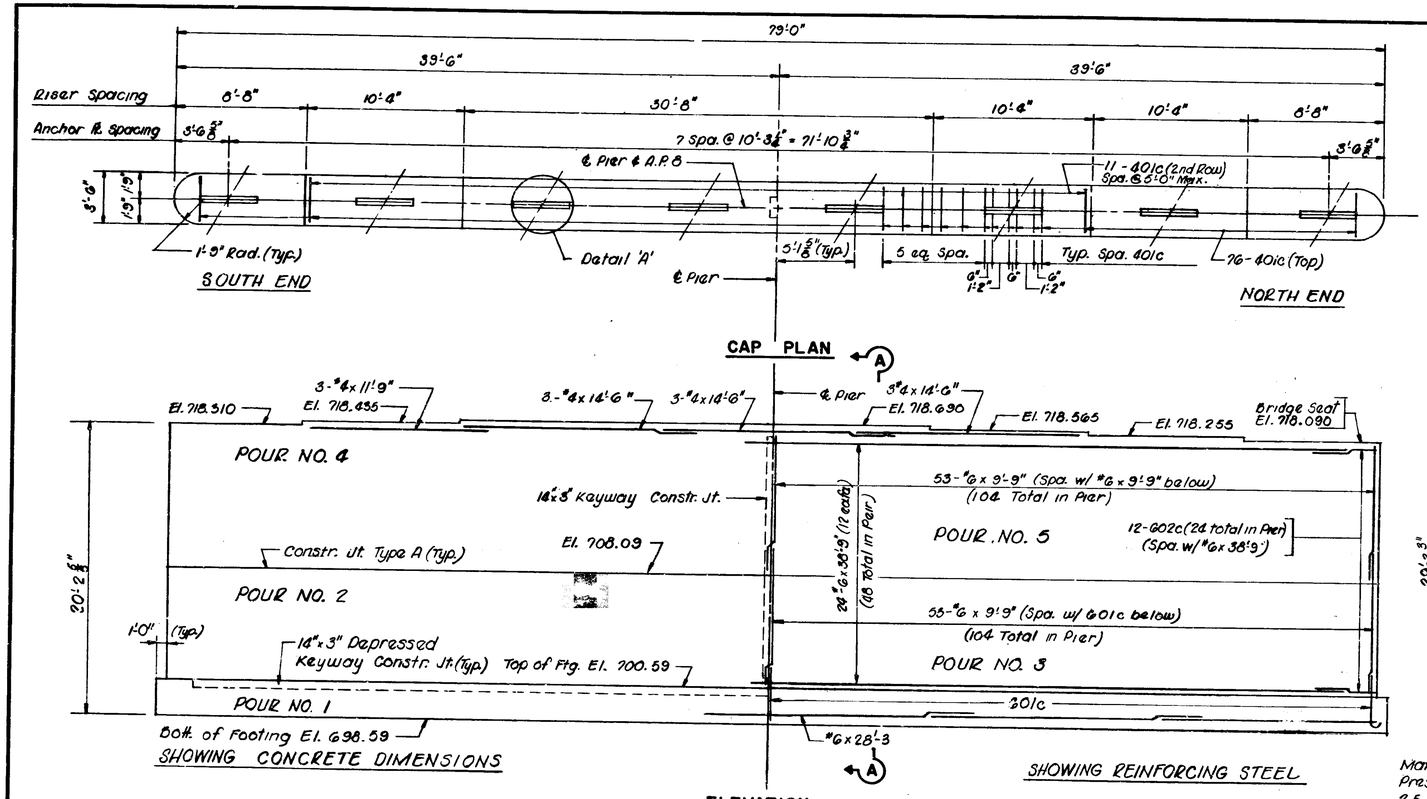

NOTES:

See Dwg S 2 for General Notes
See Dwg S 4 for Detail "A"
See Bridge Std. C 1 for Reinforcing Bar Notes.
See Dwg. S 18 for Constr. Jt. Type A Detail.

BRIDGES OVER 20' SPAN					
FED. ROAD REQ. NO.	STATE	PROJECT NO.	FISCAL YEAR	SHEET NO.	TOTAL SHEETS
4	D.	I-65-3 (106) III	1971	9	33

BILL OF MATERIALS

REINFORCING STEEL

MARK OR SIZE	NO. REQ'D	LENGTH	WEIGHT (LBS)
#10	107	12'-6"	
Total #10 Bars			5,755
G01c	104	5'-0"	
G02c	24	9'-6"	
#6	48	38'-9"	
#6	27	28'-3"	
#6	208	9'-9"	
Total #6 Bars			8,109
401c	87	5'-2"	
#6	9	14'-6"	
#6	3	11'-9"	
Total #4 Bars			111
Total Reinf. Steel			13,975

CONCRETE QUANTITIES

Class 'B' above Footing	Cu. Yd.
Pour No. 2	38.1
Pour No. 3	38.1
Pour No. 4	53.8
Pour No. 5	53.0
Total above Footing	183.0
Class 'B' in Footing	
Pour No. 1	78.0
Total in Footing	78.0

MISCELLANEOS

Anchor R. MK AP8	8 ea.

PIER 2

INDIANA STATE HIGHWAY COMMISSION

SCALE:- 1/4" = 1'-0" MARCH 29, 1971


SUBMITTED FOR APPROVAL:

DRAWING:- 37 OF 18
PROJECT:- I - 65 - 3 (106) III
CONTRACT NO. B-8877
BRIDGE FILE:- I - 65 - 112 - 5723

DESIGNED ____ C'K'D ____
DRAWN GJA C'K'D KAC
TRACED ____ C'K'D ____

Rev. 3-23-72 Bar Size

PROJECT NO.	LINE	SHEET NO.	TOTAL SHEETS	FILE

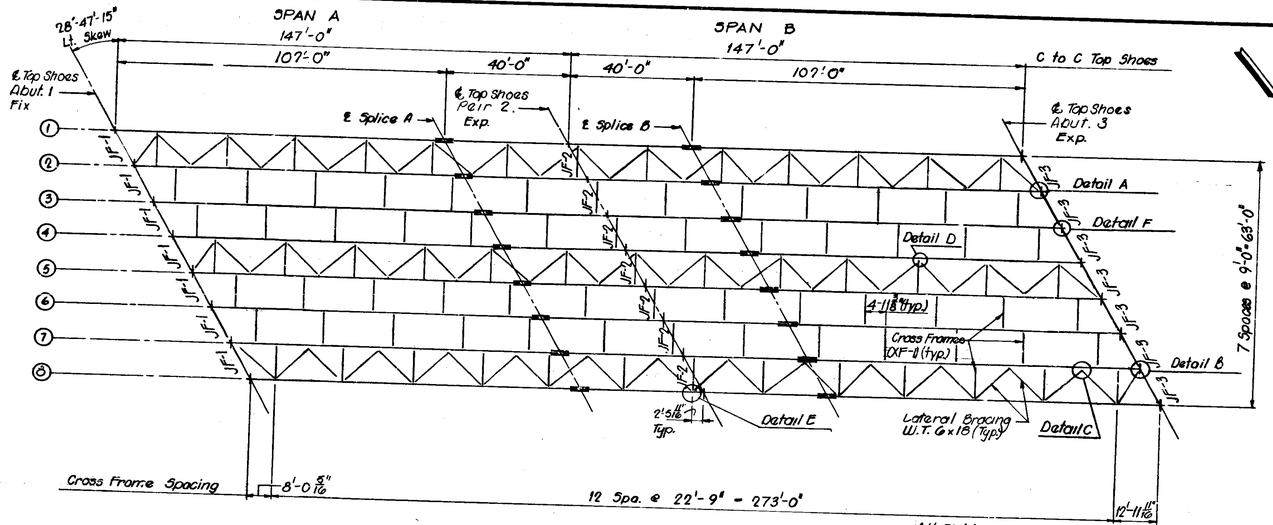

FRAMING PLAN
Scale: 1" = 15'

SHOE TABLE								
	GRD. 1	GRD. 2	GRD. 3	GRD. 4	GRD. 5	GRD. 6	GRD. 7	GRD. 8
ABUT. 1	FS1	FS2	FS3	FS3	FS3	FS3	FS2	FS1
PIER 2	ES1	ES2	ES3	ES3	ES3	ES3	ES2	ES1
ABUT.3	ES4	ES5	ES6	ES6	ES6	ES6	ES5	ES4

NOTE:

Materials as listed on the shop drawings which do not require mill test reports may be changed from that shown on the contract plans subject to approval. The material specification shall be given on the shop drawings if different than that on contract plans. See Art. 711.07 of the Specifications.

STRUCTURAL STEEL NOTES:

High Strength bolts ⅞" unless noted; Open Holes 15/16" Unless noted
All paint shall be in accordance with current State Highway Specifications: (Shop Point & Field Paint) Basic Lead Silico Chromate.
All Structural Steel shall conform to ASTM A-36 unless otherwise noted.

All butt welds shall be subject to radio-graphic inspection at the option of the Engineer.
The Contractor shall prepare detailed working or shop drawings to enable him to fabricate, erect, and construct all parts of the work in conformity with the Engineer's drawings and specifications and shall submit five (5) copies to the Engineer. See Article 711.04 of the Specifications.
The shop details shall show a plan of matchmarking for all reamed pieces.
All splice plates to be removed, cleaned, and deburred after reaming. Splice plates shall not extend beyond the end of girder after bolting for shipment.

Rev. 12-16-71 Notes Rev. 12-29-72 Notes

All field splices are optional (except as noted) subject to "Regulations pertaining to the movement of over length concrete and steel beams on State Highways" as stated in Supplement #2 to General Letter #19-71 dated Aug. 19, 1971. Shop plans shall indicate which splices the contractor intends to eliminate and also means of transportation, whether by rail or over State highways.
The shop plans shall indicate whether reaming or drilling is to be done in shop or field. If shop reaming or drilling is used the girders shall be assembled in accordance with no load camber and reaming diagram. If the girders are shop reamed or drilled, full size drift pins shall be used in erection.
Structural steel for welding may be flame cut if the flame cutting is mechanically guided. Hand flame cutting shall be used only when approved, and the surface is further treated by milling, grinding, or chipping and grinding.
All shop butt welds in flange plates shall be ground smooth and flush with the base metal on all surfaces. This shall apply to both parts of equal thickness and unequal thickness. Grinding shall be done in the direction of stress and in such a manner that the metal is kept below the blue brittle range. Any defects exposed by the grinding shall be cleaned, filled with weld metal, and reground to a uniform finish.
Girders must be cambered to a smooth curve. Camber must be checked after shop welding is completed and while girders are supported in such a way as to have no bending moment in the direction of camber.
Sheared plates or universal mill plates shall be used for girder webs, and shall be ordered with sufficient additional width to allow for trimming of edges to provide built-in camber for deadload deflection and vertical curve. Trimming shall be by flame cutting. The faying surfaces of the web and flange plates and the adjacent surfaces that are to be fillet welded shall be cleaned by grinding prior to assembly and welding of web to flange.
When the girder sections are fit up in the shop for reaming or drilling of field splices, the centerlines of opposing flanges shall not deviate more than ⅛ inch with the webs in alignment.
Holes for girder splices, and splice plates shall be subpunched or subdrilled and reamed to size while assembled. See Article 711.24 of the Specifications. Flange splice bars shall have planed or rolled edges and holes in bars shall be subdrilled and reamed or drilled full size while assembled.

Rev. 8-3-73 Notes

BRIDGES OVER 20' SPAN					
FED. ROAD DESIGN NO.	STATE	PROJECT NO.	FISCAL YEAR	SHEET NO.	TOTAL SHEETS
4	IND.	I-65-3 (106) 111	1971	10	33

Diameter of holes in all material connecting top shoes to girder flanges to be 1" ϕ. Bolts connecting girder flange to top shoe shall extend into top shoe a minimum of 1 inch.
Shims between girders and top shoes may be built up. No shim shall be less than ⅛" thickness.
Structural steel shall be erected using sufficient full size drift pins to permit placement of bolts without damage thereto and to facilitate setting splices to grade. At the time of erection not less than 50 percent of the holes in any connection shall be filled with bolts. The bolts shall not be tightened more than snug tight at this stage. Any drifting required shall be only such that will draw the parts into position but not sufficient to enlarge the holes or distort the metal. Unfair holes shall be reamed or drilled.
Rivets shall not be used in the assembly of structural steel.
As soon as the Engineer has approved the field welds, all welds and any surface from which the shop coat has been omitted or becomes worn off or has otherwise become defective shall be thoroughly cleaned of all charred paint or any foreign matter and completely covered with one coat of shop paint.
The weight of high strength bolts is not included in the estimated weight of structural steel. The cost of these bolts shall be included in the cost of structural steel.

Estimated weight of structural steel:------ 4254.200 lbs.
This includes, A-36 ---------- 1,233,600 lbs.
A-514 ---------- 7,700 lbs.
A-36 (Toothed Exp. Jt.)----- 12,900 lbs.
Weight of Bronze plates---------- 948 lbs.

DESIGN DATA:

Live Loads: H.S. 20-44 loading in accordance with 1969 A.A.S.H.O. Specifications.
Dead Loads: Actual weight plus 35 pounds per square foot of roadway to provide for future wearing surface.
Slab: Designed for 16,000 pound wheel plus impact and with 1" monolithic wearing surface.
Allowable Stresses: To be in accordance with 1969 AASHO Specifications.

NOTES:

See Dwg. S2 for General Notes
See Dwg. S9 and S10 for Girder Elevation & Splices
See Dwg. S11 for Detail A, B, C, D, E, F and other Misc. Details
See Dwg S12 and S13 for Shoe Details
See Dwg. S14 and S15 for Toothed Expansion Joint Details

FRAMING PLAN

INDIANA STATE HIGHWAY COMMISSION

SCALE:- AS NOTED
SUBMITTED FOR APPROVAL:
MARCH 29, 1971
DRAWING:- S 8 OF 18
PROJECT:- I-65-3(106)111
CONTRACT NO. B-9877
BRIDGE FILE:- I-65-112-5723


CHAS. W. COX JR. REGISTERED No. 3883 STATE OF INDIANA PROFESSIONAL ENGINEER

DESIGNED ____ C'K'D ____
DRAWN MC G.I.A C'K'D KAC
TRACED ____ C'K'D ____

PROJECT NO.	LOAD	SHEET NO.	TOTAL SHEETS	FILE


Rev. 12-16-71 J.J.W. CHK. A.W.M.
Rev 8-3-73 H.R.B./CHM

BRIDGES OVER 20' SPAN					
FED. ROAD SEQ. NO.	STATE	PROJECT NO.	FISCAL YEAR	SHEET NO.	TOTAL SHEETS
4	IND.	I-65-3 (006) 111	1971	11	33

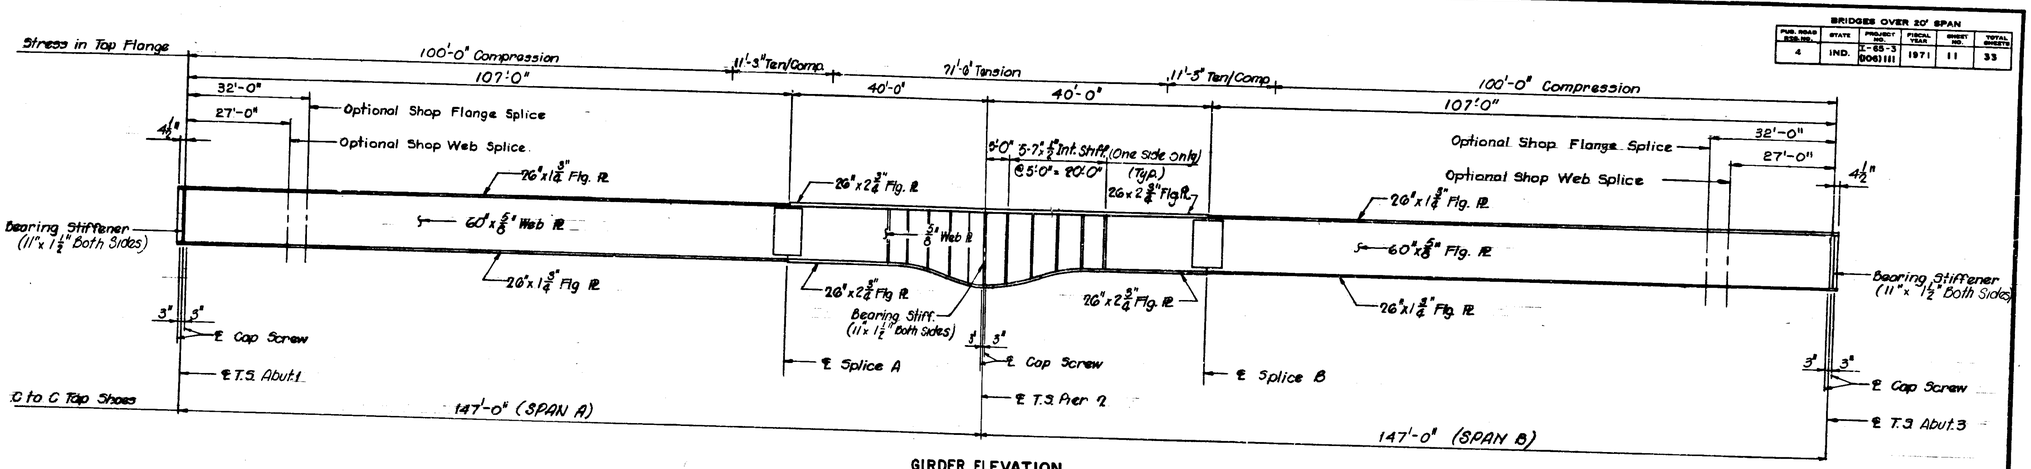


GIRDER ELEVATION

GIRDER 1 & 8

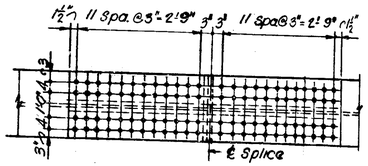

TOP VIEW

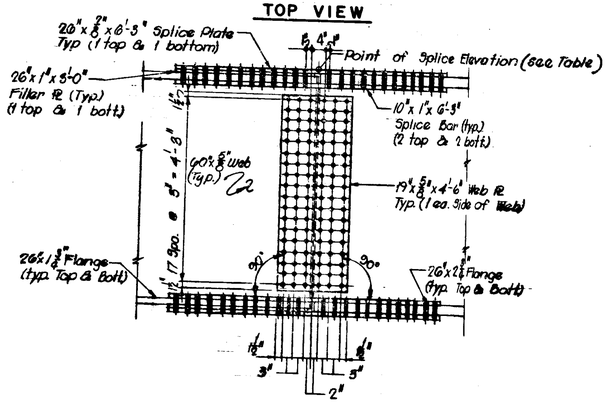

ELEVATION

(A & B)

TABLE OF TOP OF SPLICE ELEVATIONS		
	SPLICE A	SPLICE B
GIRDER 1	727.265	726.870
GIRDER 2	727.280	726.830
GIRDER 3	727.390	726.880
GIRDER 4	727.470	726.910
GIRDER 5	727.460	726.845
GIRDER 6	727.360	726.690
GIRDER 7	727.235	726.515
GIRDER 8	727.200	726.425

NOTE:
Splice elevations are with falsework removed and carrying steel deadload only. Top of Girder Splice plates shall be adjusted to the above elevations before bolting field splice.

NOTES:
See Dwg. S-2 for General Notes & Framing Plan.
See Dwg. S-8 for Structural Steel Notes & Framing Plan.
See Dwg. S 10, S 11, S 12 [illegible], S 14 and S 15 for other Steel Details

DESIGNED ____ C'K'D ____
DRAWN MW GJA C'K'D KRC
TRACED ____ C'K'D ____

STEEL DETAILS (GIRDER 1 & 8)

INDIANA STATE HIGHWAY COMMISSION

SCALE:- AS NOTED


SUBMITTED FOR APPROVAL:- [signature] MARCH 29, 1971

DRAWING:- S9 OF 18
PROJECT:- I-65-3(106)111
CONTRACT NO. B-8877
BRIDGE FILE:- I-65-112-5723


Rev. 3-23-72 Gage on Splice

PROJECT NO.	LINE	SHEET NO.	STATE	FILE


BRIDGES OVER 20' SPAN					
FHS. ROAD SEC. NO.	STATE	PROJECT NO.	FISCAL YEAR	SHEET NO.	TOTAL SHEETS
4	IND.	I-65-3 (106)111	1971	12	53

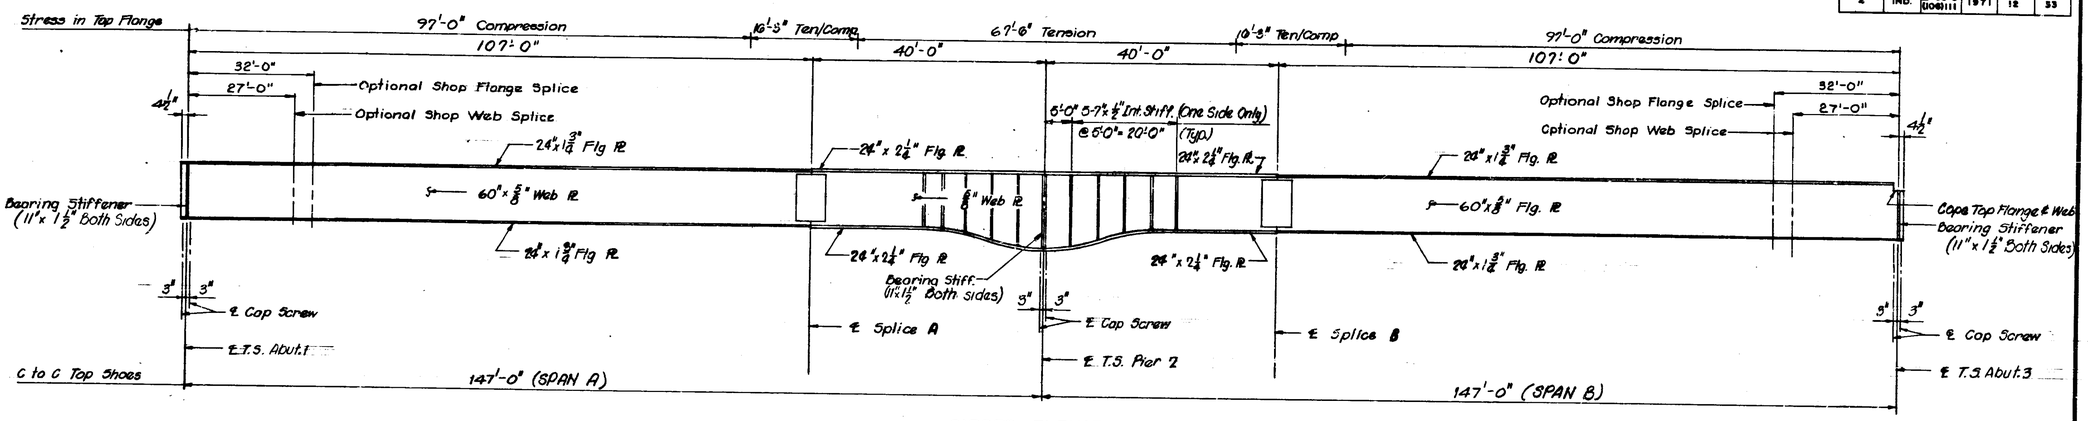


GIRDER ELEVATION
GIRDER 2, 3, 4, 5, 6, & 7

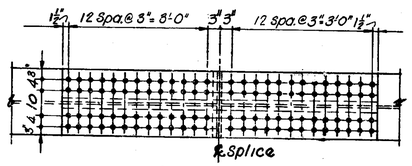

TOP VIEW

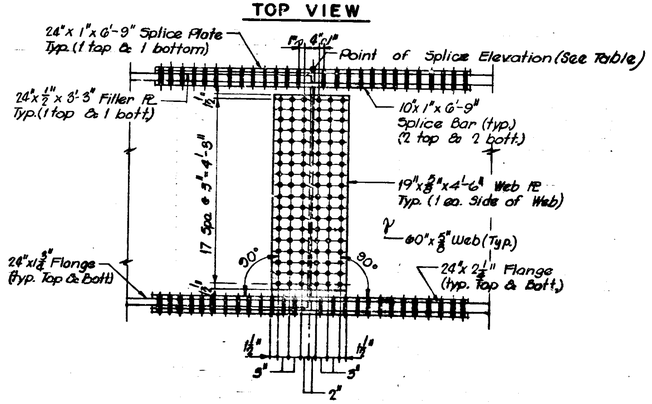

ELEVATION
(A & B)

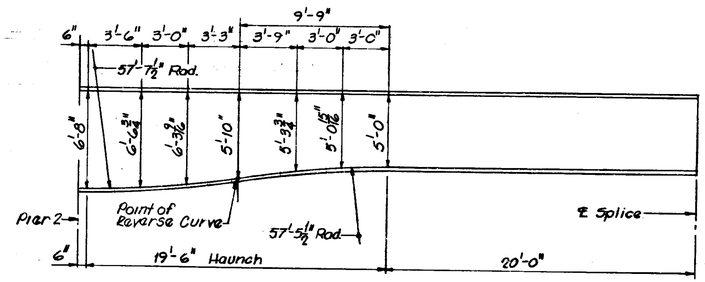

TYPICAL HAUNCH DETAIL
Scale: ¼"=1'-0"

NOTES:

See Dwg. S2 for General Notes.
See Dwg. S8 for Structural Steel Notes and Framing Plan
See Dwg. S9 for Table of Top of Splice Elevations.
See Dwg. S9, S11, S12, S13, S14 and S15 for other Steel Details

STEEL DETAILS (GIRDER 2 THRU 7)

INDIANA STATE HIGHWAY COMMISSION

SCALE:- AS NOTED

MARCH 29, 1971

SUBMITTED FOR APPROVAL:

DRAWING:- S10 OF 18
PROJECT:-I-65-3(106) 111
CONTRACT NO. B-8877
BRIDGE FILE:-I-65-112-5723


CHIEF ENGINEER No. 3660 STATE OF INDIANA REGISTERED PROFESSIONAL ENGINEER

DESIGNED _____ C'K'D _____
DRAWN MC & JA C'K'D KRC
TRACED _____ C'K'D _____

Rev. 3-28-72 Splice Gage


PROJECT NO.	LINE	SHEET NO.	TOTAL SHEETS	FILE

BRIDGES OVER 20' SPAN					
PUB. ROAD SER. NO.	STATE	PROJECT NO.	FISCAL YEAR	SHEET NO.	TOTAL SHEETS
4	IND.	I-65-3 (106)111	1971	13	33

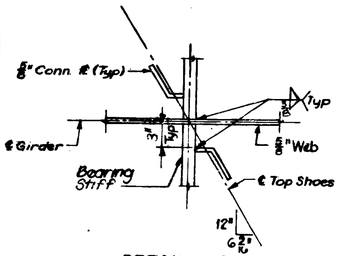


DETAIL F


NOTE:
Weld ⅝" Conn. Pl to Br. Stiffener before welding Br Stiffener to Girder Web.

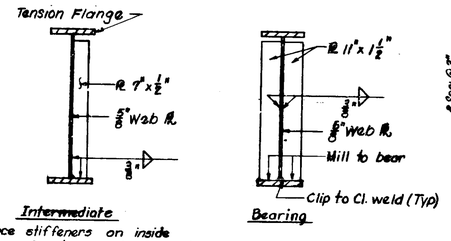


STIFFENER DETAILS

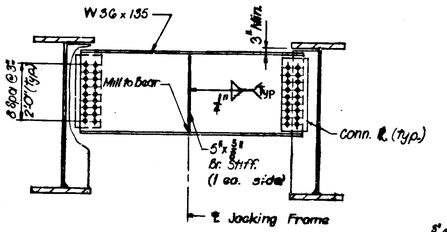


JACKING FRAME JF-1
Scale: ½"=1'-0"

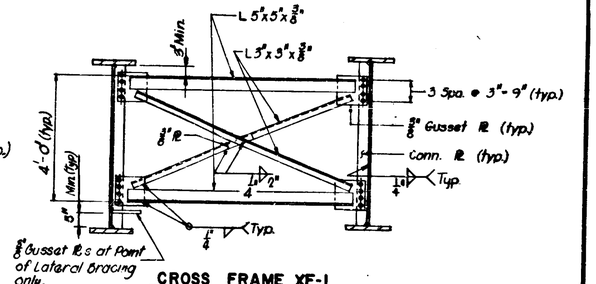


CROSS FRAME XF-1
Scale: ½"=1'-0"

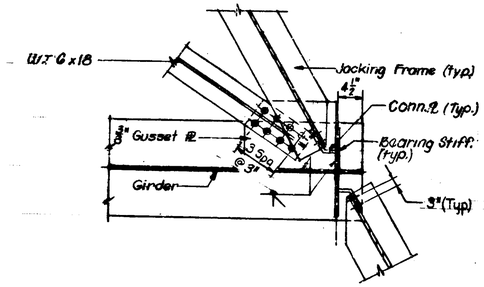


DETAIL A

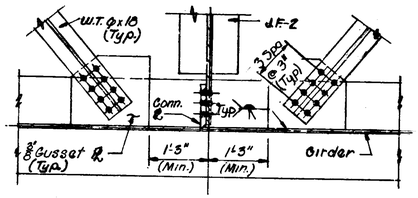


DETAIL E

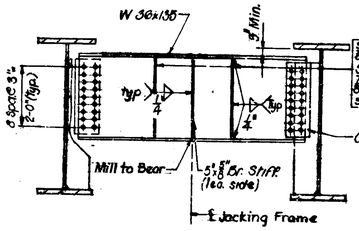


JACKING FRAME JF-3
Scale: ½"=1'-0"

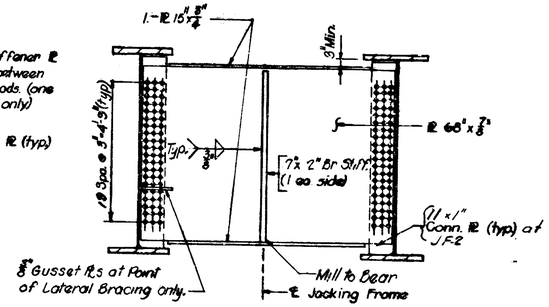


JACKING FRAME JF-2
Scale: ½"=1'-0"

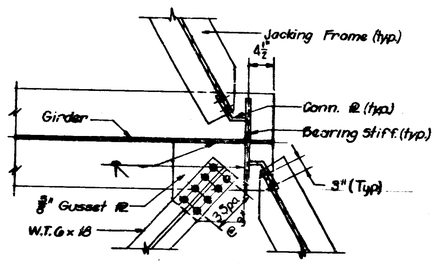

DETAIL B

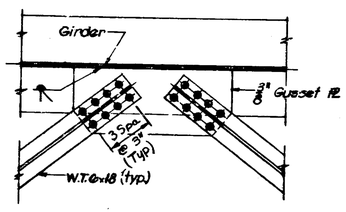

DETAIL C

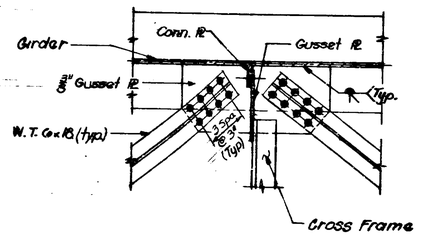

DETAIL D

NOTES:
See Dwg. S2 for General Notes
See Dwg. S8 for Structural Steel Notes & Framing Plan.
See Dwg. S9, S10, S12, S13, S14 and S15 for other Steel Details.


STEEL DETAILS
INDIANA STATE HIGHWAY COMMISSION

SCALE:- 1"=1'-0", UNLESS NOTED
MARCH 29, 1971
SUBMITTED FOR APPROVAL:
DRAWING:- S11 OF 18
PROJECT:- I-65-3(106) 111
CONTRACT NO. B-8877
BRIDGE FILE:- I-65-112-5723


DESIGNED ____ C'K'D ____
DRAWN Mac G.J.B C'K'D KRC
TRACED ____ C'K'D ____

Rev. 18-29-72 Fillet Weld Sizes
Rev. 3-23-72 Stiffener Size


PROJECT NO.	LINE	SHEET NO.	SHEET SHEETS	FILE

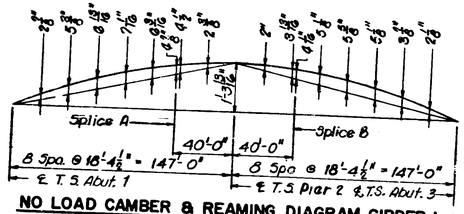


NO LOAD CAMBER & REAMING DIAGRAM GIRDER 1

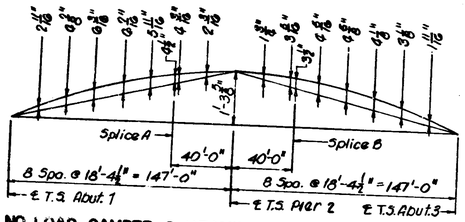


NO LOAD CAMBER & REAMING DIAGRAM GIRDER 2

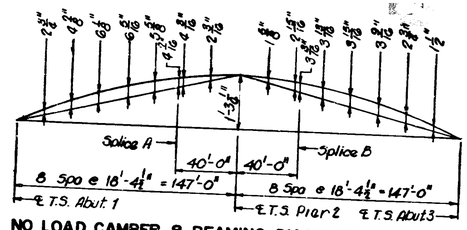


NO LOAD CAMBER & REAMING DIAGRAM GIRDER 3 & 4

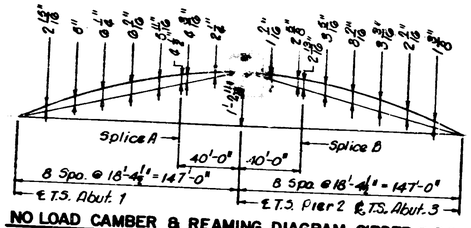

NO LOAD CAMBER & REAMING DIAGRAM GIRDER 5 & 6

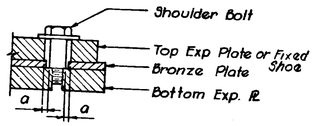


DETAIL "B"

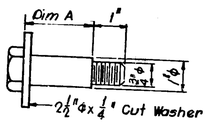


SHOULDER BOLT


TYPE OF SHOE	DIM A
ES-1, ES-2	3½"
ES-4, ES-5	2½"
FS-1, FS-2	2¼"

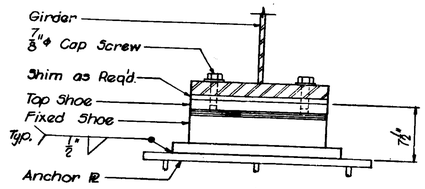


FIXED SHOE (FS-3)

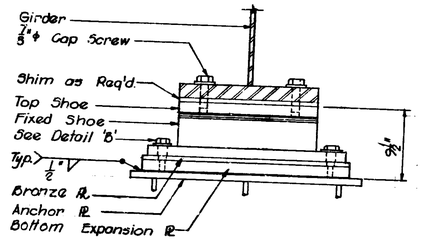

FIXED SHOE (FS-1 & 2)

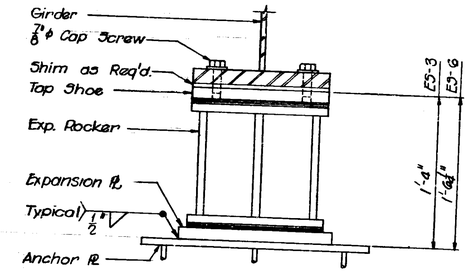

EXPANSION SHOE (ES-3 & 6)

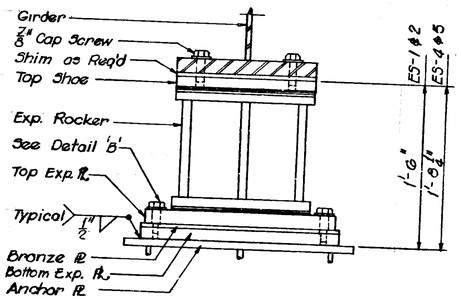

EXPANSION SHOE (ES-1, 2, 4 & 5)

NOTES:

See Dwg. S2 for General Notes
See Dwg. S8 for Structure Steel Notes & Framing Plan
See Dwg S9, S10, S11, S13, S14 and S15, for other Steel Details.
If curves in Plates & Angles are flamed cut, they shall be ground smooth.

STEEL DETAILS

INDIANA STATE HIGHWAY COMMISSION

SCALE:- ½" = 1'-0"

SUBMITTED FOR APPROVAL:

MARCH 29, 1971

DRAWING:- S12 OF 18
PROJECT:- I-65-3(106) III
CONTRACT NO. 8-8877
BRIDGE FILE:- I-65-112-5723

CARL W. COLE — No. 3683 STATE — REGISTERED PROFESSIONAL ENGINEER


DESIGNED — CK'D —
DRAWN MK, GJR CK'D KAC
TRACED — CK'D —

BRIDGES OVER 20' SPAN

PUB. ROAD SEC. NO.	STATE	PROJECT NO.	FISCAL YEAR	SHEET NO.	TOTAL SHEETS
4	IND.	I-65-3 (106) III	1971	14	33


PROJECT NO.	LINE	SHEET NO.	VOL. NO. SHEETS	FILE

BRIDGES OVER 20' SPAN					
PUB. ROAD ASSN. NO.	STATE	PROJECT NO.	FISCAL YEAR	SHEET NO.	TOTAL SHEETS
4	IND.	I-65-3 (106) 111	1971	15	33

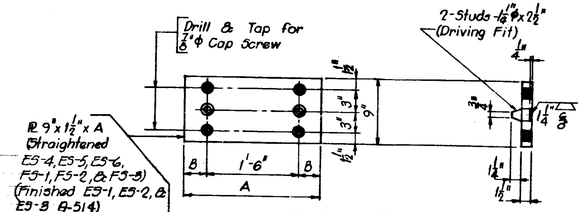


TOP SHOE

TYPE OF SHOE	A	B
(E5-2,3,5,&6)(F5-2&3)	2'-0"	3"
E5-1	2'-2"	4"
F5-1	2'-10 1/2"	3 1/4"
E5-4	2'-1 1/2"	3 3/4"

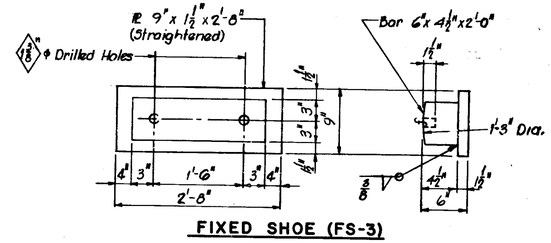


FIXED SHOE (FS-3)

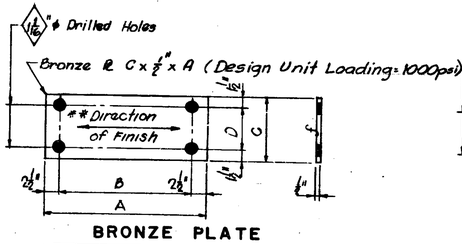

BRONZE PLATE


TYPE OF SHOE	A	B	C	D
E5-1	2'-11"	2'-6"	1'-8"	1'-5"
E5-2	2'-9"	2'-4"	1'-8"	1'-5"
E5-5, F5-2	2'-9"	2'-4"	9"	6"
E5-4, F5-1	2'-9 1/2"	2'-4 1/2"	9"	6"

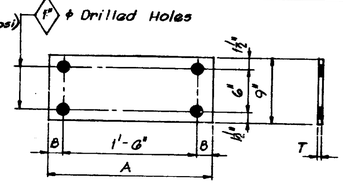

SHIM


SHIM THICKNESS TABLE

GIRDER No	ABUT. 1			PIER 2			ABUT. 3		
	A	B	T	A	B	T	A	B	T
Girder No 1	2'-0 1/2"	3 1/4"	1/2"	2'-2"	4"	2 1/8"	2'-1 1/2"	3 3/4"	1/2"
Girder No 2	2'-0"	3"	1/2"	2'-0"	3"	1/2"	2'-0"	3"	1/2"
Girder No 3	2'-0"	3"	1/2"	2'-0"	3"	1/2"	2'-0"	3"	1/2"
Girder No 4	2'-0"	3"	1/2"	2'-0"	3"	1 1/8"	2'-0"	3"	5/16"
Girder No 5	2'-0"	3"	1 3/16"	2'-0"	3"	11/16"	2'-0"	3"	1/16"
Girder No 6	2'-0"	3"	1 5/16"	2'-0"	3"	1 1/16"	2'-0"	3"	5/16"
Girder No 7	2'-0"	3"	1 3/16"	2'-0"	3"	1/2"	2'-0"	3"	1/2"
Girder No 8	2'-0 1/2"	3 1/4"	1/2"	2'-2"	4"	1/2"	2'-1 1/2"	3 3/4"	1/2"

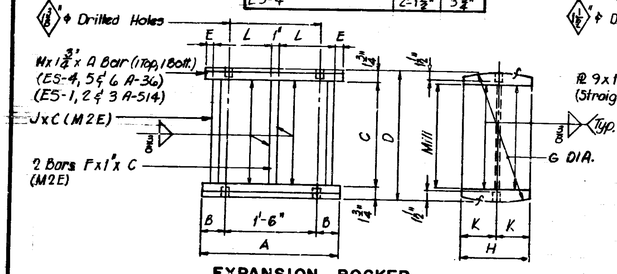


EXPANSION ROCKER

TYPE OF SHOE	A	B	C	D	E	F	G	H	J	K	L
E5-1	2'-2"	4"	8 1/2"	1'-0"	5/8"	2 5/8"	1'-0"	6"	W24x145	3"	11 3/4"
E5-2&3	2'-0"	3"	8 1/2"	1'-0"	1 1/4"	2 5/8"	1'-0"	6"	W21x142	3"	10 1/2"
E5-4	2'-1 1/2"	3 3/4"	11 1/2"	1'-3"	1/2"	3 5/8"	1'-3"	7 1/2"	W24x145	3 3/4"	11 3/8"
E5-5&6	2'-0"	3"	11 1/2"	1'-3"	1 1/16"	3 3/8"	1'-3"	7 1/2"	W21x142	3 3/4"	10 5/8"

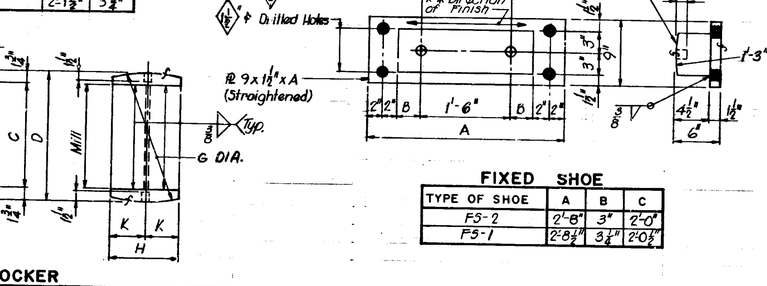


FIXED SHOE

TYPE OF SHOE	A	B	C
F5-2	2'-8"	3"	2'-0"
F5-1	2'-8 1/2"	3 1/4"	2'-0 1/2"

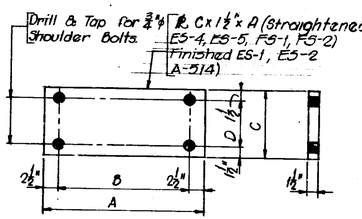


BOTTOM EXPANSION PLATE

TYPE OF SHOE	A	B	C	D
E5-1	2'-11"	2'-0"	1'-8"	1'-5"
E5-2	2'-9"	2'-4"	1'-8"	1'-5"
E5-5, F5-2	2'-9"	2'-4"	9"	6"
E5-4, F5-1	2'-9 1/2"	2'-4 1/2"	9"	6"

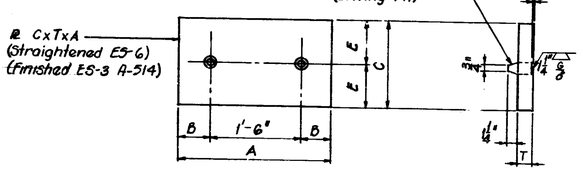

EXPANSION PLATE

TYPE OF SHOF	A	B	C	D	T	E
E5-5	2'-8"	7"	1'-8"	3 5/8"	2 1/2"	10"
E5-6	2'-8"	7"	9"	2 5/8"	1 3/8"	4 1/2"

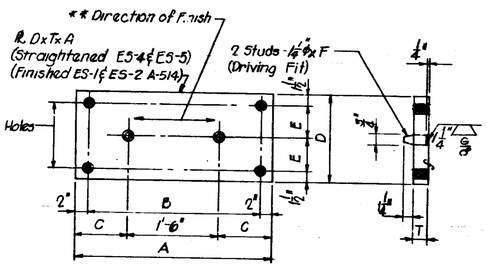

TOP EXPANSION PLATE

TYPE OF SHOE	A	B	C	D	E	F	T
E5-1	2'-10"	2'-6"	8"	1'-8"	8 1/2"	3 1/4"	2 1/2"
E5-2	2'-8"	2'-4"	7"	1'-8"	8 1/2"	3 1/4"	2 1/2"
E5-4	2'-8 1/2"	2'-4 1/2"	7 1/4"	9"	3"	2 5/8"	1 3/8"
E5-5	2'-8"	2'-4"	7"	9"	3"	2 1/2"	1 3/8"

NOTES:

See Dwg. S2 for General Notes
See Dwg. S8 for Structural Steel Notes & Framing Plan.
All steel shall be A-36, Unless noted
** Indicates minimum finish to be 125 Micro-inch R.M.S. Curved surfaces of shoes to be machined after weldments are completed
See dwg. S9, S10, S11, S12, S14, and S15 for other steel details.

STEEL DETAILS

INDIANA STATE HIGHWAY COMMISSION

SCALE:- 1 1/2" = 1'-0"

MARCH 29, 1971

SUBMITTED FOR APPROVAL:


DRAWING:- S13 OF 18
PROJECT:- I-65-3(106)111
CONTRACT NO. B-8877
BRIDGE FILE:- I-65-112-5723

CHAS. W. COLE REGISTERED No. 3666 PROFESSIONAL ENGINEER

DESIGNED _____ C'K'D _____
DRAWN MRC C'K'D KAC
TRACED _____ C'K'D _____

PROJECT NO.	LOG	WORK ORD.	CONTR. ORDER	FILE

BRIDGES OVER 20' SPAN					
FED. ROAD DESIGN.	STATE	PROJECT NO.	FISCAL YEAR	SHEET NO.	TOTAL SHEETS
4	IND.	I-65-3 (106)111	1971	16	33

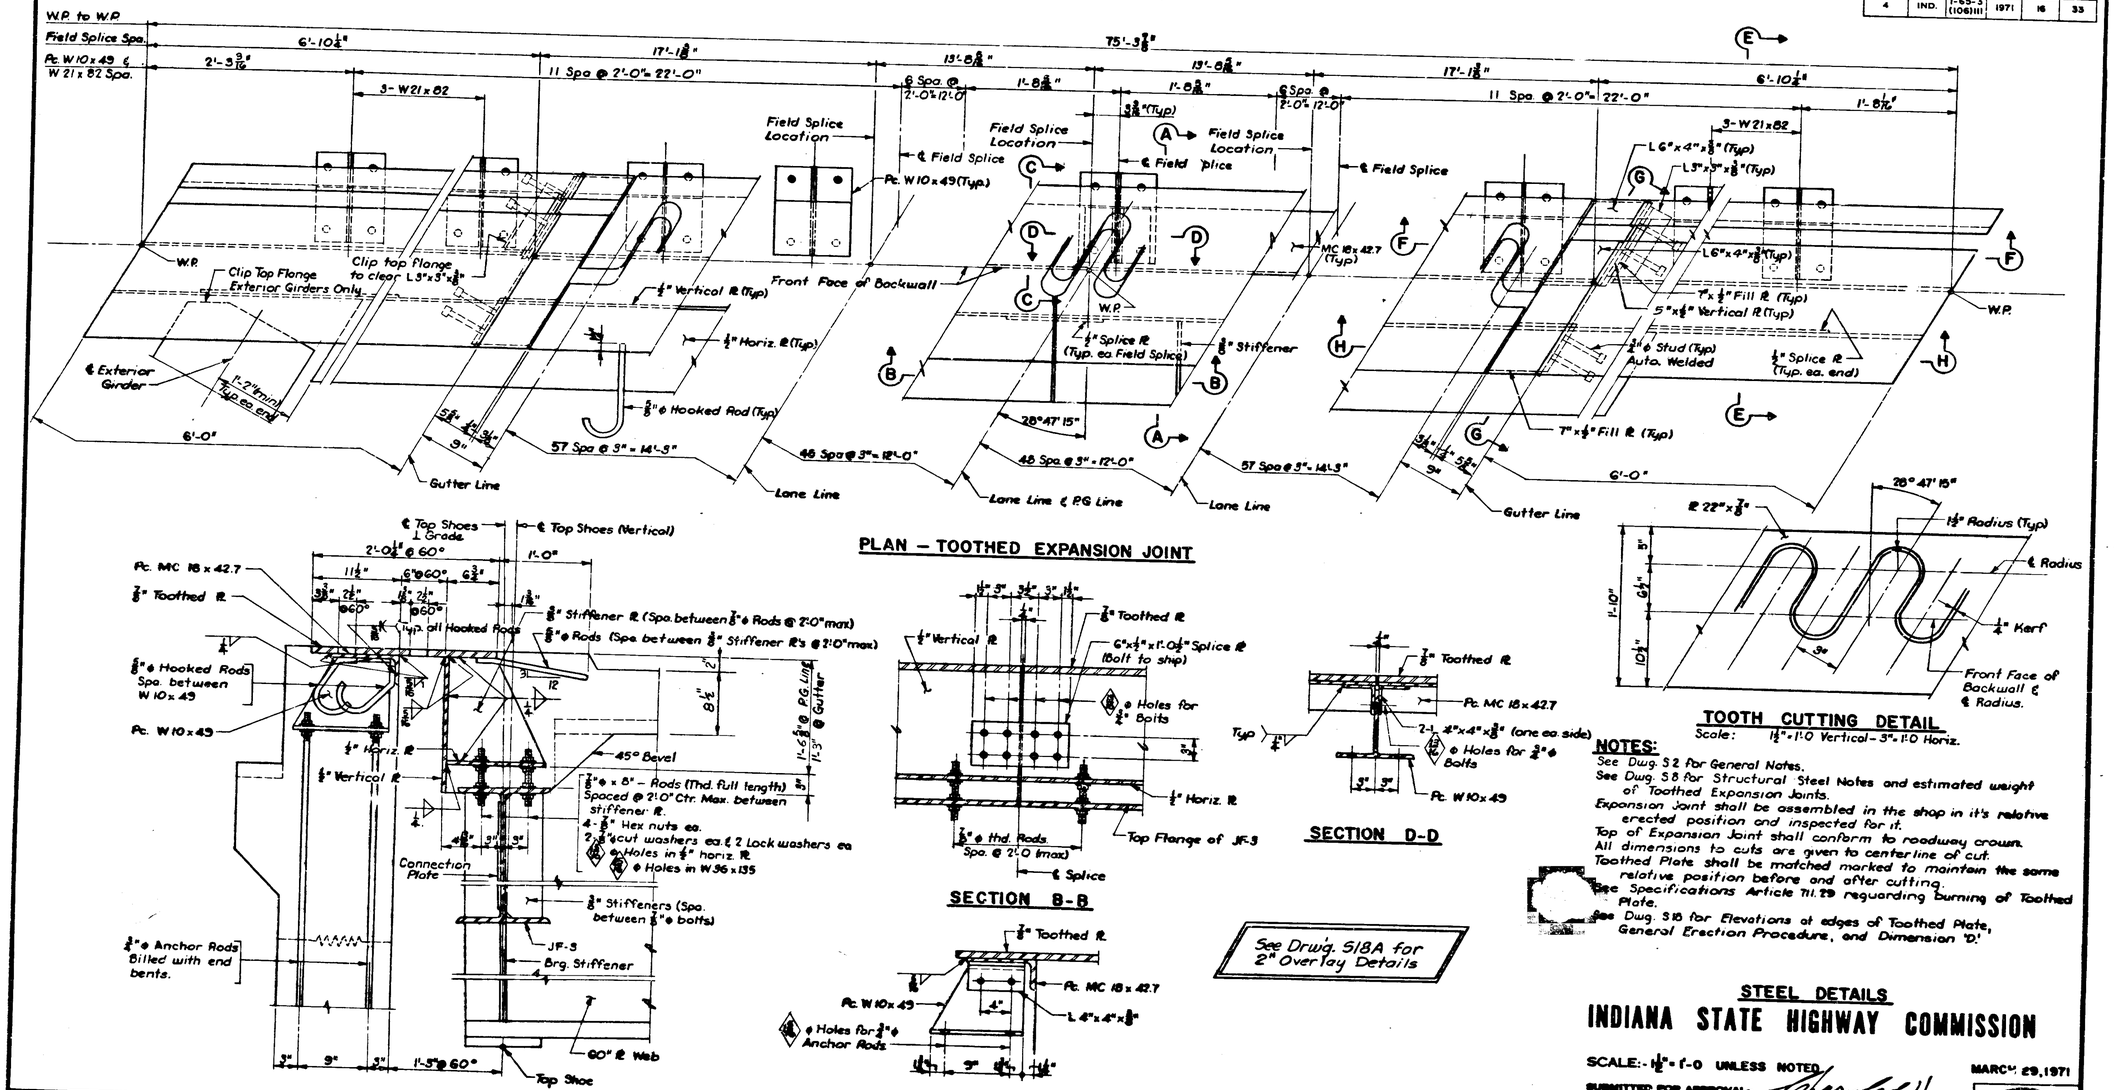

PLAN — TOOTHED EXPANSION JOINT

SECTION A-A

SECTION B-B

SECTION C-C

SECTION D-D

See Drwg. 518A for 2" Overlay Details

TOOTH CUTTING DETAIL

Scale: 1 1/2" = 1'-0 Vertical - 3" = 1'-0 Horiz.

NOTES:

See Dwg. S2 for General Notes.
See Dwg. S8 for Structural Steel Notes and estimated weight of Toothed Expansion Joints.
Expansion Joint shall be assembled in the shop in it's relative erected position and inspected for it.
Top of Expansion Joint shall conform to roadway crown.
All dimensions to cuts are given to centerline of cut.
Toothed Plate shall be matched marked to maintain the same relative position before and after cutting.
See Specifications Article 711.29 regarding burning of Toothed Plate.
See Dwg. S15 for Elevations at edges of Toothed Plate, General Erection Procedure, and Dimension 'D.'

Rev. 8-3-73 Section A-A & Plan
Rev. 12-29-72 Fillet Weld Sizes

DESIGNED ____ C'K'D ____
DRAWN T.J.H. C'K'D KAC
TRACED ____ C'K'D ____

STEEL DETAILS

INDIANA STATE HIGHWAY COMMISSION

SCALE:- 1/2" = 1'-0 UNLESS NOTED. MARCH 29, 1971

SUBMITTED FOR APPROVAL:


DRAWING:- S14 OF 18
PROJECT:- I-65-3 (106) III
CONTRACT NO. B-8877
BRIDGE FILE:- I-65-112-5723

STATE OF INDIANA No. 3688


PROJECT NO.	LINE	SHEET NO.	TOTAL SHEETS	FILE

Rev. 8-3-73 HAP/CHM

BRIDGES OVER 20' SPAN					
FUR. ROAD RTE. NO.	STATE	PROJECT NO.	FISCAL YEAR	SHEET NO.	TOTAL SHEETS
4	IND.	I-65-3 (106)111	1971	17	33

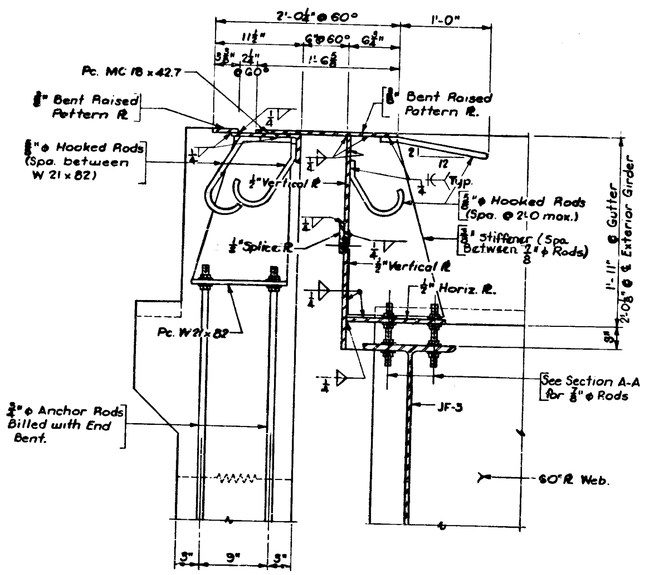


SECTION E-E

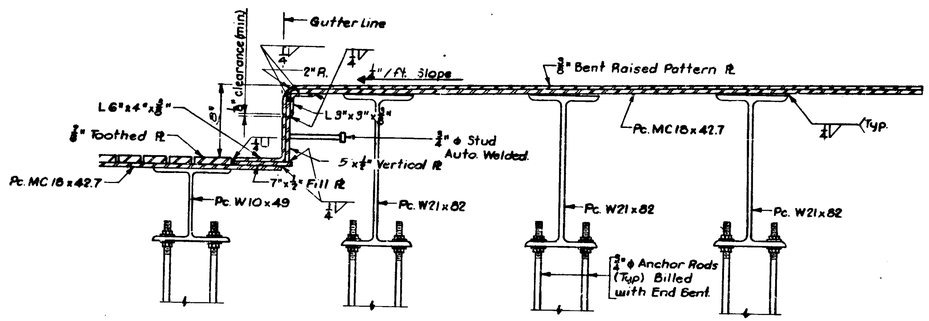


SECTION F-F

See Drw'g. S18A for 2" Overlay Details.

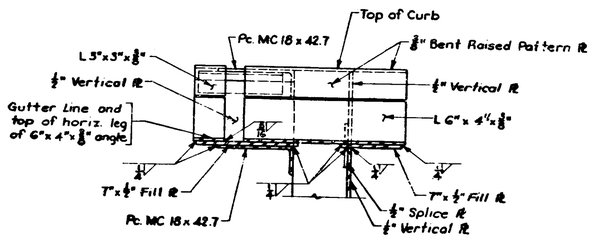

SECTION G-G

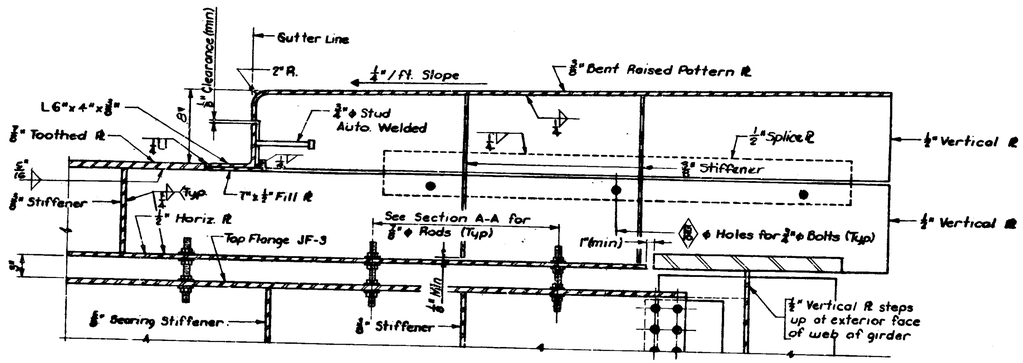

SECTION H-H

NOTE:
See dwg. S14 for Notes.

STEEL DETAILS

INDIANA STATE HIGHWAY COMMISSION

SCALE:- 1½" = 1'-0"

SUBMITTED FOR APPROVAL:

MARCH 29, 1971

DRAWING:- S 15 OF 18
PROJECT:- I-65-3 (106)111
CONTRACT NO. B-8877
BRIDGE FILE:- I-65-112-5723

CHAS. W. LOLE JR. REGISTERED (No. 3483) PROFESSIONAL ENGINEER

DESIGNED ____ CK'D ____
DRAWN TJH CK'D KAC
TRACED ____ CK'D ____


Rev. 8-3-73 H.A.P./C.H.M.

Rev. 8-3-73 Sec. G-G, F-F, & H-H
Rev. 12-29-72 Fillet Weld Size

PROJECT NO.	LINE	BRIDGE NO.	TOTAL SHEETS	FILE


Rev. 12-16-71 J.J.W. Chk. A.W.M.
Rev. 2-23-72 AWM
Rev 8-3-73 HRR/CHM

BRIDGES OVER 20' SPAN					
FUR. ROAD SYS. NO.	STATE	PROJECT NO.	FISCAL YEAR	SHEET NO.	TOTAL SHEETS
4	IND.	I-65-3 (106) 111	1971	16	33

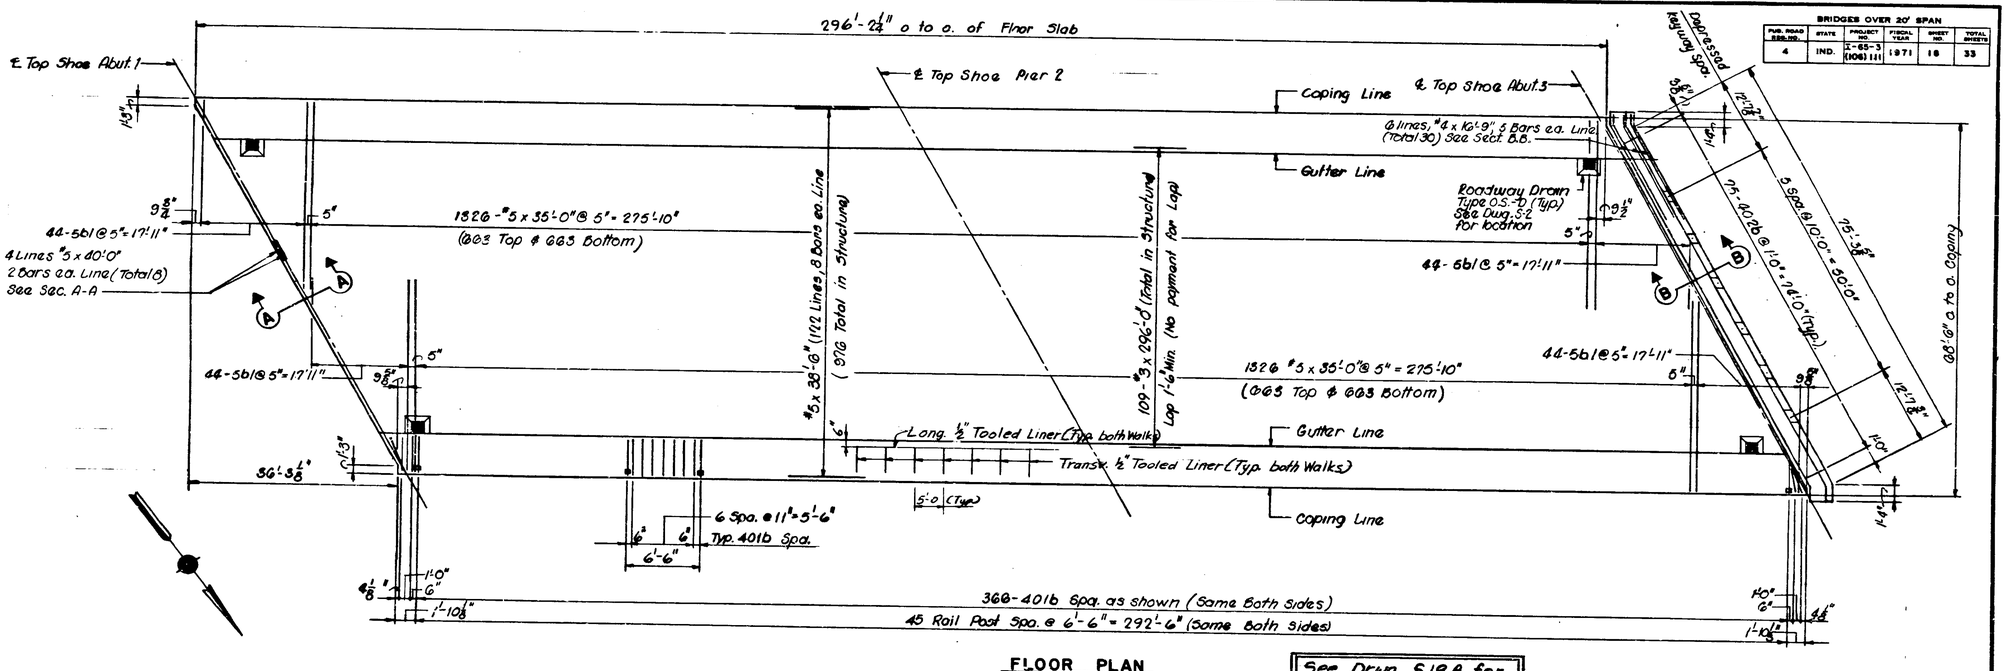

FLOOR PLAN
Scale: 3/32"=1'-0"

See Drwg. S18A for Overlay details

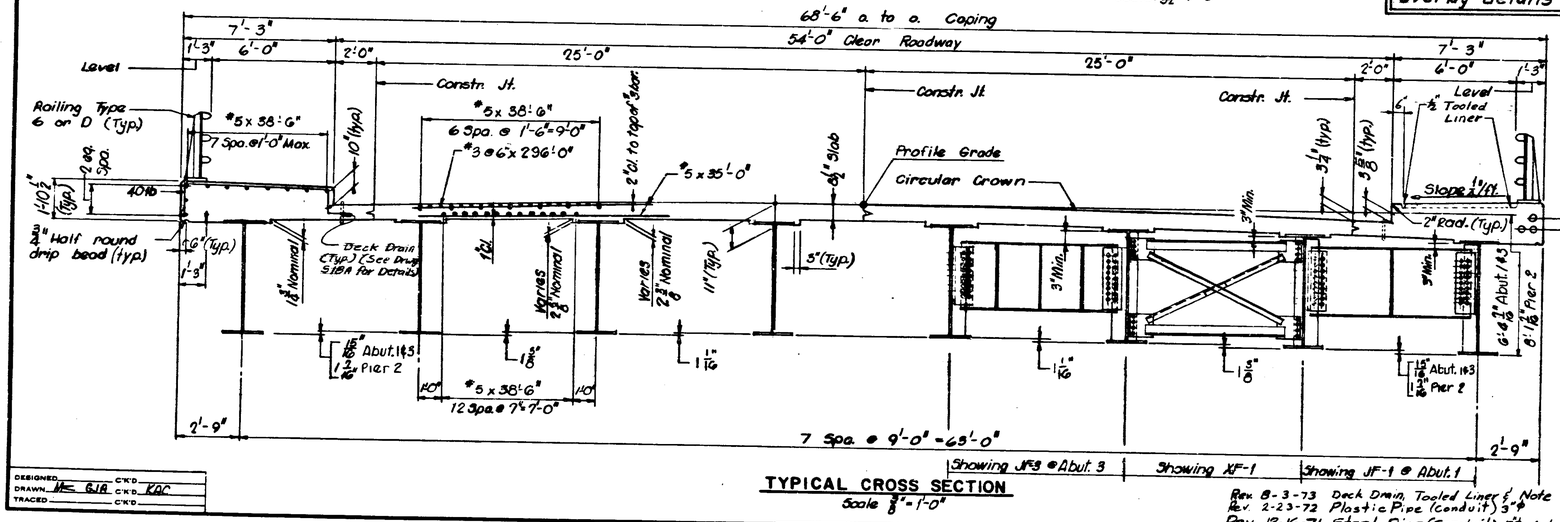

TYPICAL CROSS SECTION
Scale ⅜"=1'-0"

NOTES:

See dwg. S2 for General Notes.
See dwg. S17 for Section A-A, B-B, Corner Details, Drain Detail and Depressed keyway.
See Br. Std. C1 for Reinforcing Bar Notes.
See Br. Std. D for detail of Roadway Drains.
See Br. Std. BR1 & BR2 for details of Aluminum Railing Type 6.
See Br. Std. BR3 & BR4 for details of Steel Railing Type D.
See dwg. S18 for plan of Poure and Screeds.
Welded deformed steel wire fabric may be used in place of #3 Bars in Top of Slab.
See Drwg. S2 for location of 8" Light Standard.

Rev. 8-3-73 Deck Drain, Tooled Liner & Note
Rev. 2-23-72 Plastic Pipe (conduit) 3" ϕ
Rev. 12-16-71 Steel Pipe (Conduit) 2" ϕ Added.

DESIGNED ____ C'K'D. ____
DRAWN MC GJA C'K'D. KAC
TRACED ____ C'K'D. ____

FLOOR DETAILS
INDIANA STATE HIGHWAY COMMISSION


SCALE:- AS NOTED
SUBMITTED FOR APPROVAL: [signature]
MARCH 29, 1971


DRAWING:- S16 OF 18
PROJECT:- I-65-3(106)111
CONTRACT NO. B-8877
BRIDGE FILE:- I-65-112-5723

CHARLES W. COLE JR. REGISTERED No. 3682 STATE OF INDIANA PROFESSIONAL ENGINEER

PROJECT NO.	LINE	SHEET NO.	DATE	FILE


Rev 12-16-71 J.J.W. Corr. shown
Rev. 2-23-72 AWM
Rev 8-3-73 HRP/SHW

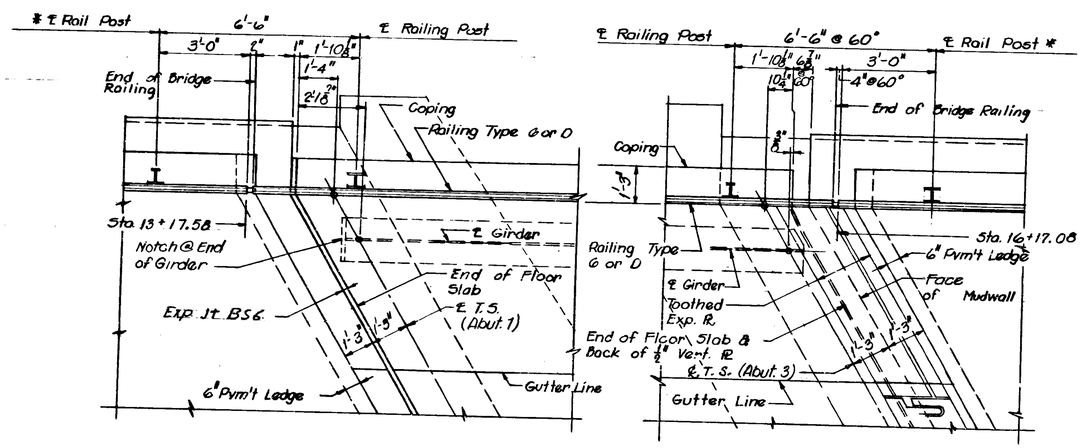

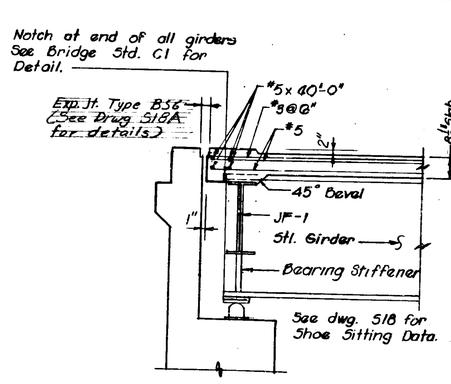

SECTION A-A

NOTE:
Hatched area to be poured & billed with superstructure.

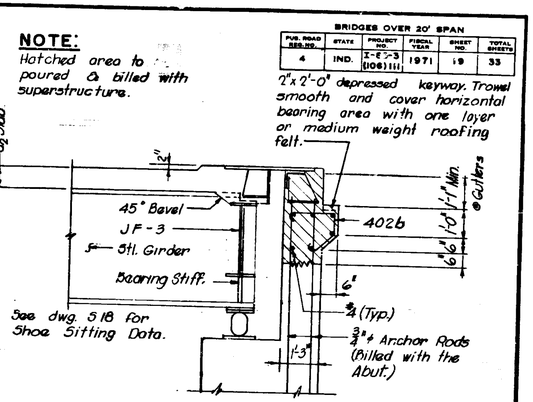


SECTION B-B

BRIDGES OVER 20' SPAN

FED. ROAD SER. NO.	STATE	PROJECT NO.	FISCAL YEAR	SHEET NO.	TOTAL SHEETS
4	IND.	I-65-3 (106)111	1971	19	33


2"x 2'-0" depressed keyway. Trowel smooth and cover horizontal bearing area with one layer of medium weight roofing felt.

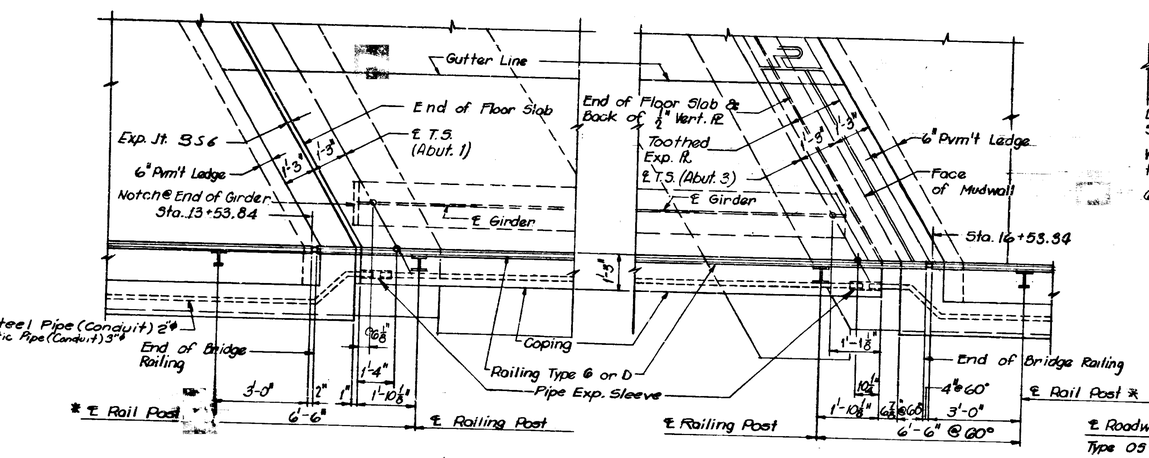

ABUT. 1


ABUT. 3

CORNER DETAILS

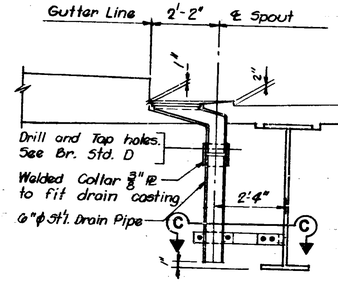


NOTE:
Cost of all plates & hardware to be included in cost of 6" ϕ Steel Drain Pipe.

DRAIN DETAIL

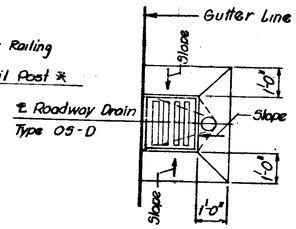


℄ Roadway Drain Type 05-D

PLAN OF ROADWAY DRAIN OPENING

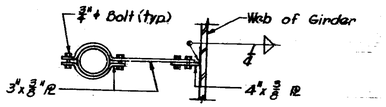

SECTION C-C

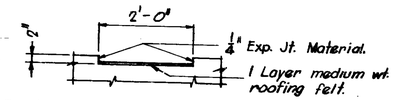

2"x 2'-0" DEPRESSED KEYWAY

NOTES:
See dwg. 52 for General Note.
See dwg. 516 and 518 for Floor details.
See Br. Std. BR1 & BR2 for details of Aluminum Railing Type 6.
See Br. Std BR3 & BR4 for details of Steel Railing Type D.
See dwg. 518 for Pour & Screed Diagram and Bill of Materials.
*Indicates items not included in Bridge Summary

See Drwg. 518A for Overlay and Exp. Joint Type BS6 Details

Rev. 8-3-73 Exp Jt Type BS6, Sec 13-B & Drain Detail
Rev. 2-23-72 Plastic Pipe (Conduit) 3"ϕ
Rev. 12-16-71 Steel Pipe (Conduit) 2"ϕ Added

FLOOR DETAILS

INDIANA STATE HIGHWAY COMMISSION

SCALE:- ½" = 1'-0"

MARCH 29, 1971


SUBMITTED FOR APPROVAL:

DRAWING:-517 OF 18
PROJECT:-I-65-3(106)111
CONTRACT NO. B-8377
BRIDGE FILE:-I-65-112-5723

CHAS. W. COLE JR. REGISTERED No. 3653 STATE INDIANA PROFESSIONAL ENGINEER

DESIGNED ___ C'K'D ___
DRAWN MC G.B. C'K'D KAC
TRACED ___ C'K'D ___

PROJECT NO.	LINE	SHEET NO.	TOTAL SHEETS	FILE

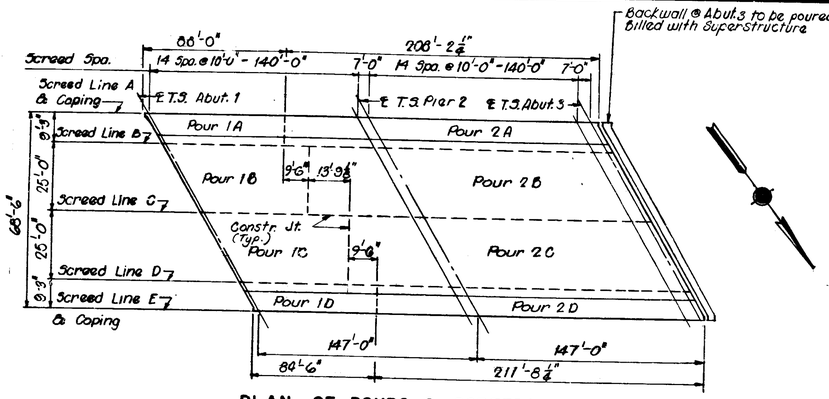


PLAN OF POURS & SCREEDS

NOTES:

Sequence of pours to be made in order of pour numbers. All superstructure construction joints are optional except as noted, and pours may be made continuous provided the pour terminates at a construction joint indicated on the plans. The Contractor may change the width of pours, sequence of pours, or location of construction joints subject to the approval of the Engineer.
After structural steel has been erected, concrete forms shall not be blocked against the expansion end of the steel in making any pours adjacent to steel spans.


GENERAL PROCEDURE

1. After the structural steel has been erected, adjust the superstructure longitudinally so that the dimension @ Abut. 1 parallel to the Girder from ℄ Exp. Shoe to front face backwall is 1-5⅛ regardless of temperature.
2. With the superstructure in the adjusted position, weld the bearing plate of the fixed shoes at Abut. 1 to the anchor plates.
3. Adjust the expansion plate under each expansion shoe in accordance with dimension 'A' or 'B' in Table II for the prevailing temparature. Note that dimension 'A' is always the distance from a vertical line through the center line of the top shoes to the center line of the expansion plate in a direction away from the fixed shoe. Weld the expansion plate to the anchor plate.
4. Set the toothed expansion joint and adjust it to the elevations shown on this sheet using double nuts on anchor rods.
5. Adjust the toothed expansion joint horizontally so that openings 'D' between teeth are equal and longitudinally so that opening 'D' corresponds to the value in Table I for the prevailing temperature.
6. Screed elevations shall be determined by adding the concrete dead load deflections to the required final concrete elevations at all screed points. Take elevations at all screed points on top of girder adjacent to screed point. Subtract these elevations from the elevations corrected for deflection and use the resulting dimensions as the height for setting the screed or coping form above that point. This dimension remains constant regardless of how much or in what order the concrete is poured. Do not set screed or coping forms by leveling. Screed elevations will be furnished on request.
7. No concrete in the floor is to be poured until the above operations are completed.

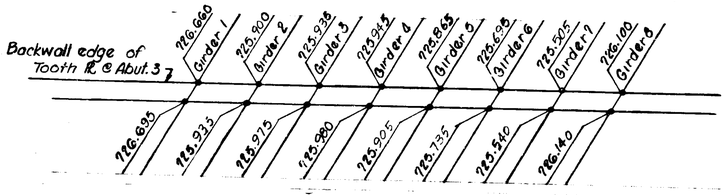


ELEVATIONS AT EDGES OF TOOTHED EXP. PLATE


Rev 8-3-73 Bill of Materials & Tooth Jt. Elev.
Rev. 2-23-72 Bill of Materials
Rev 12-16-71 Notes, Bill of Materials

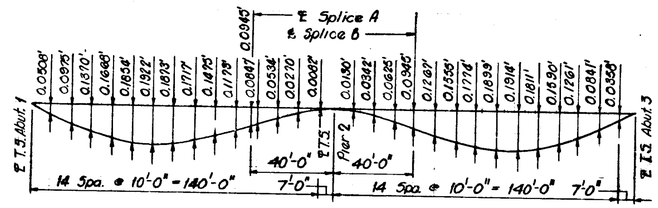


CONCRETE DEAD LOAD DEFLECTION GR. 1 & 8

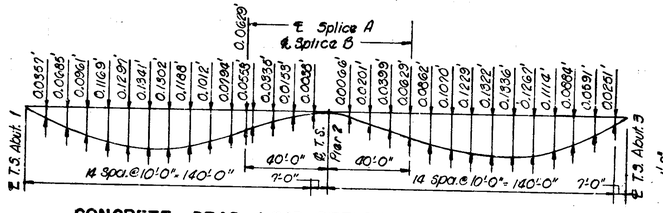


CONCRETE DEAD LOAD DEFLECTION GR. 2 & 7

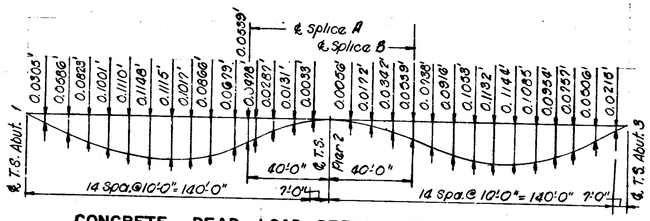

CONCRETE DEAD LOAD DEFLECTION GR. 3 THRU 6

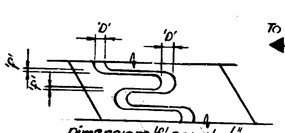

PARTIAL PLAN OF TOOTHED EXPANSION JT.

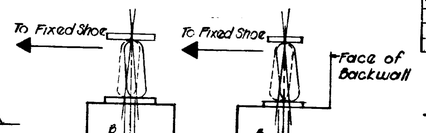


SHOE SETTING DIAGRAMS

TABLE II

TEMPERATURE	DIMENSION A							DIMENSION B		
	0°	20°	40°	60°	80°	100°	120°	80°	100°	120°
PIER 2	11/16"	7/16"	1/4"	0"	—	—	—	1/4"	2/16"	11/16"
ABUT. 3	1⅞"	1 2/16"	15/16"	½"	1/16"	—	—	—	7/16"	7/8"

TABLE I

TEMPERATURE	0°	20°	40°	60°	80°	100°	120°
DIMENSION 'D'	4¼"	3 13/16"	3 5/16"	2 7/8"	2 2/16"	1 15/16"	1½"

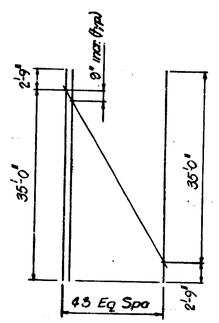

MARK & SIZE	NO. OF BARS	LENGTH	WEIGHT
601B	4	3'-8	
602B	10	4'-6	
Total #6			90#

BRIDGES OVER 20' SPAN

FED. ROAD DIST. NO.	STATE	PROJECT NO.	FISCAL YEAR	SHEET NO.	TOTAL SHEETS
4	IND.	I-65-3 (108)11	1971	20	33

BILL OF MATERIALS

REINFORCING STEEL

MARK & SIZE	NO. OF BARS	LENGTH	WEIGHT (lbs.)
561	196	37'-9"	
#5	8	40'-0"	
#5	976	38'-6"	
#6	2652	35'-0"	
			183,266
Total No. 5 Bars			
401b	732	10'-6"	
402b	75	4'-0"	
#4	30	10'-9	
Total No. 4 Bars			5,670
#3	109	296'-0"	
Total No. 3 Bars			12,131
Total Reinf Bars			161,157

CONCRETE QUANTITIES

Class 'C' Concrete	Cu. Yds.
Pour 1A	47.1
Pour 1B	59.1
Pour 1C	59.1
Pour 1D	46.9
Pour 2A	114.2
Pour 2B	143.2
Pour 2C	143.2
Pour 2D	114.4
Backwall	12.4
Total Class 'C' Conc.	739.6

MISCELLANEOUS

Plastic Pipe (Conduit) 5"	592 Lin. Ft.
Railing Type G or D	600 Lin. Ft.
6" ϕ Steel Drain Pipe (Standard Weight)	18 Lin. Ft.
Anchor Bolts - AR 22	4 Each
Steel Pipe (Conduit) 2" ϕ	296 Lin. Ft.
Roadway Drains Type OS-D, G (2 @ ea)	992 lbs.

NOTES:

See dwg. S 2 for General Notes.
See Br. Std. C1 for Reinforcing Bar Notes.
See Br Std. D for Details of Roadway Drain.
See Br. Std. R2A for 601B & 602B bending diagrams.

FLOOR DETAILS

INDIANA STATE HIGHWAY COMMISSION

SCALE:- NONE


SUBMITTED FOR APPROVAL:

MARCH 29, 1971


DRAWING:- S18 OF 18
PROJECT:- I-65-3(108)11
CONTRACT NO. B-8877
BRIDGE FILE:- I-65-112-5723

DESIGNED MAC CHK'D
DRAWN GJB CHK'D KAC
TRACED CHK'D

Rev. 12-16-71 Bill of Materials AWM
Rev. 2-23-72 AWM
Rev 8-3-73 HGP/CHM

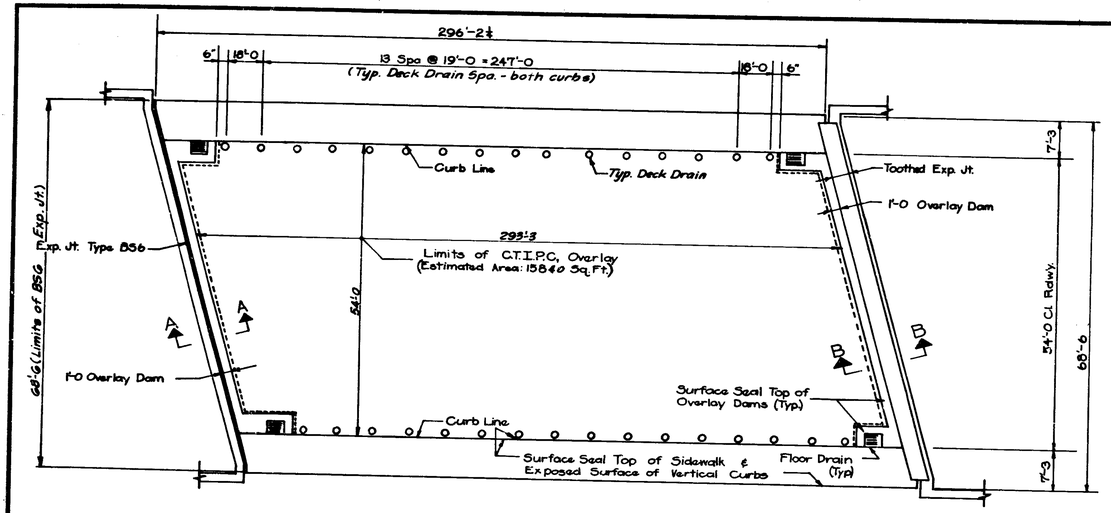

OVERLAY PLAN

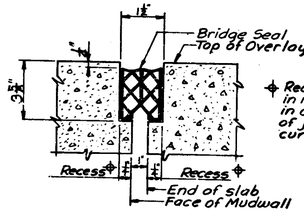


◆ Recess shall be sawcut in roadway and formed in curb areas. See details of joint installation at curbs.

Size of Seal	= 2½ x 2¾
Minimum Joint Width	= 1½
Maximum Joint Width	= 2½
Minimum Joint Width at Installation	= 1½
Minimum Joint Depth at Installation	= 3⅜

DETAIL - EXP. JOINT-TYPE B56

FEDERAL ROAD DIVISION NO.	STATE	PROJ NO	FISCAL YEAR	SHEET NO.	TOTAL SHEETS
4	IND.	I-65-3 (106)111	1974	20A	33

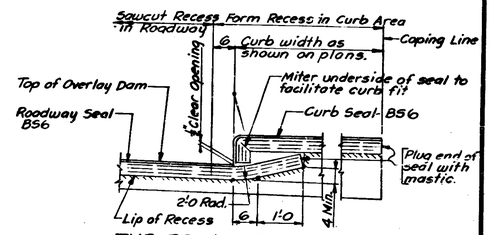


TYP. B56 JOINT INSTALLATION AT 8" CURBS◆◆


◆◆ At Overlay Dams, curb height will be 2 inches less than shown on floor details.

BILL OF MATERIALS

Coal Tar Interlayer Protective Coat*	1 Lump Sum
Bituminous Mixture for Approaches*	193.6 Tons
Deck Drains	32 Ea.
Surface Seal	4841 Sq. Ft.
Expansion Joint - Type B56	82.2 Lin. Ft.


*Bit. Surface to be paid for as "Bituminous Mixture for Approaches" and shall consist of:
170#/Sq. Yd. Hot Asphaltic Concrete Surface Type B
OVER 50#/Sq. Yd. Hot Asphaltic Conc. Surface Type D
or
170#/Sq. Yd. Hot Asphaltic Emulsion Surface Type III
OVER 50#/Sq. Yd. Hot Asphaltic Emulsion Surface Type IV

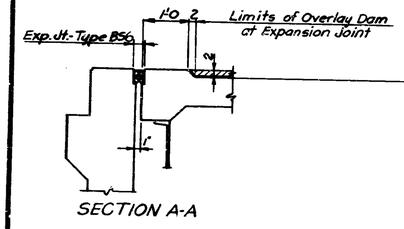

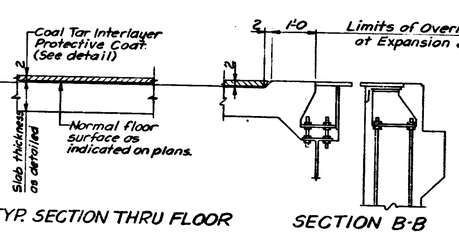


TYP. SECTION THRU FLOOR


SECTION B-B

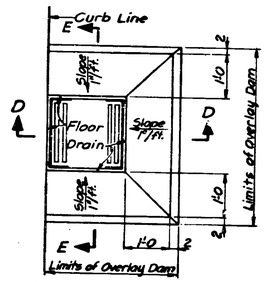


OVERLAY DAM AT FLOOR DRAINS PLAN

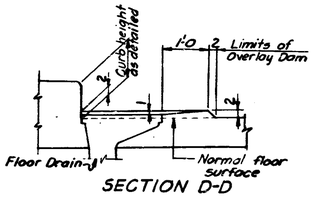


SECTION D-D

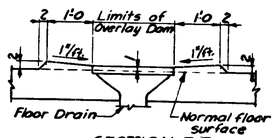

SECTION E-E

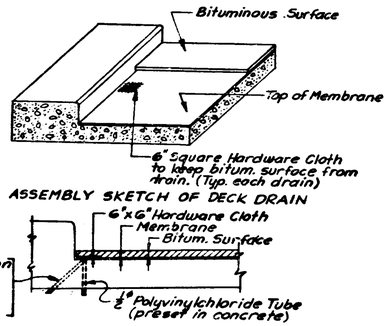

DECK DRAIN DETAIL

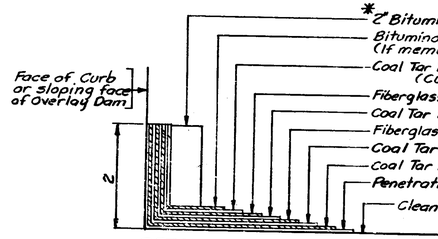

DETAIL - COAL TAR INTERLAYER PROTECTIVE COAT

NOTES:

Work this drawing with floor details.

Overlay Dams at ends of floor slab and adjacent to floor drains shall be poured monolithic with the slab.

Surface seal the top surface of all overlay dams, the exposed vertical face of all curbs and the top surface of curbs, walks and medians, where applicable. See Overlay Plan.

DETAILS - C.T.I.P.C. OVERLAY AND EXP. JOINT - TYPE B5

INDIANA STATE HIGHWAY COMMISSION

SCALE:- No Scale

DATE:- AUG. 3, 1973

Robert W. Bettig

DESIGNED J.J.W. C'K'D.
DRAWN H.R.P. C'K'D.
TRACED W.T.N. C'K'D. H.R.P.

DRAWING:- 18A OF 18 SHEET:- 20A OF 33

PROJECT:- I-65-3(106) III

CONTRACT NO. 8-8877

BRIDGE FILE:- I-65-112-5723

ROBERT W. BETTIG — No. 6403 — STATE OF INDIANA — REGISTERED PROFESSIONAL ENGINEER

BRIDGE FILE

STRUCTURE QUANTITIES

ITEM	CONCRETE CLASS C SUBSTR. CU. YDS.	CONCRETE CLASS C SUPERSTR. CU. YDS.	CONCRETE CLASS B ABOVE FTG. CU. YDS.	CONCRETE CLASS B IN. FTG. CU. YDS.	CONCRETE RAILING CLASS A CU. YDS.	CONCRETE RAILING CLASS A LIN. FT.	REINF. STEEL TOTAL LBS.	STRUCT. STEEL *** LBS.	BRONZE PLATES LBS.	ANCHOR PLATES MK-AP 8 EACH	ANCHOR RODS MK-AR 10 EACH
Substructure											
Abutment 1			226.1	73.3			22,686			8	
Pier 2			183.0	78.0			13,975			8	
Abutment 3			160.4	61.1			16,507			8	74
Superstructure		739.6									
							161,157	1,254,200	748		
Reinf. Steel for Approach Structures											
Reinf. Steel for R.C. Bridge Approaches											
Reinf. Steel for Lip Gutter, Pvmt., Tapers, etc.											
TOTALS		739.6	569.5	212.4			214,325	1,254,200	748	24	74

ITEM	UNTREATED TIMBER PILES NO.	UNTREATED TIMBER PILES LIN. FT.	TREATED TIMBER PILES NO.	TREATED TIMBER PILES LIN. FT.	STEEL ENCASED CONC. PILES NO.	STEEL ENCASED CONC. PILES LIN. FT.	STEEL H PILES BEARING NO.	STEEL H PILES BEARING LIN. FT.	CAST IRON DRAIN PIPE LBS.	RAILING TYPE 6 OR D LIN. FT.	CAST IRON, GRATES, BASINS, C. FITTINGS LBS.	B BORROW CU. YDS.	6"ϕ STL DRAIN PIPE ϕ LIN. FT.	STEEL PIPE CONDUITS ϕ LIN. FT.	ANCHOR BOLTS MK-AR22 EACH	PLASTIC PIPE (CONDUIT) 3"ϕ Lin. Ft.	EXP. J. TYPE B56 LIN. FT.
												535		30		64	
												195					
												360		28		48	
										600	992		18	280	4	592	82