DESIGNATION	
2001996	
CONTRACT	BRIDGE FILE
B-43353	008-75-04883 C

STRUCTURE INFORMATION				
STRUCTURE	TYPE	SPAN AND SKEW	OVER	STATION
008-75-04883 C	Continuous Composite Steel Beam Bridge	5 Spans: 34'-6⅞", 61'-1¾", 72'-0", 61'-1¾" & 34'-6⅞" Skew: 49°00'00" Lt.	Yellow River	202+25.00 "A"

INDIANA DEPARTMENT OF TRANSPORTATION

BRIDGE PREVENTIVE MAINTENANCE

FOR SPANS OVER 20 FEET

ROUTE: SR 8 AT: RP 35+78

DESIGNATION NO. 2001996

NO ADDITIONAL RIGHT-OF-WAY REQUIRED FOR THIS PROJECT

Rigid Deck Overlay on SR 8 over Yellow River
Located 1.32 Miles West of SR 23
Section 20 & 29, T-33-N, R-1-W, Washington Township, Starke County, Indiana

Structure: 008-75-04883 C
over Yellow River Sta. 202+25.00 "A"
Begin Project Sta. 199+29.69 "A"
End Project Sta. 205+21.69 "A"




SCALE: 1" = 1,000'

TRAFFIC DATA		
A.A.D.T.	(2025)	4,146 V.P.D.
A.A.D.T.	(2045)	4,315 V.P.D.
D.H.V	(2045)	419 V.P.H.
DIRECTIONAL DISTRIBUTION		48.73 %
TRUCKS		4.22 % A.A.D.T.
		3.77% D.H.V.

DESIGN DATA	
DESIGN SPEED	55 M.P.H.
PROJECT DESIGN CRITERIA	3R (NON-FREEWAY)
FUNCTIONAL CLASSIFICATION	MAJOR COLLECTOR
RURAL/URBAN	RURAL
TERRAIN	LEVEL
ACCESS CONTROL	NONE

LAPORTE DISTRICT

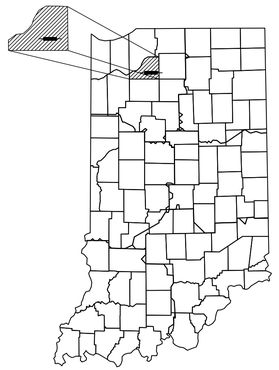

PROJECT LOCATION SHOWN BY —
STARKE COUNTY

LATITUDE: 41°17'17" LONGITUDE: 86°33'00"

BRIDGE LENGTH: 0.062 MI.
ROADWAY LENGTH: 0.051 MI.
TOTAL LENGTH: 0.113 MI.
MAX. GRADE: 1.00 %

HYDROLOGICAL UNIT CODE: 071200010505

INDIANA DEPARTMENT OF TRANSPORTATION
STANDARD SPECIFICATIONS DATED 2026
TO BE USED WITH THESE PLANS.

Lochner

MATTHEW EARL COCHRAN — REGISTERED — No. PE12200050 — STATE OF INDIANA — PROFESSIONAL ENGINEER

PLANS PREPARED BY: Lochner 219-324-4903 PHONE NUMBER

CERTIFIED BY: 6/9/2026 DATE

RECOMMENDED FOR LETTING: Stephanie J. Wagner 09/02/2026 DATE
INDIANA DEPARTMENT OF TRANSPORTATION

BRIDGE FILE
008-75-04883 C
DESIGNATION
2001996
SHEETS
1 of 14
CONTRACT
B-43353

Plot: 6/9/2026 1:30 PM AM_PM
File: c:\pw_working\lochner-pw-01\dms39769\Sht Title Sheet.dgn
Model: $MODEL_NAME$

UTILITIES

CenturyLink (CTCL) Telephone/Level 3/Lumen
Max Downey
maxwell.k.downney@lumen.com
260-301-5540
248 W. Monroe St., Decatur, IN 46733

NIPSCO Electric (Plymouth)
Dean Garrett
dagarrett@nisource.com
219-647-6260
801 E. 86th Ave., Merrillville, IN 46410

NIPSCO Gas (Plymouth)
Dean Garrett
dagarrett@nisource.com
219-647-6260
802 E. 86th Ave., Merrillville, IN 46410

Trunkline Gas Company (North Judson) Pipeline
Mick Braddock
mickey.braddock@energytransfer.com
765-869-5521
10483 W 600 S, Ambia, IN 47917

811 Know what's **below.** **Call** before you dig.

INDIANA UNDERGROUND
1-800-382-5544 OR CALL 811
24 HOURS A DAY 7 DAYS A WEEK

REVISIONS

SHEET NO.	DATE	REVISED

INDEX

SHEET NO.	SUBJECT
1	TITLE
2	INDEX
3	MAINTENANCE OF TRAFFIC
4	ROADWAY DETAILS
5	LAYOUT
6	EROSION CONTROL PLAN
7	GENERAL PLAN - EXISTING
8	GENERAL PLAN - PROPOSED
9	GENERAL PLAN - TYPICAL SECTION
10	STRUCTURE DETAILS
11-13	SUBSTRUCTURE PATCHING DETAILS
14	BRIDGE SUMMARY AND APPROACH SUMMARY OF QUANTITIES

MATTHEW EARL COCHRAN REGISTERED No. PE12200050 STATE OF INDIANA PROFESSIONAL ENGINEER

RECOMMENDED FOR APPROVAL *MATTHEW COCHRAN* 6/9/2026
DESIGN ENGINEER DATE


DESIGNED: YD 06/01/2022 | DRAWN: YD 06/01/2022
CHECKED: JS 06/01/2022 | CHECKED: JS 06/01/2022

INDIANA
DEPARTMENT OF TRANSPORTATION

INDEX

SCALE	BRIDGE FILE
N/A	008-75-04883 C
	DESIGNATION
	2001996
	SHEETS
	2 of 14
	CONTRACT
	B-43353


Plot: 6/9/2026 1:40 PM AM_PM
File: c:\pw_working\lochner-pw-01\dms39769\Sht Index Sheet.dgn
Model:$MODEL_NAME$

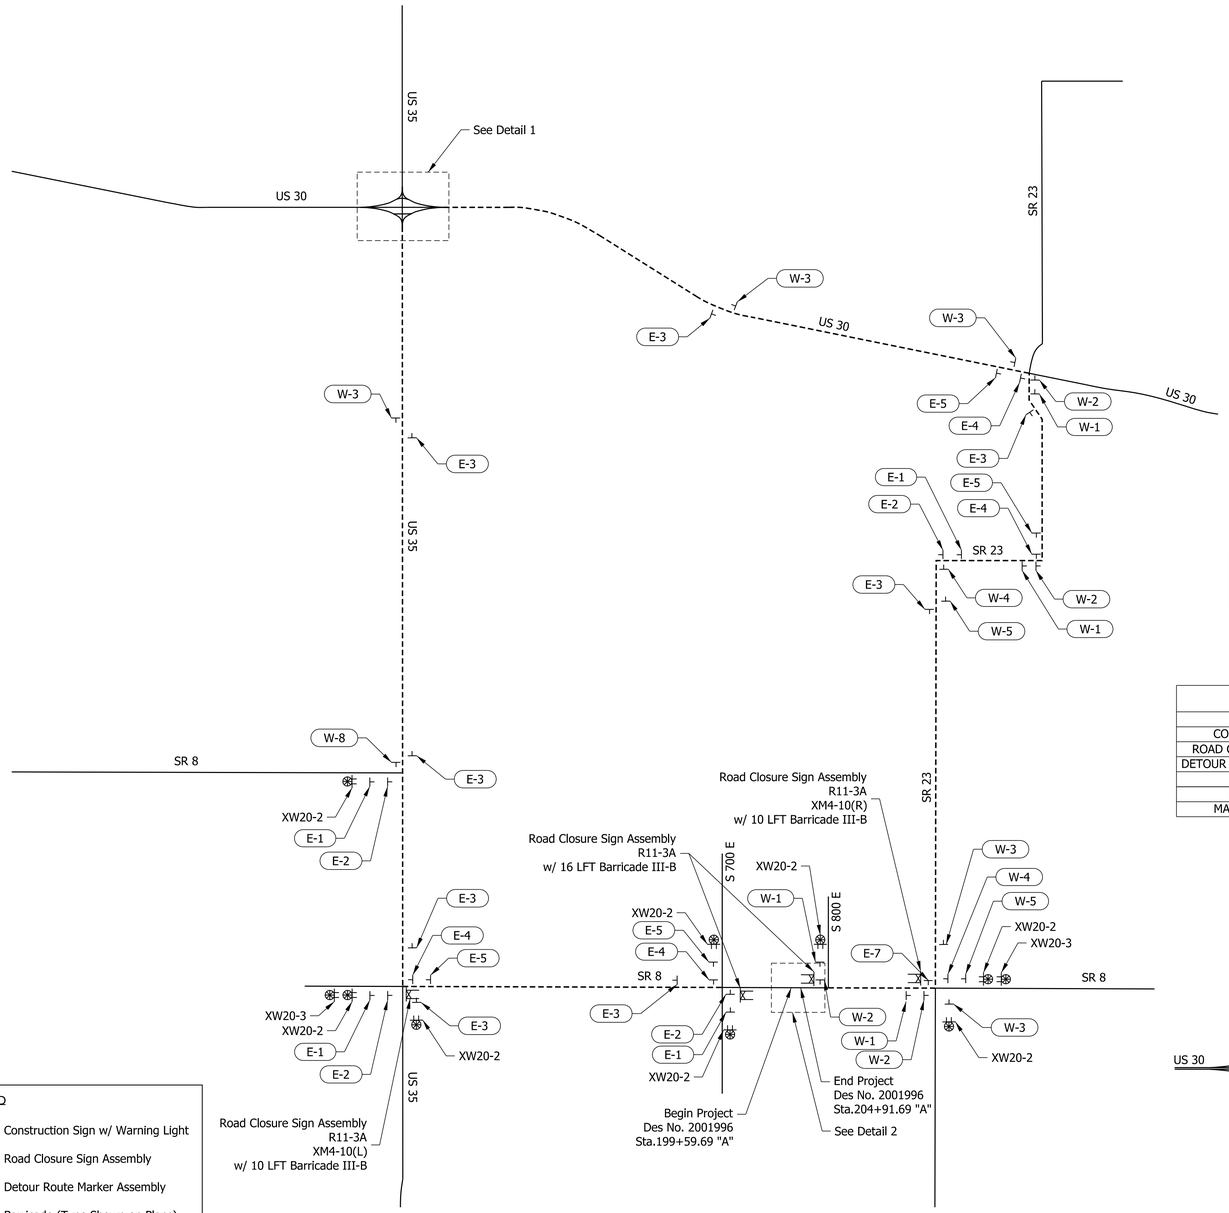


LEGEND


- Construction Sign w/ Warning Light
- Road Closure Sign Assembly
- Detour Route Marker Assembly
- Barricade (Type Shown on Plans)
- Detour Route

MOT DETAIL
N.T.S

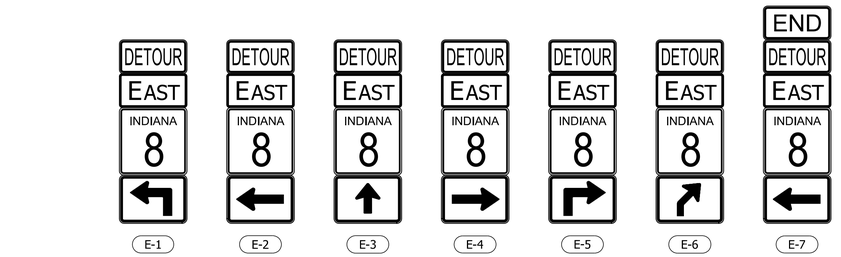


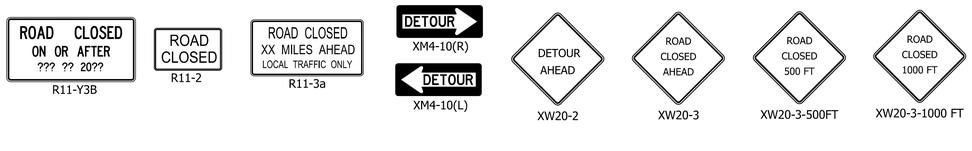


MOT SUMMARY TABLE		
ITEM	**UNIT**	**QTY**
CONSTRUCTION SIGN, A	EACH	16
ROAD CLOSURE SIGN ASSEMBLY	EACH	6
DETOUR ROUTE MARKER ASSEMBLY	EACH	52
BARRICADE, III-A	LFT	64
BARRICADE, III-B	LFT	52
MAINTAINING TRAFFIC	LS	1

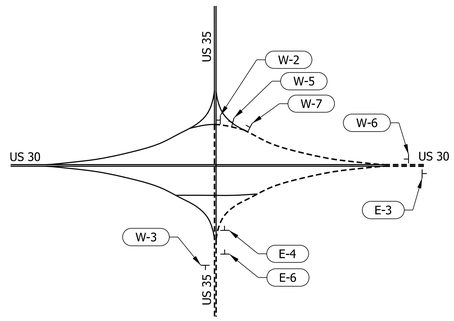

DETAIL 1
N.T.S

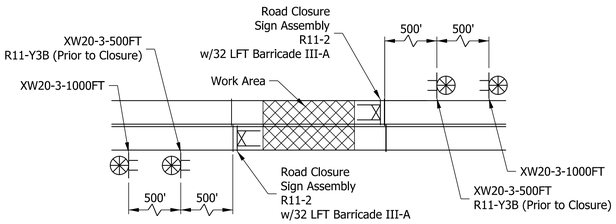

DETAIL 2
N.T.S

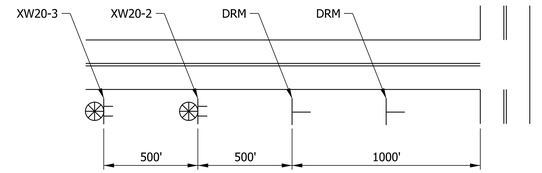

ADVANCE SIGNING DETAIL
N.T.S

MATTHEW EARL COCHRAN
REGISTERED
No. PE12200050
STATE OF INDIANA
PROFESSIONAL ENGINEER

RECOMMENDED FOR APPROVAL: MATTHEW COCHRAN — DESIGN ENGINEER — 6/9/2026 DATE

DESIGNED: YD 06/01/2022 | DRAWN: YD 06/01/2022

CHECKED: JS 06/01/2022 | CHECKED: JS 06/01/2022


INDIANA
DEPARTMENT OF TRANSPORTATION

MAINTENANCE OF TRAFFIC

SCALE	BRIDGE FILE
N.T.S.	008-75-04883 C
	DESIGNATION
	2001996
	SHEETS
	3 of 14
	CONTRACT
	B-43353

Plot: 6/9/2026 1:49 PM AM_PM

File: c:\pw_working\lochner-pw-01\dms39769\Maintenance of Traffic.dgn
Model:$MODEL_NAME$

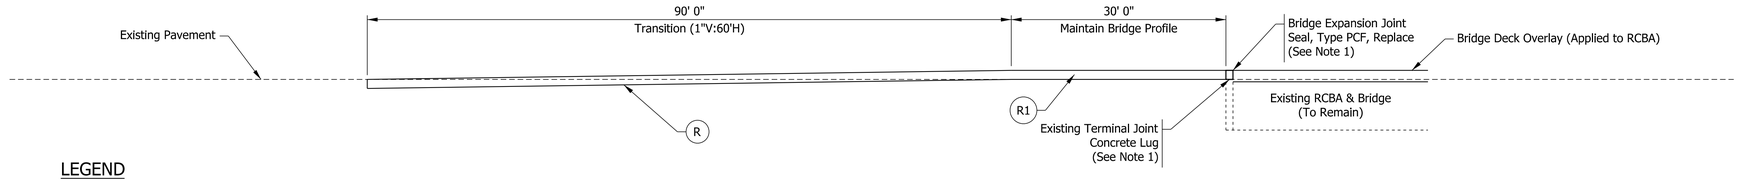


TRANSITION MILLING DETAIL

N.T.S.

LEGEND


- (R) Transitioning HMA Pavement consisting of: 165 lbs/syd QC/QA-HMA, 3, 58S, Surface, 9.5 mm on Milling, Transition
- (R1) Resurfacing HMA Pavement consisting of: 165 lbs/syd QC/QA-HMA, 3, 58S, Surface, 9.5 mm on Milling, Scarification
- (40) Line, Multi-Component, Solid, White, 6 in.
- (41) Line, Multi-Component, Solid, Yellow, 6 in.
- (43) Line, Multi-Component, Broken, Yellow, 6 in.
- * Match Existing Paved Shoulder Width

Notes:
1. For additional bridge expansion joint replacement and concrete lug details, see Sheet 10.
2. Place tack coat between all HMA layers. All intermediate and surface joints shall have Joint Adhesive applied.

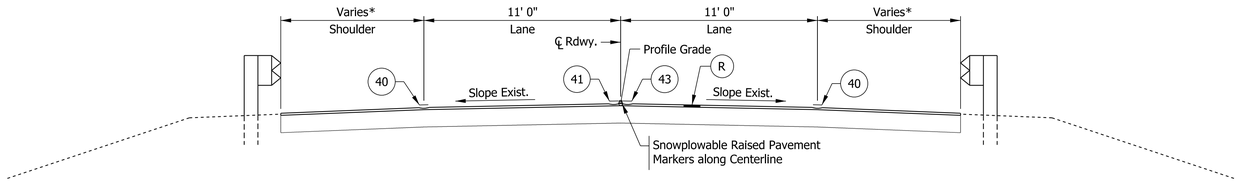

ROADWAY TYPICAL SECTION

Scale: 1/4" = 1'-0"
Sta. 199+29.69 to 200+49.69 and
Sta. 203+71.69 to 204+91.69

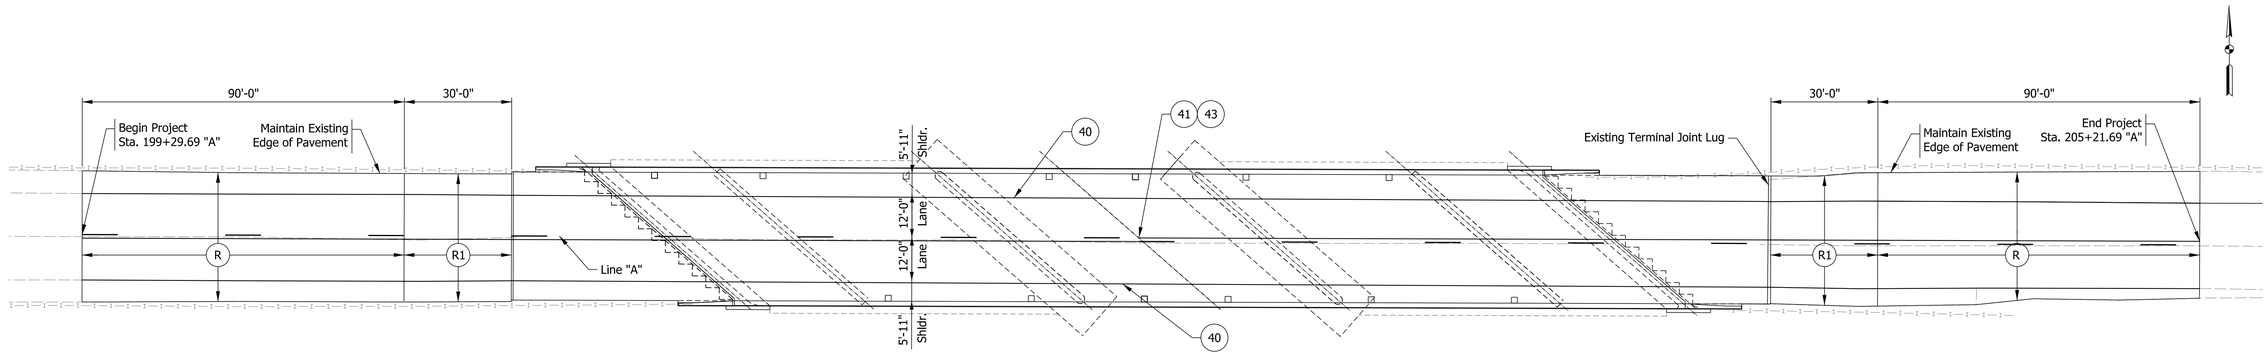

ROADWAY DETAILS

Scale: 1" = 20'-0"

MATTHEW EARL COCHRAN
REGISTERED
No. PE12200050
STATE OF INDIANA
PROFESSIONAL ENGINEER

RECOMMENDED FOR APPROVAL: MATTHEW COCHRAN — DESIGN ENGINEER — 6/9/2026 DATE

DESIGNED: YD 06/01/2022 | DRAWN: YD 06/01/2022


CHECKED: JS 06/01/2022 | CHECKED: JS 06/01/2022


INDIANA
DEPARTMENT OF TRANSPORTATION

ROADWAY DETAILS

SCALE	BRIDGE FILE
AS NOTED	008-75-04883 C
	DESIGNATION
	2001996
	SHEETS: 4 of 14
	CONTRACT: B-43353

Plot: 6/9/2023 1:58 PM AM_PM
File: c:\pw_working\lochner-pw-01\dms39769\Roadway Details.dgn
Model: $MODEL_NAME$

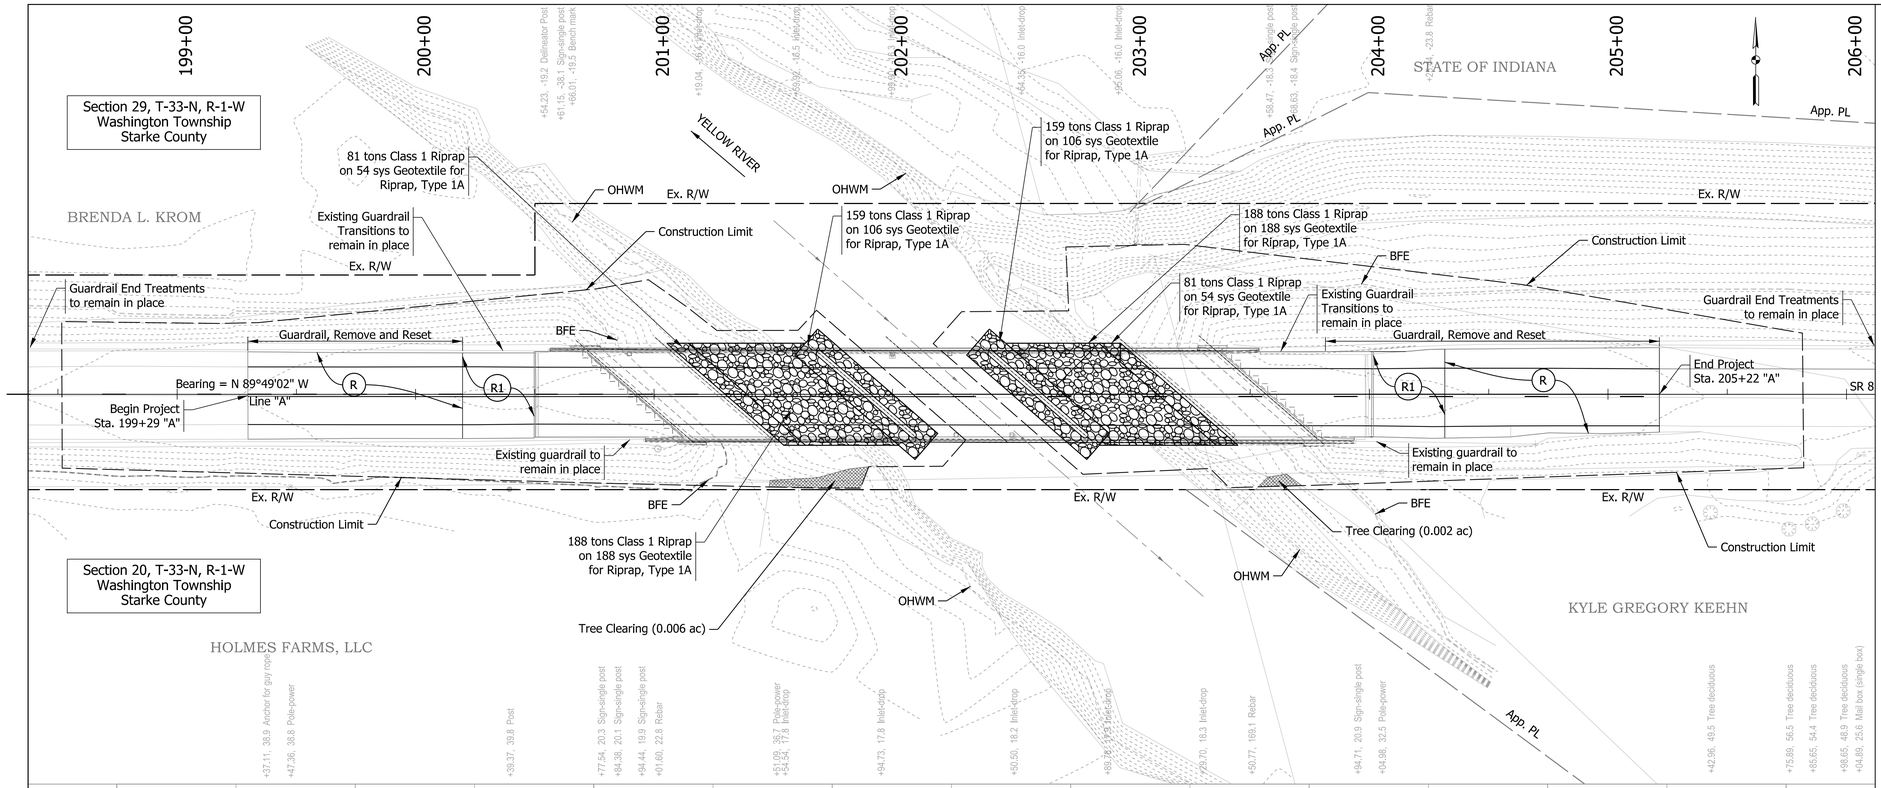

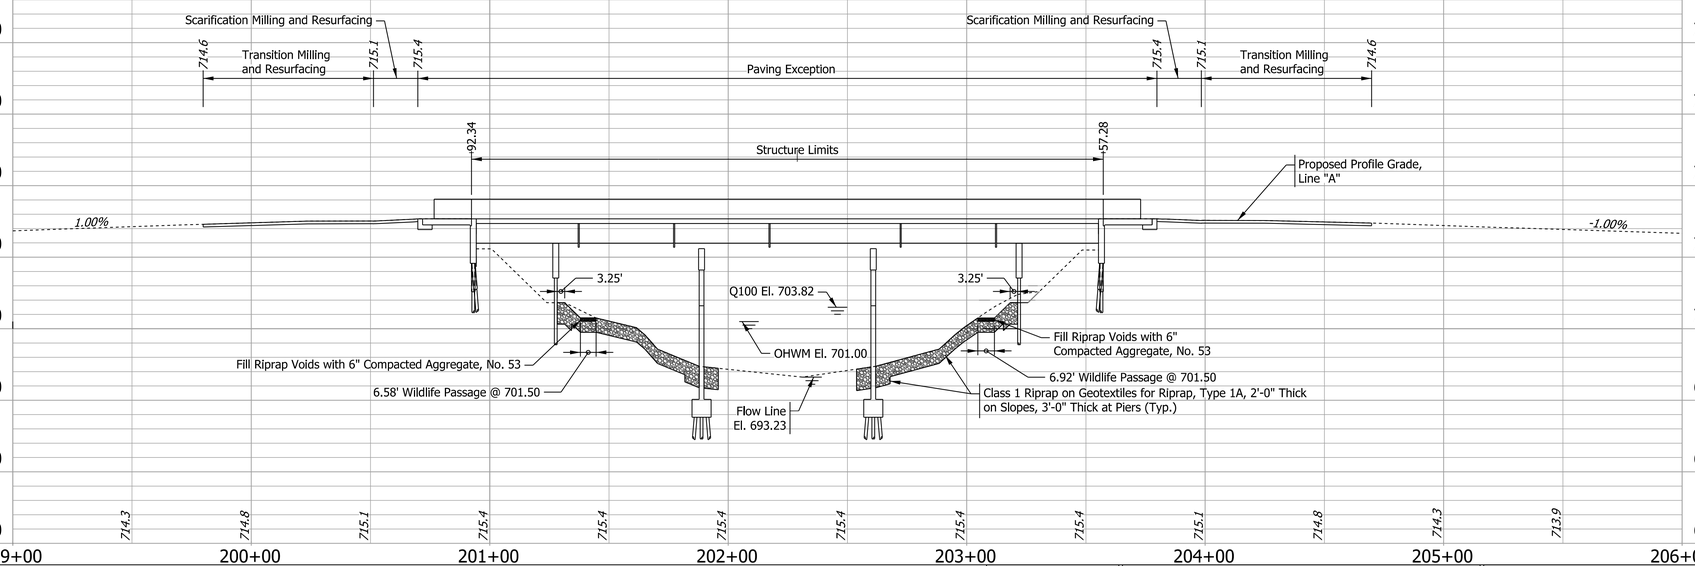

EXISTING STRUCTURE

The existing structure (008-75-04883 B) is a 265'-9" long five span continuous composite steel beam bridge built in 1964 and reconstructed in 1997 with spans of 34'-6⅞" (Span A), 61'-1¾" (Span B), 72'-0" (Span C), 61'-1¾" (Span D) and 34'-6⅞" (Span E) and 35'-10" clear roadway reinforced concrete deck with wingwalls.

HYDRAULIC DATA

Drainage Area	=	337 sq mi
Design Discharge, Q100	=	4963 cfs
Velocity	=	8.42 ft/s
Q100 Elev.	=	703.82 ft
Estimated Scour Elev.	=	688.06 ft

HYDRAULIC SCOUR DATA

Q100 Discharge	=	4963 cfs
Q100 Elev.	=	703.82 ft
Velocity at Q100	=	8.42 ft/s
Scour Depth (Contraction)	=	0.74 ft
Scour Depth (Total)	=	5.54 ft
Low Scour Elev.	=	688.06 ft

CONTINUOUS COMPOSITE STEEL BEAM BRIDGE
5 SPANS: 34'-6⅞", 61'-1¾", 72'-0", 61'-1¾" & 34'-6⅞"
35'-10" CLEAR ROADWAY;
SKEW 49°00'00" LT.
S.R. 8 OVER YELLOW RIVER
STARKE COUNTY

(R) Resurfacing HMA Pavement consisting of: 165 lbs/Syd. QC/QA-HMA, 3, 70, Surface, 9.5 mm on Milling, Transition

(R1) Resurfacing HMA Pavement consisting of: 165 lbs/Syd. QC/QA-HMA, 3, 58S, Surface, 9.5 mm on Milling, Scarification

MATTHEW EARL COCHRAN REGISTERED No. PE12200050 STATE OF INDIANA PROFESSIONAL ENGINEER

RECOMMENDED FOR APPROVAL: MATTHEW COCHRAN, DESIGN ENGINEER, 6/9/2026

DESIGNED: YD 06/01/2022 | DRAWN: YD 06/01/2022

CHECKED: JS 06/01/2022 | CHECKED: JS 06/01/2022

INDIANA DEPARTMENT OF TRANSPORTATION

LAYOUT

HORIZONTAL SCALE	BRIDGE FILE
1" = 30'	008-75-04883 C
VERTICAL SCALE	DESIGNATION
1" = 10'	2001996
SHEETS	
5 of 14	
CONTRACT	
B-43353	

Plot: 6/9/2026 2:06 PM

File: c:\pw_working\lochner-pw-01\dms39769\Layout1.dgn
Model: $MODEL_NAME$

198+00 199+00 200+00 201+00 202+00 203+00 204+00 205+00 206+00

YELLOW RIVER

Ex. R/W
Ex. R/W
Ex. R/W
Ex. R/W
Ex. R/W
Ex. R/W

OHWM
BFE
Impervious Dike
Impervious Dike
OHWM
BFE
Perimeter Protection
Construction Limit
Line "A"
Construction Equipment Access
Begin Project Sta. 199+59.69 "A"
BFE
Dewatering Pump
Filter Bag w/ Secondary Containment
Construction Limit
Perimeter Protection
Construction Equipment Access
End Project Sta. 204+91.69 "A"
SR 8
Dewatering Intake
OHWM
Dewatering Intake
Filter Bag w/ Secondary Containment
BFE
Dewatering Pump
Construction Limit
Perimeter Protection
OHWM

TOP OF PIPE ELEV. = 707.17
12 IN. CMP (PIPE SILTED OVER, INVERT NOT LOCATED, ELEVATION AT SEDIMENT GRADE) ELEV. = 706.67
TOP OF PIPE ELEV. = 704.72
INV. 12 IN. CMP = 703.76
INV. 24 IN. CMP = 697.16 PIPE HAS BACKFLOW PREVENTER
TOP OF PIPE ELEV. = 699.11
INV. 24 IN. CMP = 698.08

THIS SITE DESIGNATED AS BEING CLEAR OF GAS AS MARKED. BY UTILITY. LOCATORS. BY PAINT MARKS "OK" ON THE GROUND OF THE SITE AT THIS LOCA

NO MARKINGS IN AREA

Disturbed Areas shall be reseeded with Mulched Seeding, Type R. Disturbed areas below the Q100 shall be reseeded with Seed Mixture, Floodplain.

Areas to be re-seeded with Floodplain Seed Mixture

MATTHEW EARL COCHRAN REGISTERED No. PE12200050 STATE OF INDIANA PROFESSIONAL ENGINEER

RECOMMENDED FOR APPROVAL *MATTHEW COCHRAN* DESIGN ENGINEER 6/9/2026 DATE

DESIGNED: YD 06/01/2022
DRAWN: YD 06/01/2022
CHECKED: JS 06/01/2022
CHECKED: JS 06/01/2022

INDIANA DEPARTMENT OF TRANSPORTATION

EROSION CONTROL PLAN


SCALE	BRIDGE FILE
1" = 30'	008-75-04883 C
	DESIGNATION
	2001996

SHEETS 6 of 14
CONTRACT B-43353


Plot: 6/9/2026 2:15 PM AM_PM

File: c:\pw_working\lochner-pw-01\dms39769\19848 EC.dgn
Model: $MODEL_NAME$

EXISTING STRUCTURE BUILT ON A 500' VERTICAL CURVE

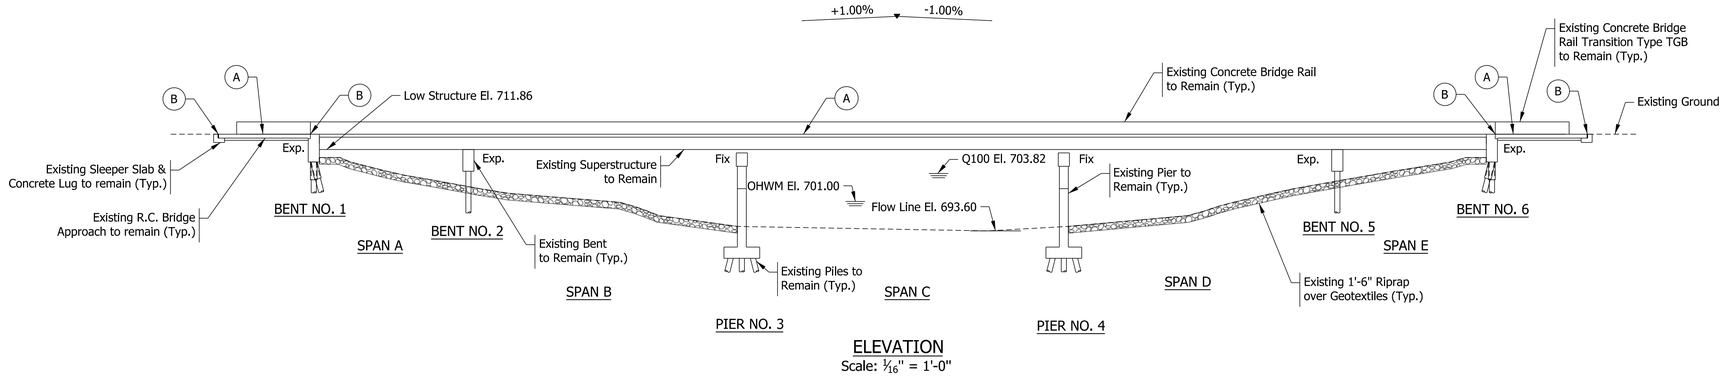

ELEVATION
Scale: 1/16" = 1'-0"

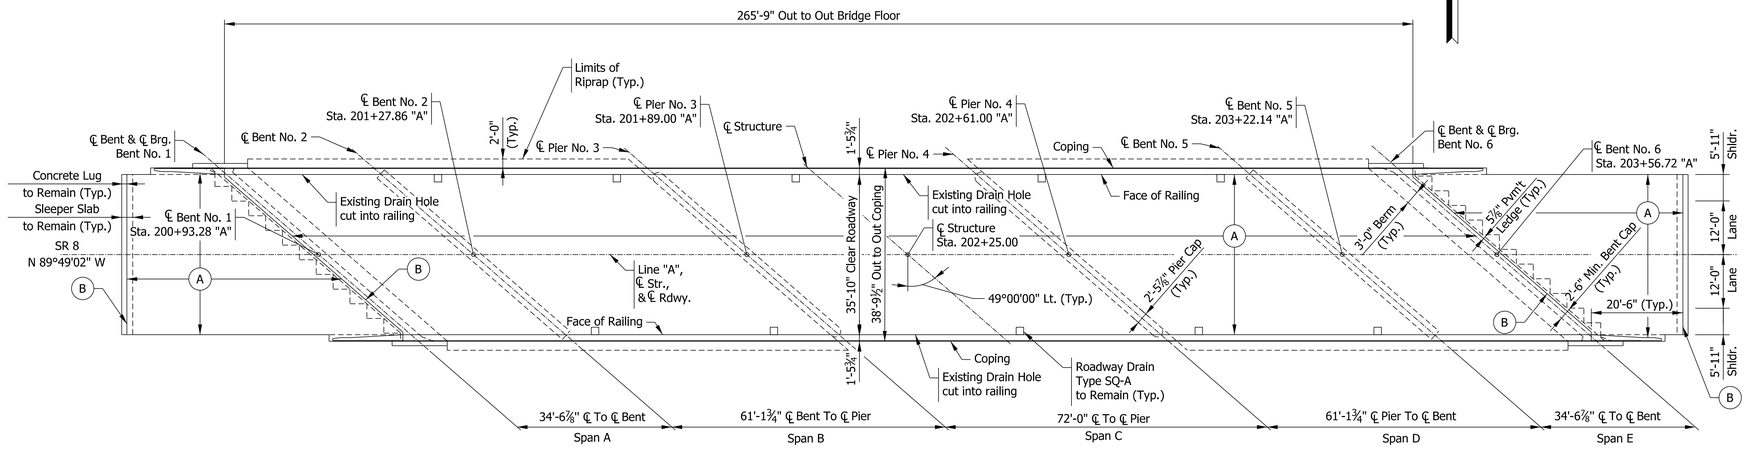

PLAN
Scale: 1/16" = 1'-0"

LEGEND:

- (A) Remove Existing Raised Pavement Markers, Remove Existing Concrete Surface (Avg. ¼"), and Perform Hydrodemolition on Bridge and R.C. Bridge Approaches.
- (B) Remove Existing Expansion Joint

NOTES:

1. For Proposed General Plan, General Notes, Design Data and Material Notes, See Sheet 8.
2. For Existing & Proposed Typical Section, See Sheet 9.

CONTINUOUS COMPOSITE STEEL BEAM BRIDGE
5 SPANS: 34'-6⅞", 61'-1¾", 72'-0", 61'-1¾" & 34'-6⅞"
35'-10" CLEAR ROADWAY;
SKEW 49°00'00" LT.
S.R. 8 OVER YELLOW RIVER
STARKE COUNTY

MATTHEW EARL COCHRAN REGISTERED No. PE12200050 STATE OF INDIANA PROFESSIONAL ENGINEER

RECOMMENDED FOR APPROVAL MATTHEW COCHRAN 6/9/2026
DESIGN ENGINEER DATE

DESIGNED: YD 06/01/2022 DRAWN: YD 06/01/2022
CHECKED: MEC 01/20/2026 CHECKED: MEC 01/20/2026


INDIANA DEPARTMENT OF TRANSPORTATION

GENERAL PLAN - EXISTING


SCALE	BRIDGE FILE
AS NOTED	008-75-04883 C
	DESIGNATION
	2001996
	SHEETS
	7 of 14
	CONTRACT
	B-43353

Plot: 6/9/2026 2:22 PM AM_PM
File: c:\pw_working\lochner-pw-01\dms39769\General Plan Existing.dgn
Model:$MODEL_NAME$

EXISTING STRUCTURE BUILT ON A 500' VERTICAL CURVE

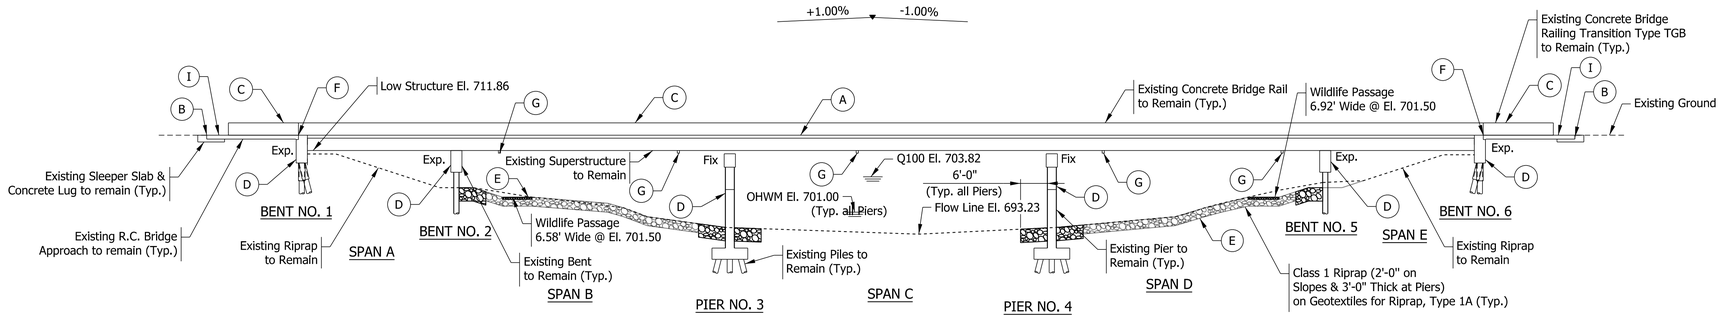

ELEVATION
Scale: 1/16" = 1'-0"

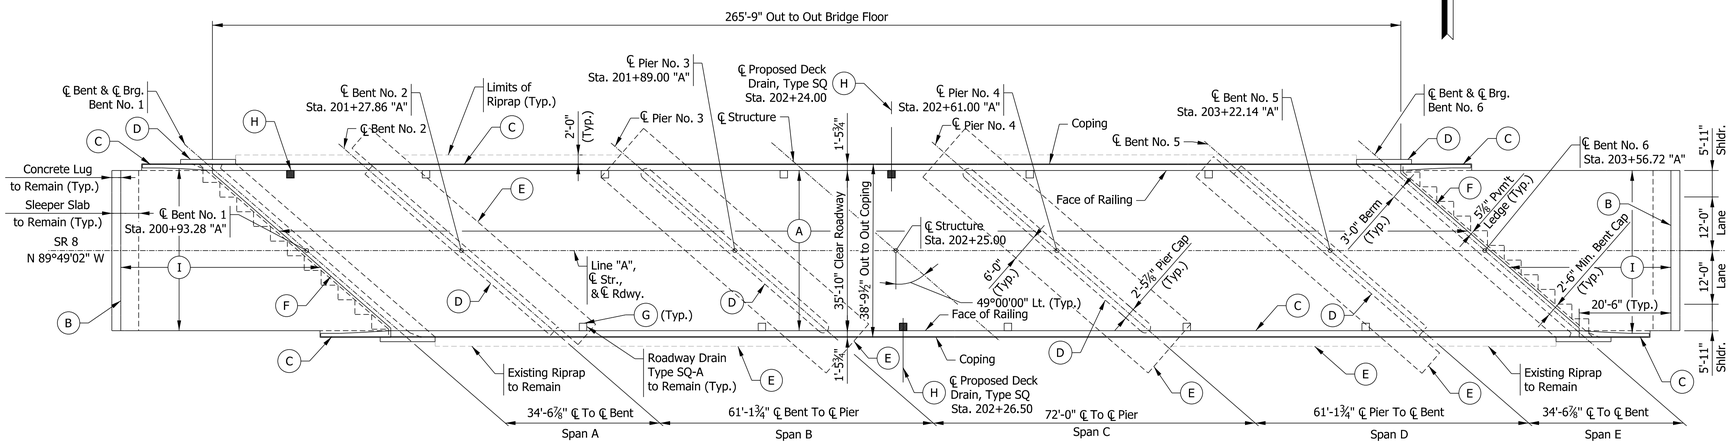

PLAN
Scale: 1/16" = 1'-0"

NOTES:

1. For Existing General Plan, See Sheet 7.
2. For Existing & Proposed Typical Section, See Sheet 9.
3. For proposed Longitudinal Section, See Sheet 10.
4. For Substructure Patching Details, See Sheets 11-13.

LEGEND:

- (A) Full Depth Patch any areas of deteriorated concrete on Bridge Deck and Install 1¾" Latex Modified Concrete Overlay
- (B) 36 Lft Bridge Expansion Joint, Seal PFC, Replace with Overlay Dams (See Proposed Longitudinal Section)
- (C) Surface Seal Bridge Railings and Railing Transitions and Install Top Mounted Barrier Delineators
- (D) Concrete Patching and Crack Sealing on Substructure Units (See Substructure Patching Details)
- (E) Establish New Class 1 Riprap Around Piers as shown. Re-establish Riprap between Bent 2 and Pier 3, as well as between Pier 4 and Bent 5 with additional Class 1 Riprap as needed. Construct wildlife passages. See Layout sheet for additional details.
- (F) Type I-A Joint, Saw and Seal with Overlay Dams (See Proposed Longitudinal Section)
- (G) Clean Existing Roadway Drains and Replace Casting Extensions
- (H) Install New Deck Drains, Type SQ (See Proposed Roadway Drain Details)
- (I) PCCP Patching Full Depth (Approx. 5 SYS @ Abut. 1 & 5 SYS @ Abut. 2) and Install 1¾" Latex Modified Concrete Overlay on Existing R.C. Bridge Approaches

GENERAL NOTES

Plans for the existing structures are on file in the Research and Document Section at the Indiana Department of Transportation as Bridge Files 008-75-04883 & 008-75-04883A, and 008-75-04883B and are available upon request. The original bridge and horizontal alignment was established under Project S-250(2)/Contract 6229.

Where new work is to be fitted to old work, the Contractor shall check and verify all dimensions, elevations, and conditions in the field, and report any errors or discrepancies to the Engineer and assume responsibility for their correctness and the fit of the new construction to the existing structure.

Reinforcing steel cover shall be 2 ½" in top and 1" minimum in bottom of floor slab, and 2" in all other parts, unless noted.

Surface Seal exposed faces of concrete railings and railing transitions. Estimated Quantity is 4,732 sft.

Portions of Present Structure to be Removed.

Data shown for existing bridge and subsequent geometry for proposed structure taken from original structure plans.

All reinforcing bars shall be epoxy coated unless otherwise noted. Restore damaged epoxy coating on existing epoxy coated bars that are to remain in place. Cost to be included in cost of concrete removal.

Chamfer exposed edges 1" unless otherwise noted.

DESIGN DATA

1997 Rehabilitation Allowable Design Stresses:

Class "C" Concrete	f'c = 4,000 psi
Class "A" Concrete	f'c = 3,500 psi
Class "B" Concrete	f'c = 3,000 psi
Reinforcing Steel (Grade 60)	fy = 60,000 psi

LIVE LOAD:
Original Structure designed for H20-S16-44 loading in accordance with 1961 A.A.S.H.O. Specifications.
The structure underwent rehabilitation in 1997. Modifications were designed for HS20-44 Loading with impact and distribution of loads in accordance with 1992 AASHTO Specifications and Interim Specifications.

DEAD LOAD:
Original Structure for actual weight plus 35 psf for future wearing surface. 1997 Rehabilitation designed for actual weight plus 35 psf (composite) for future wearing surface and 15 psf (Non-Composite) for permanent metal deck forms. 1997 Rehabilitation Slab designed with a structural depth of 6½".

MATERIAL NOTES:

Bridge Deck Overlay:
1¾" Latex Modified Portland Cement Concrete

CONTINUOUS COMPOSITE STEEL BEAM BRIDGE
5 SPANS: 34'-6⅞", 61'-1¾", 72'-0", 61'-1¾" & 34'-6⅞"
35'-10" CLEAR ROADWAY;
SKEW 49°00'00" LT.
S.R. 8 OVER YELLOW RIVER
STARKE COUNTY

MATTHEW EARL COCHRAN · REGISTERED · No. PE12200050 · STATE OF INDIANA · PROFESSIONAL ENGINEER

RECOMMENDED FOR APPROVAL: MATTHEW COCHRAN, DESIGN ENGINEER — 6/9/2026 DATE


DESIGNED: YD 06/01/2022 | DRAWN: YD 06/01/2022
CHECKED: MEC 01/20/2026 | CHECKED: MEC 01/20/2026

INDIANA
DEPARTMENT OF TRANSPORTATION


GENERAL PLAN - PROPOSED

SCALE	BRIDGE FILE
AS NOTED	008-75-04883 C
	DESIGNATION
	2001996
	SHEETS: 8 of 14
	CONTRACT: B-43353

Plot: 6/9/2026 2:29 PM AM_PM
File: c:\pw_working\lochner-pw-01\dms39769\General Plan Proposed.dgn
Model:$MODEL_NAME$

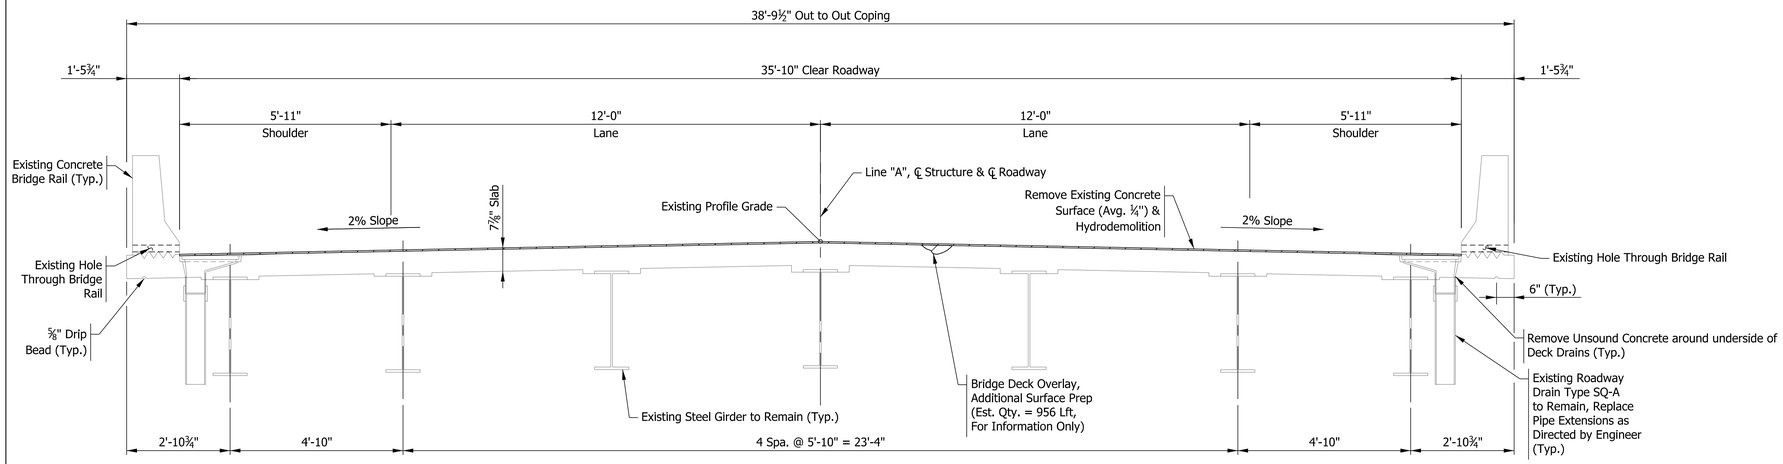

EXISTING TYPICAL SECTION
Scale: ½" = 1'-0"

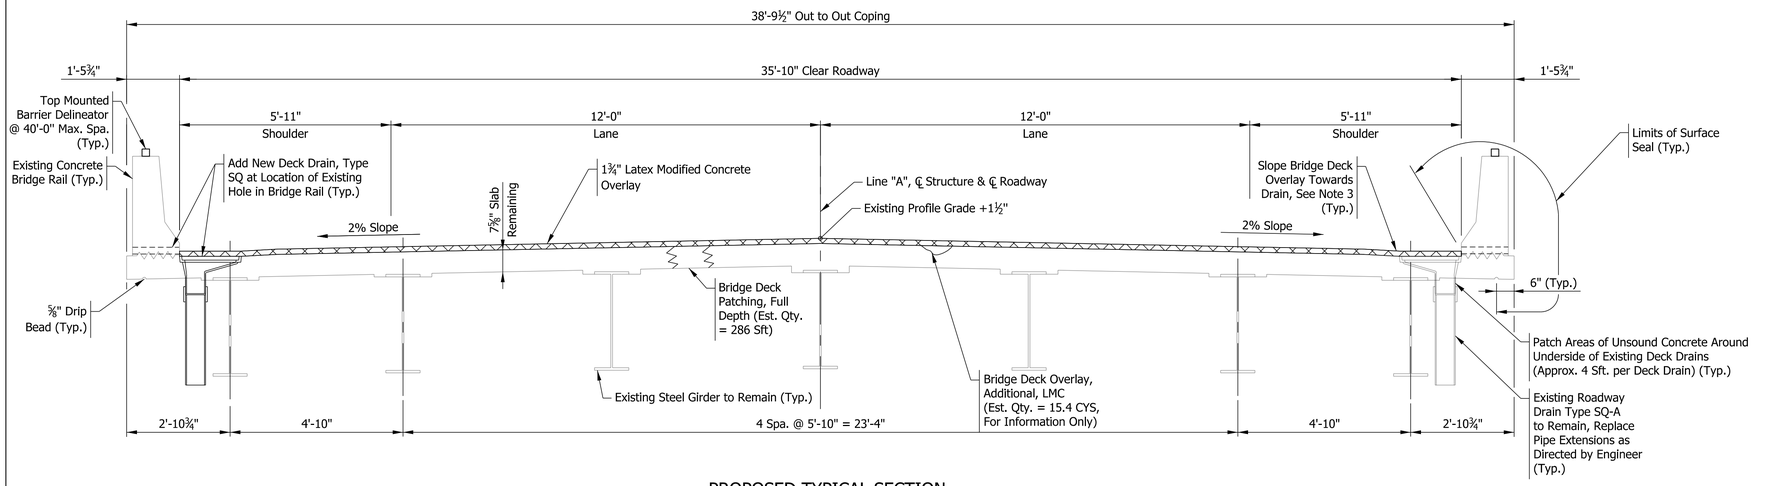

PROPOSED TYPICAL SECTION
Scale: ½" = 1'-0"

NOTES:

1. For Existing General Plan, See Sheet 7.
2. For Proposed General Plan, General Notes, Design Data, and Material Notes, See Sheet 8.
3. Transition overlay thickness to provide positive slope towards deck drains as required. For additional details, See Roadway Drain overlay Plan View on Sheet 10.

CONTINUOUS COMPOSITE STEEL BEAM BRIDGE
5 SPANS: 34'-6⅞", 61'-1¾", 72'-0", 61'-1¾" & 34'-6⅞"
35'-10" CLEAR ROADWAY;
SKEW 49°00'00" LT.
S.R. 8 OVER YELLOW RIVER
STARKE COUNTY

MATTHEW EARL COCHRAN — REGISTERED — No. PE12200050 — STATE OF INDIANA — PROFESSIONAL ENGINEER

RECOMMENDED FOR APPROVAL: MATTHEW COCHRAN — DESIGN ENGINEER — 6/9/2026 DATE


DESIGNED: YD 06/01/2022 | DRAWN: YD 06/01/2022
CHECKED: MEC 01/21/2026 | CHECKED: MEC 01/21/2026

INDIANA DEPARTMENT OF TRANSPORTATION


GENERAL PLAN - TYPICAL SECTION

SCALE	BRIDGE FILE
AS NOTED	008-75-04883 C
	DESIGNATION
	2001996
	SHEETS
	9 of 14
	CONTRACT
	B-43353


Plot: 6/9/2026 2:38 PM AM_PM
File: c:\pw_working\lochner-pw-01\dms39769\Typical Section.dgn
Model: $MODEL_NAME$

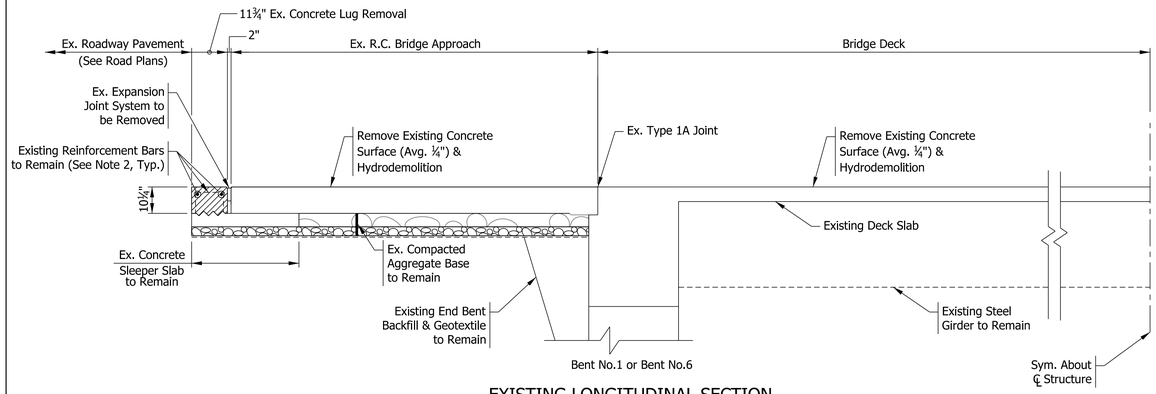


EXISTING LONGITUDINAL SECTION
N.T.S.

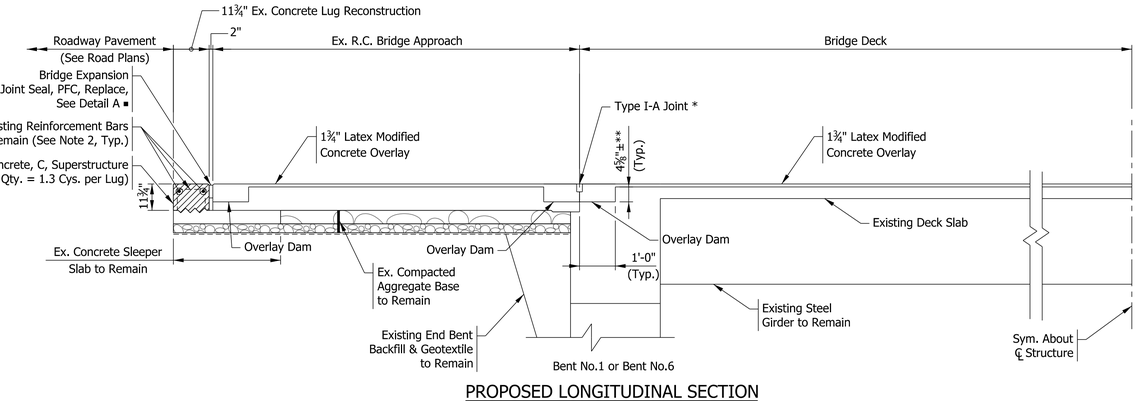


PROPOSED LONGITUDINAL SECTION
N.T.S.

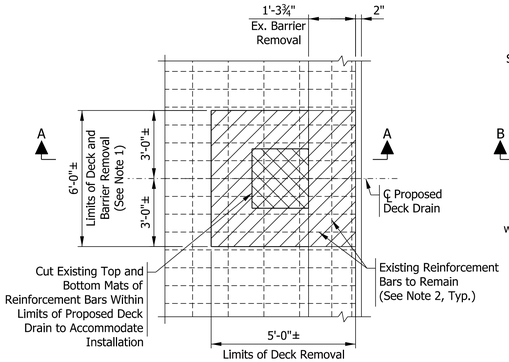

REMOVAL PLAN

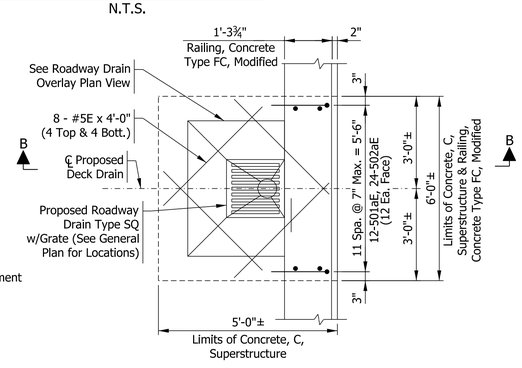

PROPOSED PLAN
(Existing Reinforcement Not Shown for Clarity)

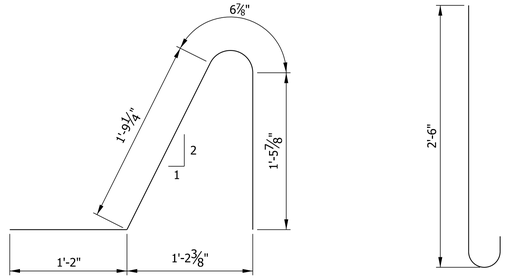


501aE x 5'-0"


502aE x 3'-1"

BAR BENDING DETAILS
N.T.S

BILL OF MATERIALS BARRIER & SUPERSTRUCTURE (THREE DECK DRAIN INSTALLATIONS & CONCRETE LUG REPLACEMENT)			
EPOXY - COATED REINFORCING BARS			
SIZE & MARK	NO. OF BARS	LENGTH	WEIGHT (Lbs)
#5	24	4'-0"	
501aE	36	5'-0"	
502aE	72	3'-1"	
		Total #5	520
Total Epoxy-Coated Reinforcing Bars			520
CONCRETE			
Concrete, C, Superstructure			
Deck Drain Pour (3 x 0.73 Cys)			2.2 Cys
Concrete Lug Pour (2 x 1.3 Cys)			2.6 Cys
Total Concrete, C, Superstructure			4.8 Cys
MISCELLANEOUS			
Railing, Concrete Type FC, Modified (3 x 0.6 Cys)			1.8 Cys
Grates, Basins, and Fittings, Cast Iron			3 Ea
Pipe Roadway Drain, Casting Extension			13 Ea

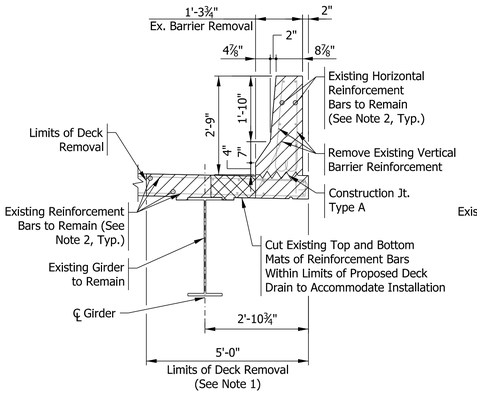


SECTION A-A

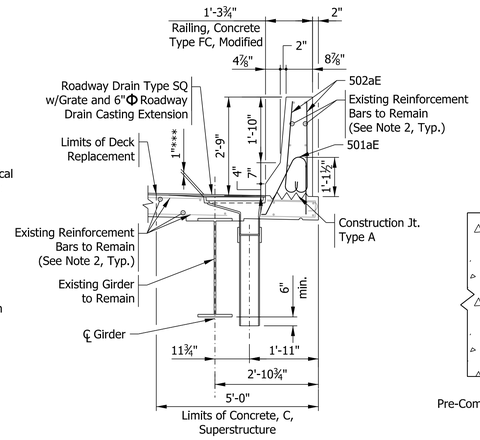


SECTION B-B

PROPOSED ROADWAY DRAIN DETAIL
N.T.S.

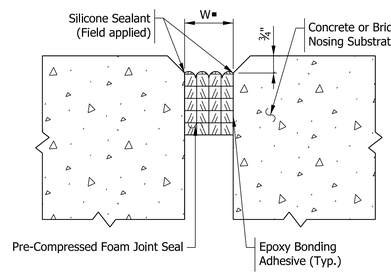

DETAIL A
N.T.S.

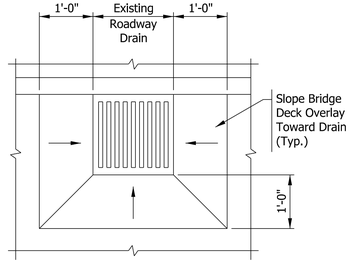

ROADWAY DRAIN OVERLAY PLAN VIEW
Scale: ¾" = 1'-0"

LEGEND:

* Contractor shall verify existing joint was constructed per plan (Bridge File 008-75-7883B) after removal of existing joint. If R.C. Bridge Approach is not cast against pavement ledge and/or connected to superstructure, inform the Engineer immediately to determine appropriate alternative for joint replacement.

** Measured from top of deck after deck removal. Provide 1" Clr. to Top Mat of Deck Reinforcement

*** Typical 3 Sides

■ Expansion Length = 132'-11"
Nominal Opening @ 60° F, W = 2" (Per Existing Plans)
Temperature Fall Movement ("A") = 1⅛" (Maximum Opening = 3⅛")
Temperature Rise Movement ("B") = ¾" (Minimum Opening = 1¼")
Total Thermal Movement = "A" + "B" = 1⅞"
(Thermal movements include load factor of 1.2 per AASHTO LRFD Specifications)

NOTES:

1. Use a pachometer to locate existing reinforcement bars. Adjust Removal limits as required to avoid reinforcement bars.
2. Protect, clean, straighten and repair epoxy coating for all exposed reinforcement that is to remain in place (incidental to removal item).
3. For Roadway Drain Type SQ Details, See Standard Drawings E 704-BDCG-03 and E 704-BDCG-04.
4. For Roadway Drain Casting Extension Pipe Details, See Standard Drawing E 715-BDCG-01.

MATTHEW EARL COCHRAN REGISTERED No. PE12200050 STATE OF INDIANA PROFESSIONAL ENGINEER

RECOMMENDED FOR APPROVAL MATTHEW COCHRAN 6/9/2026
DESIGN ENGINEER DATE


DESIGNED: YD 03/30/2023 | DRAWN: YD 03/30/2023
CHECKED: MEC 01/22/2026 | CHECKED: MEC 01/22/2026

INDIANA DEPARTMENT OF TRANSPORTATION


STRUCTURE DETAILS

SCALE	BRIDGE FILE
AS NOTED	008-75-04883 C
	DESIGNATION
	2001996
SHEETS	
10 of 14	
CONTRACT	
B-43353	


Plot: 6/9/2026 2:45 PM AM_PM
File: c:\pw_working\lochner-pw-01\dms39769\Structure Details.dgn
Model:$MODEL_NAME$

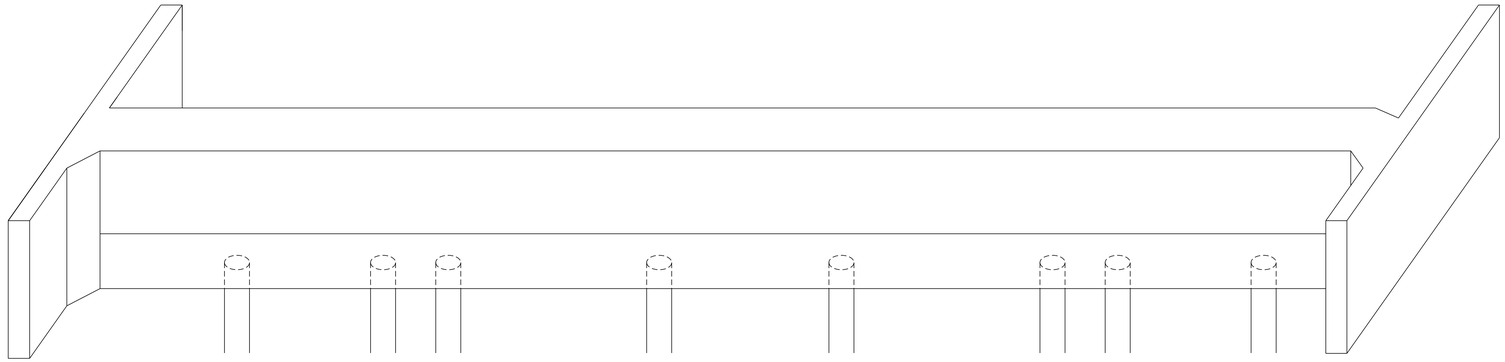

BENT #1
EAST FACE

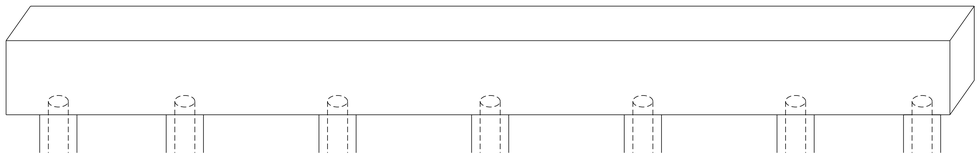

BENT #2
WEST FACE

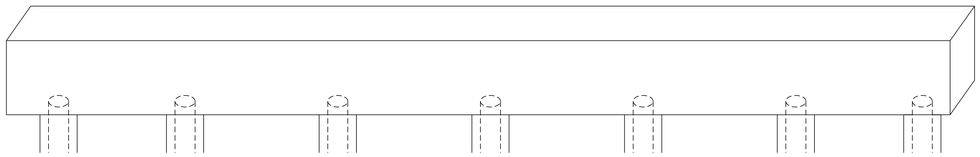

BENT #2
EAST FACE

EPOXY INJECTION CRACK PREPARATION & EPOXY INJECTION ADHESIVE ESTIMATED QUANTITIES			
Location	Quantity	Contingency	Total
BENT NO. 1	0 LFT/0 GAL	63 LFT/5 GAL	63 LFT/5 GAL
BENT NO. 2	0 LFT/0 GAL	55 LFT/5 GAL	55 LFT/5 GAL

PATCHING CONCRETE STRUCTURES ESTIMATED QUANTITIES			
Location	Area	Contingency	Total
BENT NO. 1	0 SFT	10 SFT	10 SFT
BENT NO. 2	0 SFT	10 SFT	10 SFT

PATCHING DETAILS - BENT #1 AND BENT #2

Not to Scale

LEGEND:

Approximate Limits of Concrete Patching Repair areas for estimating purposes only. Final Patch locations to be determined by the Engineer during construction.

Approximate Limits of Epoxy Injection Crack Sealing for estimating purposes only. Final crack sealing locations to be determined by the Engineer during construction.

MATTHEW EARL COCHRAN
REGISTERED
No. PE12200050
STATE OF INDIANA
PROFESSIONAL ENGINEER

RECOMMENDED FOR APPROVAL MATTHEW COCHRAN 6/9/2026
DESIGN ENGINEER DATE

DESIGNED: MDS 06/28/2023
DRAWN: MDS 06/28/2023
CHECKED: MEC 1/21/2026
CHECKED: MEC 1/21/2026

INDIANA
DEPARTMENT OF TRANSPORTATION

SUBSTRUCTURE PATCHING DETAILS

SCALE	BRIDGE FILE
AS NOTED	008-75-04883 C
	DESIGNATION
	2001996
	SHEETS
	11 of 14
	CONTRACT
	B-43353

Plot: 6/9/2026 2:52 PM AM_PM
File: c:\pw_working\lochner-pw-01\dms39770\Patching Details.dgn
Model: $MODEL_NAME$



PIER #3
WEST FACE



PIER #3
EAST FACE



PIER #4
WEST FACE



PIER #4
EAST FACE

EPOXY INJECTION CRACK PREPARATION & EPOXY INJECTION ADHESIVE ESTIMATED QUANTITIES			
Location	Quantity	Contingency	Total
PIER NO. 3	0 LFT/0 GAL	55 LFT/5 GAL	55 LFT/5 GAL
PIER NO. 4	0 LFT/0 GAL	55 LFT/5 GAL	55 LFT/5 GAL

PATCHING CONCRETE STRUCTURES ESTIMATED QUANTITIES			
Location	Area	Contingency	Total
PIER NO. 3	0 SFT	10 SFT	10 SFT
PIER NO. 4	0 SFT	10 SFT	10 SFT

PATCHING DETAILS - PIER #3 AND PIER #4

Not to Scale

LEGEND:

Approximate Limits of Concrete Patching Repair areas for estimating purposes only. Final Patch locations to be determined by the Engineer during construction.

Approximate Limits of Epoxy Injection Crack Sealing for estimating purposes only. Final crack sealing locations to be determined by the Engineer during construction.

MATTHEW EARL COCHRAN REGISTERED No. PE12200050 STATE OF INDIANA PROFESSIONAL ENGINEER

RECOMMENDED FOR APPROVAL MATTHEW COCHRAN 6/9/2026
DESIGN ENGINEER DATE


DESIGNED: MDS 06/28/2023 | DRAWN: MDS 06/28/2023
CHECKED: MEC 1/21/2026 | CHECKED: MEC 1/21/2026

INDIANA
DEPARTMENT OF TRANSPORTATION


SUBSTRUCTURE PATCHING DETAILS

SCALE	BRIDGE FILE
AS NOTED	008-75-04883 C
	DESIGNATION
	2001996
	SHEETS
	12 of 14
	CONTRACT
	B-43353


Plot: 6/9/2026 2:59 PM AM_PM
File: c:\pw_working\lochner-pw-01\dms39770\Patching Details-2.dgn
Model:$MODEL_NAME$

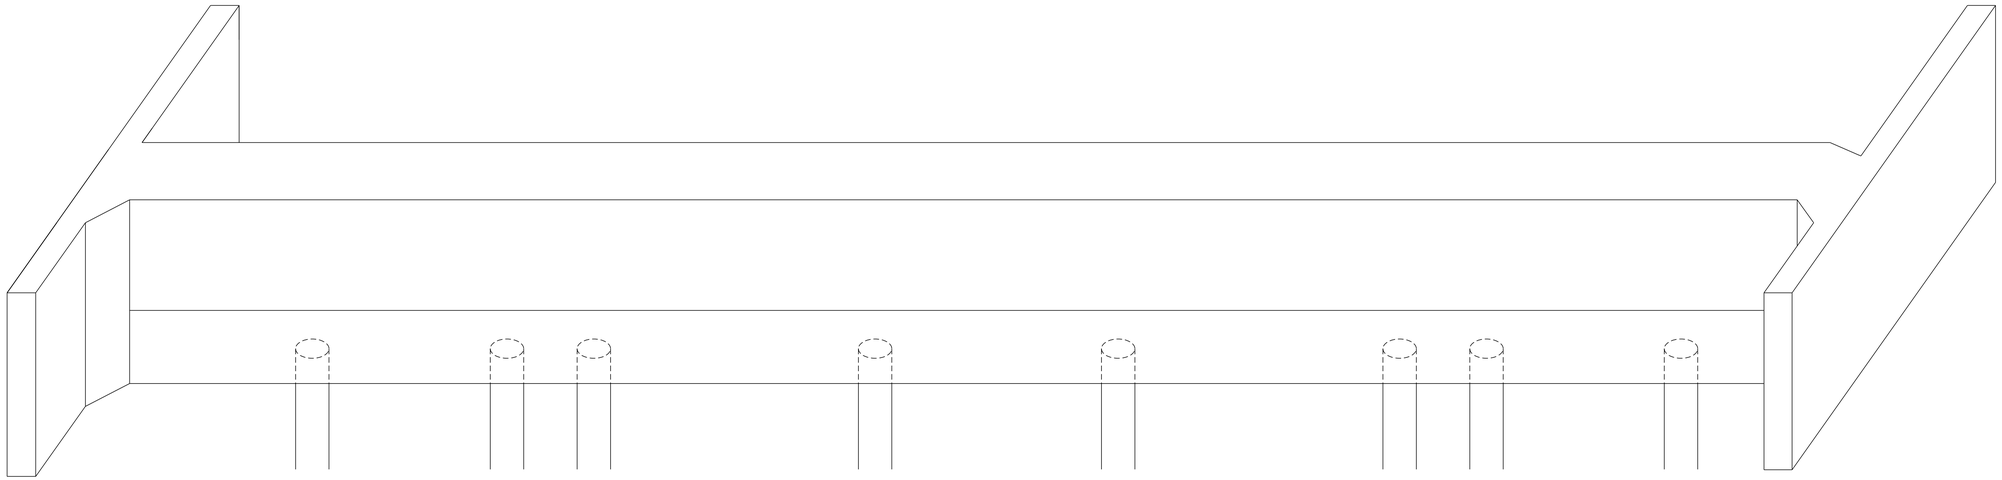

BENT #6
WEST FACE

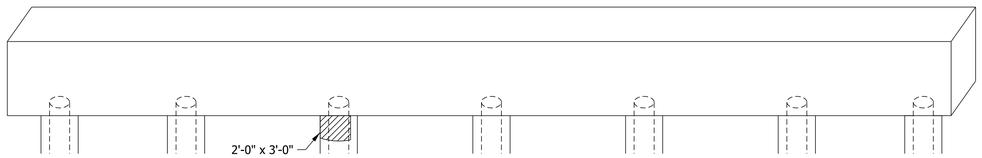

BENT #5
WEST FACE

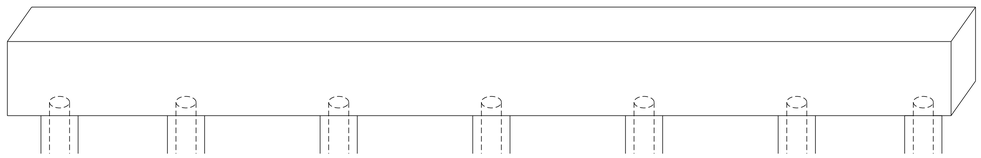

BENT #5
EAST FACE

EPOXY INJECTION CRACK PREPARATION & EPOXY INJECTION ADHESIVE ESTIMATED QUANTITIES			
Location	Quantity	Contingency	Total
BENT NO. 5	0 LFT/0 GAL	55 LFT/5 GAL	55 LFT/5 GAL
BENT NO. 6	0 LFT/0 GAL	63 LFT/5 GAL	63 LFT/5 GAL

PATCHING CONCRETE STRUCTURES ESTIMATED QUANTITIES			
Location	Area	Contingency	Total
BENT NO. 5	6 SFT	10 SFT	16 SFT
BENT NO. 6	0 SFT	10 SFT	10 SFT

PATCHING DETAILS - BENT #5 AND BENT #6

Not to Scale

LEGEND:

Approximate Limits of Concrete Patching Repair areas for estimating purposes only. Final Patch locations to be determined by the Engineer during construction.

Approximate Limits of Epoxy Injection Crack Sealing for estimating purposes only. Final crack sealing locations to be determined by the Engineer during construction.

MATTHEW EARL COCHRAN
REGISTERED
No. PE12200050
STATE OF INDIANA
PROFESSIONAL ENGINEER

RECOMMENDED FOR APPROVAL: MATTHEW COCHRAN — DESIGN ENGINEER — 6/9/2026 DATE

DESIGNED: MDS 06/28/2023 | DRAWN: MDS 06/28/2023

CHECKED: MEC 1/21/2026 | CHECKED: MEC 1/21/2026

INDIANA
DEPARTMENT OF TRANSPORTATION

SUBSTRUCTURE PATCHING DETAILS

SCALE	BRIDGE FILE
AS NOTED	008-75-04883 C
	DESIGNATION
	2001996
	SHEETS
	13 of 14
	CONTRACT
	B-43353

Plot: 6/9/2026 3:06 PM AM_PM

File: c:\pw_working\lochner-pw-01\dms39770\Patching Details-3.dgn
Model:$MODEL_NAME$

SUMMARY OF BRIDGE QUANTITIES

ITEM	CONCRETE C, SUPERSTRUCTURE	PRESENT STRUCTURE, REMOVE PORTIONS	PCCP PATCHING, FULL DEPTH	JOINTS IN PCCP, SAW AND SEAL	BARRIER, DELINEATOR	RIPRAP, CLASS 1	GEOTEXTILE FOR RIPRAP TYPE 1A	GRATES, BASINS, AND FITTINGS, CAST IRON	REINFORCING BARS, EPOXY COATED	RAILING, CONCRETE TYPE FC, MODIFIED	SURFACE SEAL	PATCHING CONCRETE STRUCTURES	PIPE, ROADWAY DRAIN CASTING EXTENSION	BRIDGE DECK OVERLAY, LATEX MODIFIED	HYDRODEMOLITION	BRIDGE DECK OVERLAY, ADDITIONAL SURFACE PREP	BRIDGE DECK OVERLAY, ADDITIONAL, LMC	BRIDGE DECK, REMOVE EXISTING CONCRETE SURFACE	LONGITUDINAL GROOVING	BRIDGE DECK PATCHING, FULL DEPTH	OVERLAY DAM	BRIDGE EXPANSION JOINT SEAL, PCF, REPLACE	EPOXY INJECTION, CRACK PREPARATION	EPOXY INJECTION, EPOXY INJECTION ADHESIVE	EPOXY INJECTION, FURNISHING EQUIPMENT
	CYS	LS	SYS	LFT	EACH	TON	SYS	EACH	LBS	CYS	LS	SFT	EACH	SYS	SYS	LFT	CYS	SYS	SYS	SFT	SFT	LFT	LFT	GAL	LS
SUPERSTRUCTURE	2.2	4 CYS*						3	520			40	13	1059	1059	732**	11.8**	1059	1059	286	110				1
BENT NO. 1												10											63	5	
BENT NO. 2						269	242					10											55	5	
PIER NO. 3						159	106					10											55	5	
PIER NO. 4						159	106					10											55	5	
BENT NO. 5						269	242					16											55	5	
BENT NO. 6												10											63	5	
R.C. BRIDGE APPROACH AT BENT NO. 1	1.3	2 CYS*	5	55										162	162	112**	1.8**	162	162		91	36			
R.C. BRIDGE APPROACH AT BENT NO. 6	1.3	2 CYS*	5	55										162	162	112**	1.8**	162	162		91	36			
CONCRETE BRIDGE RAILING					18					1.8	4732 SFT*														
TOTALS	4.8	8 CYS*	10	110	18	856	696	3	520	1.8	4732 SFT*	106	13	1383	1383	956**	15.4**	1383	1383	286	292	72	346	30	1

* Quantity Provided for Informational Purposes Only.
** Quantities included in Bridge Deck Overlay, Budget

PAVEMENT QUANTITIES AND APPROACH TABLE

LOCATION	DESCRIPTION	WIDTH	LENGTH	RADII	PAVEMENT REMOVAL	MILLING, TRANSITION	MILLING, ASPHALT, SCARIFICATION	SUBGRADE TREATMENT, TYPE IC	GEOTEXTILE FOR PAVEMENT, TYPE 2B	COMPACTED AGGREGATE NO. 53	SUBBASE FOR PCCP	HMA PATCHING FULL DEPTH TYPE D	HMA FOR ROADS			JOINT ADHESIVE	ASPHALT FOR TACK COAT	MULCHED SEEDING, TYPE R	FLOODPLAIN SEED MIXTURE
													QC/QA-HMA, 3, SBS, SURFACE, 9.5 MM						
													LBS PER SYD						
													165	275	550				
		FT	FT	FT	SYS	SYS	SYS	SYS	SYS	CYS	CYS	TONS	TONS	TONS	TONS	LFT	SYS	SYS	LBS
Line "A"	Transition					729	241						81			720	970	1757	10

PAVEMENT MARKINGS SUMMARY OF QUANTITIES

LOCATION	LINE, MULTI-COMPONENT			GROOVING FOR PAVEMENT MARKINGS	SNOWPLOWABLE RAISED PAVEMENT MARKER	SNOWPLOWABLE RAISED PAVEMENT MARKER, REMOVE
	SOLID WHITE 6 in	BROKEN YELLOW 6 in	SOLID YELLOW 6 in			
	LFT	LFT	LFT	LFT	EACH	EACH
TOTAL	1184	148	592	1924	16	16

TEMPORARY EROSION CONTROL TABLE

STATION	LOCATION			PERIMETER PROTECTION	PROTECTED RESOURCE FENCE	TEMPORARY SEEDING	TEMPORARY MULCH	REMARKS
	LEFT	MEDIAN	RIGHT					
				LFT	LFT	LB	TONS	
TOTAL				1170	240	158	3	

MATTHEW EARL COCHRAN — REGISTERED — No. PE12200050 — STATE OF INDIANA — PROFESSIONAL ENGINEER

RECOMMENDED FOR APPROVAL: MATTHEW COCHRAN — DESIGN ENGINEER — 6/9/2026 DATE

DESIGNED: YD 06/01/2022 | DRAWN: YD 06/01/2022

CHECKED: JS 06/01/2022 | CHECKED: JS 06/01/2022

INDIANA
DEPARTMENT OF TRANSPORTATION

SUMMARY OF QUANTITIES

SCALE	BRIDGE FILE
N/A	008-75-04883 C
	DESIGNATION
	2001996
	SHEETS
	14 of 14
	CONTRACT
	B-43353

Plot: 6/9/2026 3:14 PM AM_PM
File: c:\pw_working\lochner-pw-01\dms39769\Quantities_Summary.dgn
Model: $MODEL_NAME$